
备注：所有平面系统尺寸仅供参考，实际要以现场实际尺寸为准，施工方需审核图纸，如图纸与现场不符，需要及时向设计方反馈问题。

会签 | 建筑 | 电气 | 结构 | 暖通 | 给排水 | 动力

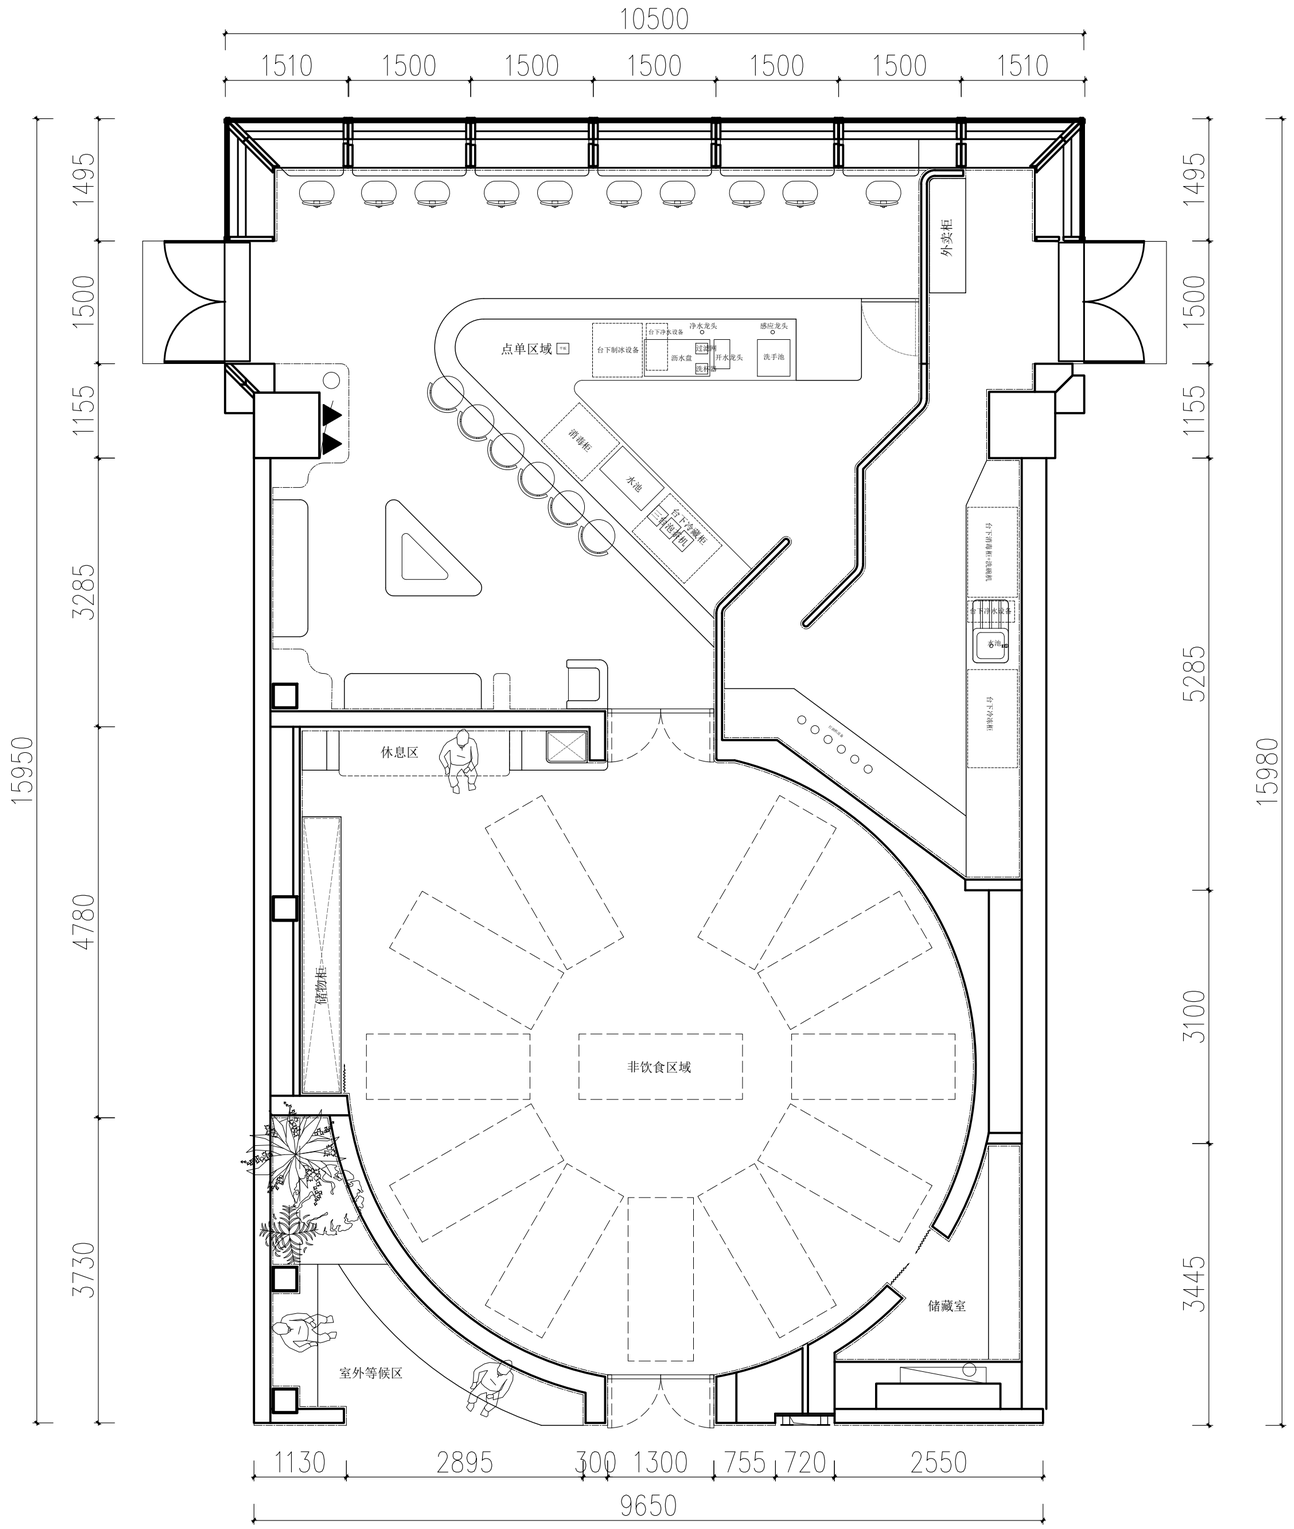

0F 1F ORIGONAL FLOOR PLAN 平面布置图 SCALE:1/75

ESSENZA ARMONIOSA
architecture interiors

中国 杭州
TEL: 180 6796 1470
FAX: 180 6796 1470

图注：Exegesis

建设单位 Construction unit

设计单位 Engineering design company

顾问单位 Consultant unit

工程名称 project name

FIONA SHANGHAI

审 定		
审 核		
校 对		
项目负责人		
设 计		
制 图		

图 名

平面布置图

图 号	PL-01
比 例	1:75
日 期	2026.08
专 业	装饰
设计阶段	施工图
版本编号	
设计编号	

出 图 盖 章

此设计图则之版权归杭州光几建筑室内设计有限公司所有 非得建筑师或设计师之书面批准 不得随意将任何部分翻印 切勿以比例量度此图 一切依图内数字所示为准承建人必须在工场核对图内所示数字之准则如发现有任何矛盾处应立即通知建筑师或设计师

ALL DESIGNS ARE THE SOLE PROPERTY OF HANGZHOU , LTD. AND CANNOT BE USED WITHOUT WRITTEN PERMISSION.DO NOT SCALE DRAWING. FIGURED DIMENSIONS ARE TO BE FOLLOWED. ALL MEASUREMENTS MUST BE CHECKED ON SITE BY THE CONTRACTOR. ANYDISCREPANCIES SHOULD BE REPORTED TO THE ARCHITECT OR DESIGNER

A3-420*297