
会签 | 建筑 | 电气 | 结构 | 暖通 | 给排水 | 动力

备注：所有平面系统尺寸仅供参考，实际要以现场实际尺寸为准，施工方需审核图纸，如图纸与现场不符，需要及时向设计方反馈问题。

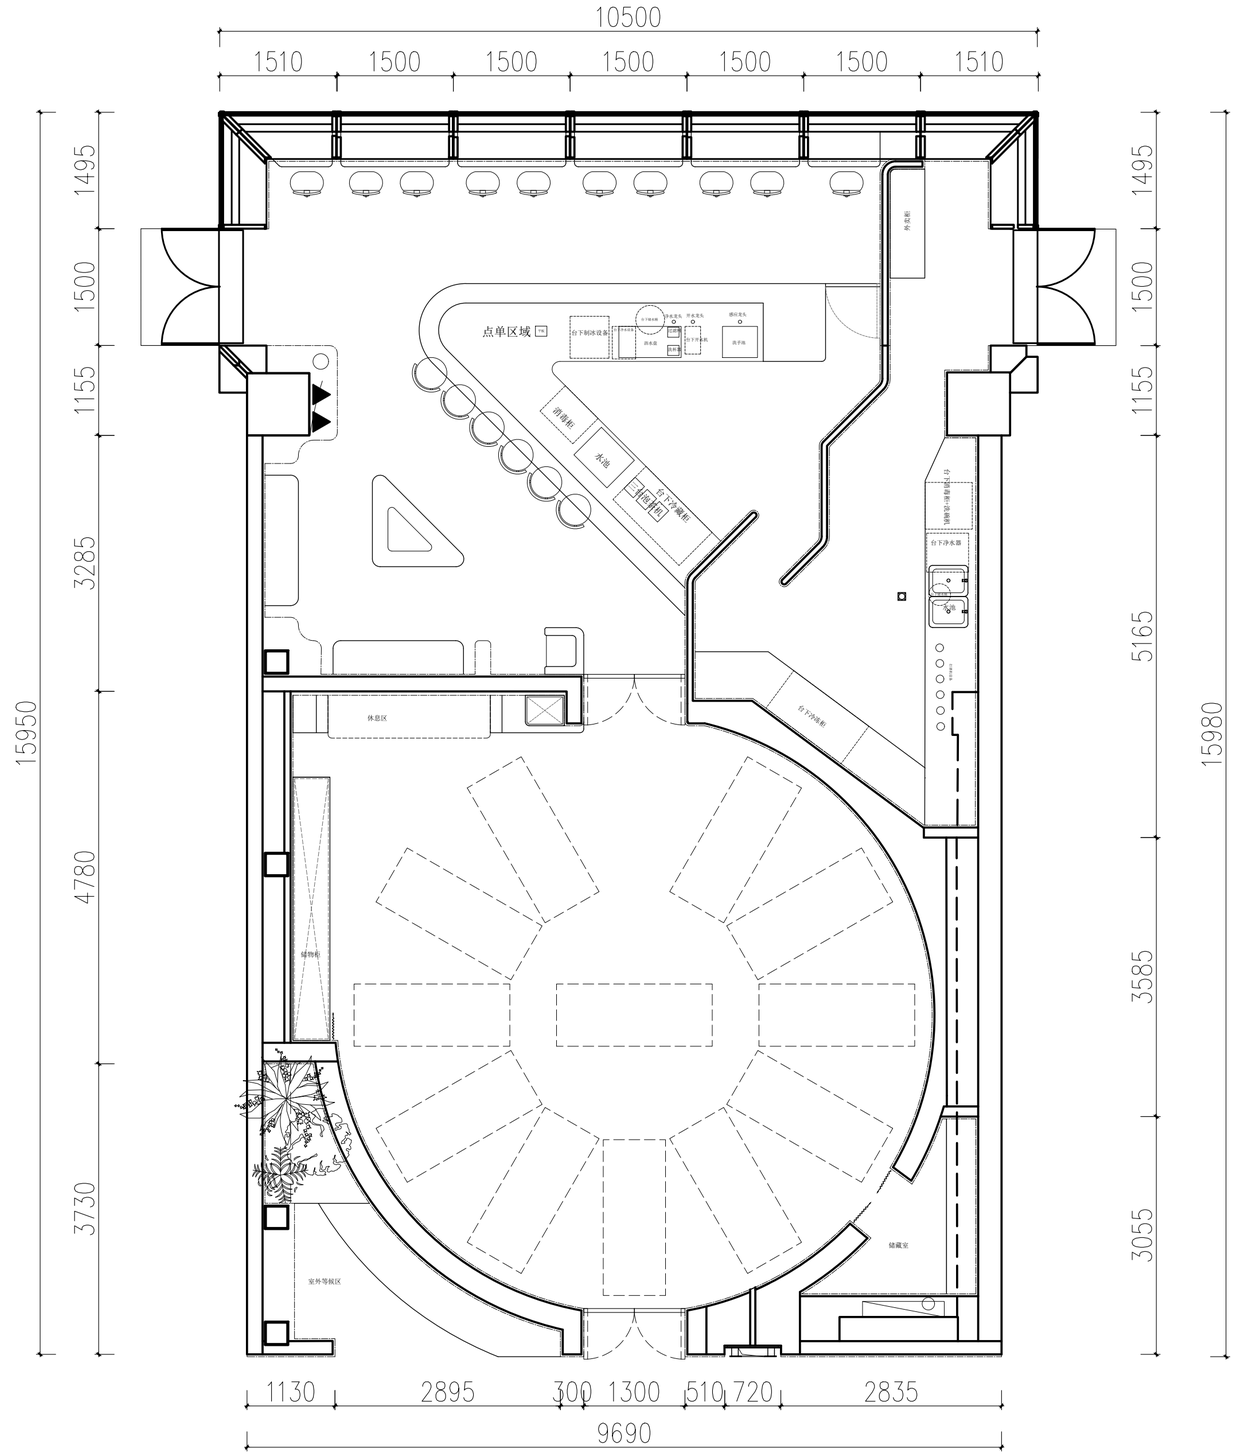

0F 1F ORIGONAL FLOOR PLAN 平面布置图 SCALE:1/75

ESSENZA ARMONIOSA
architecture interiors

中国 杭州
TEL: 180 6796 1470
FAX: 180 6796 1470

图注：Exegesis

建设单位 Construction unit

设计单位 Engineering design company

顾问单位 Consultant unit

工程名称 project name

FIONA SHANGHAI

审 定		
审 核		
校 对		
项目负责人		
设 计		
制 图		

图 名

平面布置图


图 号	PL-01
比 例	1:75
日 期	2026.08
专 业	装饰
设计阶段	施工图
版本编号	
设计编号	

出 图 盖 章

此设计图则之版权归杭州光几建筑室内设计有限公司所有 非得建筑师或设计师之书面批准 不得随意将任何部分翻印 切勿以比例量度此图 一切依图内数字所示为准承建人必须在工场核对图内所示数字之准则如发现有任何矛盾处应立即通知建筑师或设计师

ALL DESIGNS ARE THE SOLE PROPERTY OF HANGZHOU • LTD. AND CANNOT BE USED WITHOUT WRITTEN PERMISSION.DO NOT SCALE DRAWING. FIGURED DIMENSIONS ARE TO BE FOLLOWED. ALL MEASUREMENTS MUST BE CHECKED ON SITE BY THE CONTRACTOR. ANYDISCREPANCIES SHOULD BE REPORTED TO THE ARCHITECT OR DESIGNER.

A3-420*297

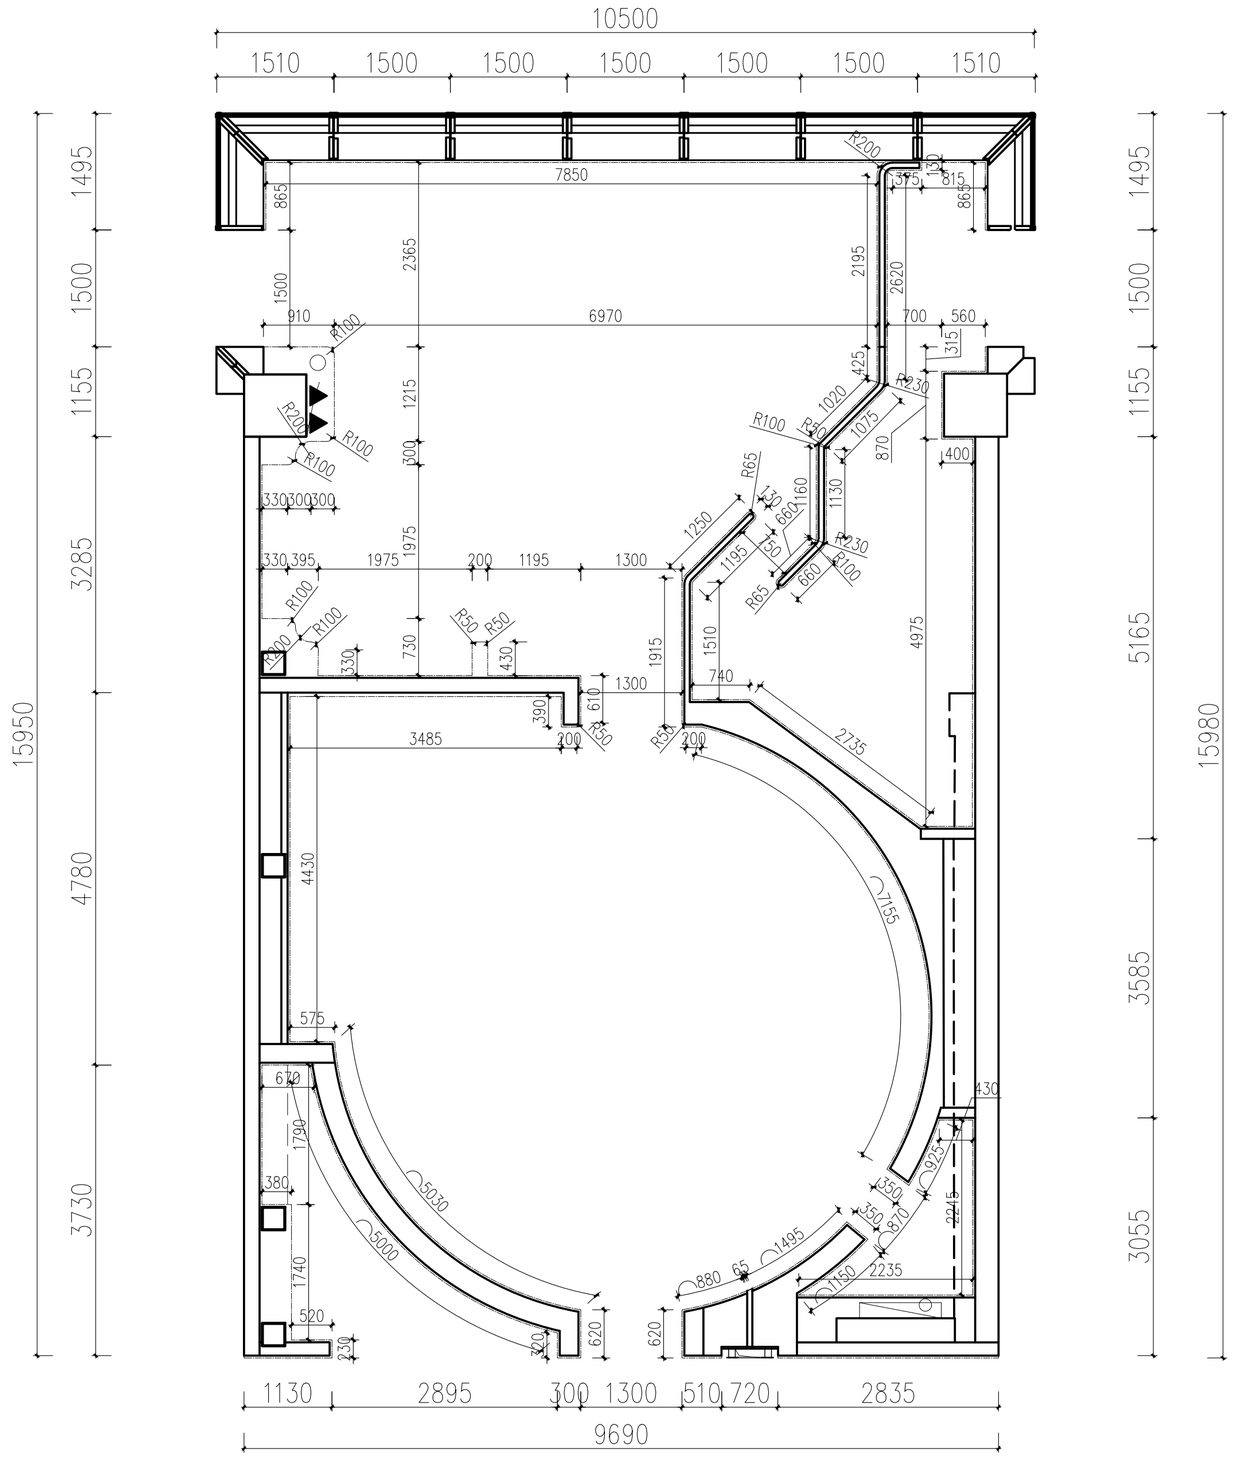

会	签
建筑	电气
结构	暖通
给排水	动力

ESSENZA ARMONIOSA
architecture
interiors

中国 杭州
TEL: 180 6796 1470
FAX: 180 6796 1470

图注: Exegesis

建设单位 Construction unit

设计单位 Engineering design company

顾问单位 Consultant unit

工程名称 project name

FIONA SHANGHAI

审 定		
审 核		
校 对		
项目负责人		
设 计		
制 图		

图 名

完成面尺寸图

图 号	PL-02
比 例	1:75
日 期	2026.08
专 业	装饰
设计阶段	施工图
版本编号	
设计编号	


出 图 盖 章

此设计图则之版权归杭州光几建筑室内设计有限公司所有 非得建筑师或设计师之书面批准 不得随意将任何部分翻印 切勿以比例量度此图 一切依图内数字所示为准承建人必须在工场核对图内所示数字之准则如发现有任何矛盾处应立即通知建筑师或设计师

ALL DESIGNS ARE THE SOLE PROPERTY OF HANGZHOU . LTD. AND I CANNOT BE USED WITHOUT WRITTEN PERMISSION.DO NOT SCALE DRAWING. FIGURED DIMENSIONS ARE TO BE FOLLOWED. ALL MEASUREMENTS MUST BE CHECKED ON SITE BY THE CONTRACTOR. ANYDISCREPANCIES SHOULD BE REPORTED TO THE ARCHITECT OR DESIGNER.

FD 1F FINISH DIMENSION PLAN 完成面尺寸图 SCALE:1/75

A3-420*297

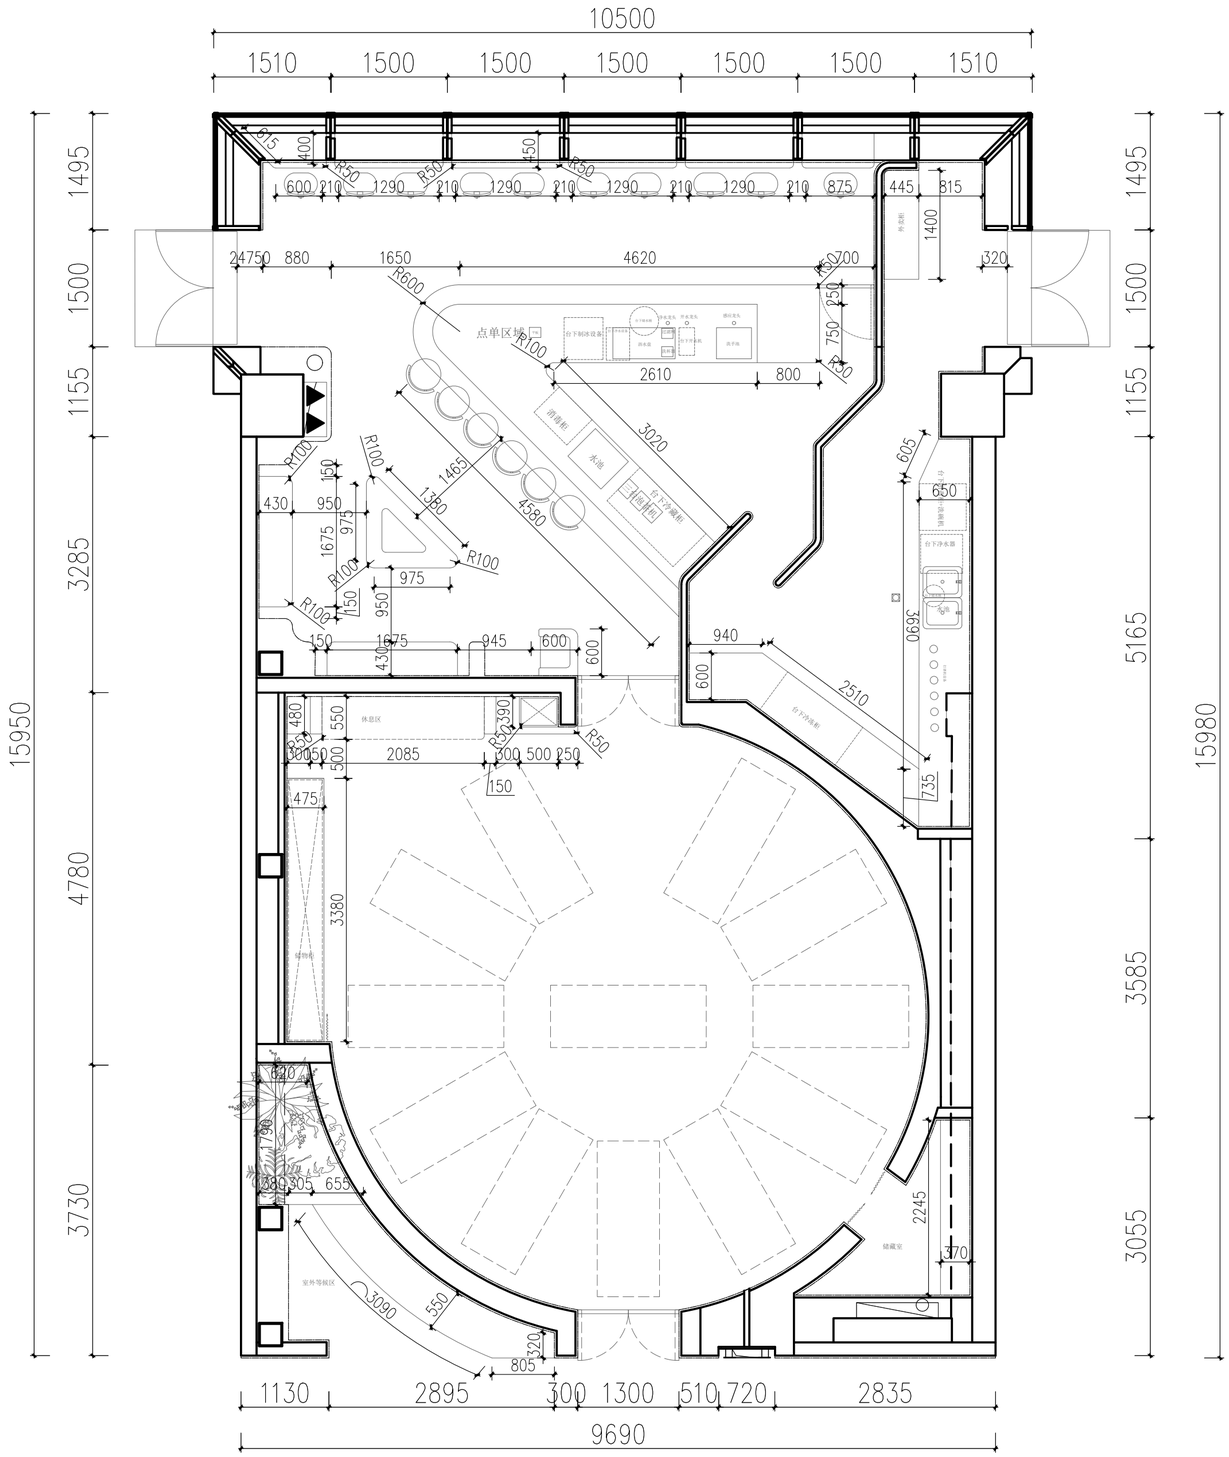

会签	建筑	电气
	结构	暖通
	给排水	动力

ESSENZA ARMONIOSA
architecture
interiors

中国 杭州
TEL: 180 6796 1470
FAX: 180 6796 1470

图注: Exegesis

建设单位 Construction unit

设计单位 Engineering design company

顾问单位 Consultant unit

工程名称 project name

FIONA SHANGHAI

审 定		
审 核		
校 对		
项目负责人		
设 计		
制 图		

图 名

家私定位图

图 号	PL-03
比 例	1:75
日 期	2026.08
专 业	装饰
设计阶段	施工图
版本编号	
设计编号	


出 图 盖 章

此设计图则之版权归杭州光几建筑室内设计有限公司所有 非得建筑师或设计师之书面批准 不得随意将任何部分翻印 切勿以比例量度此图 一切依图内数字所示为准承建人必须在工场核对图内所示数字之准则如发现有任何矛盾处应立即通知建筑师或设计师

ALL DESIGNS ARE THE SOLE PROPERTY OF HANGZHOU . LTD. AND I CANNOT BE USED WITHOUT WRITTEN PERMISSION.DO NOT SCALE DRAWING. FIGURED DIMENSIONS ARE TO BE FOLLOWED. ALL MEASUREMENTS MUST BE CHECKED ON SITE BY THE CONTRACTOR. ANYDISCREPANCIES SHOULD BE REPORTED TO THE ARCHITECT OR DESIGNER.

FD 1f FINISH DIMENSION PLAN 家私定位 SCALE:1/75

A3-420*297

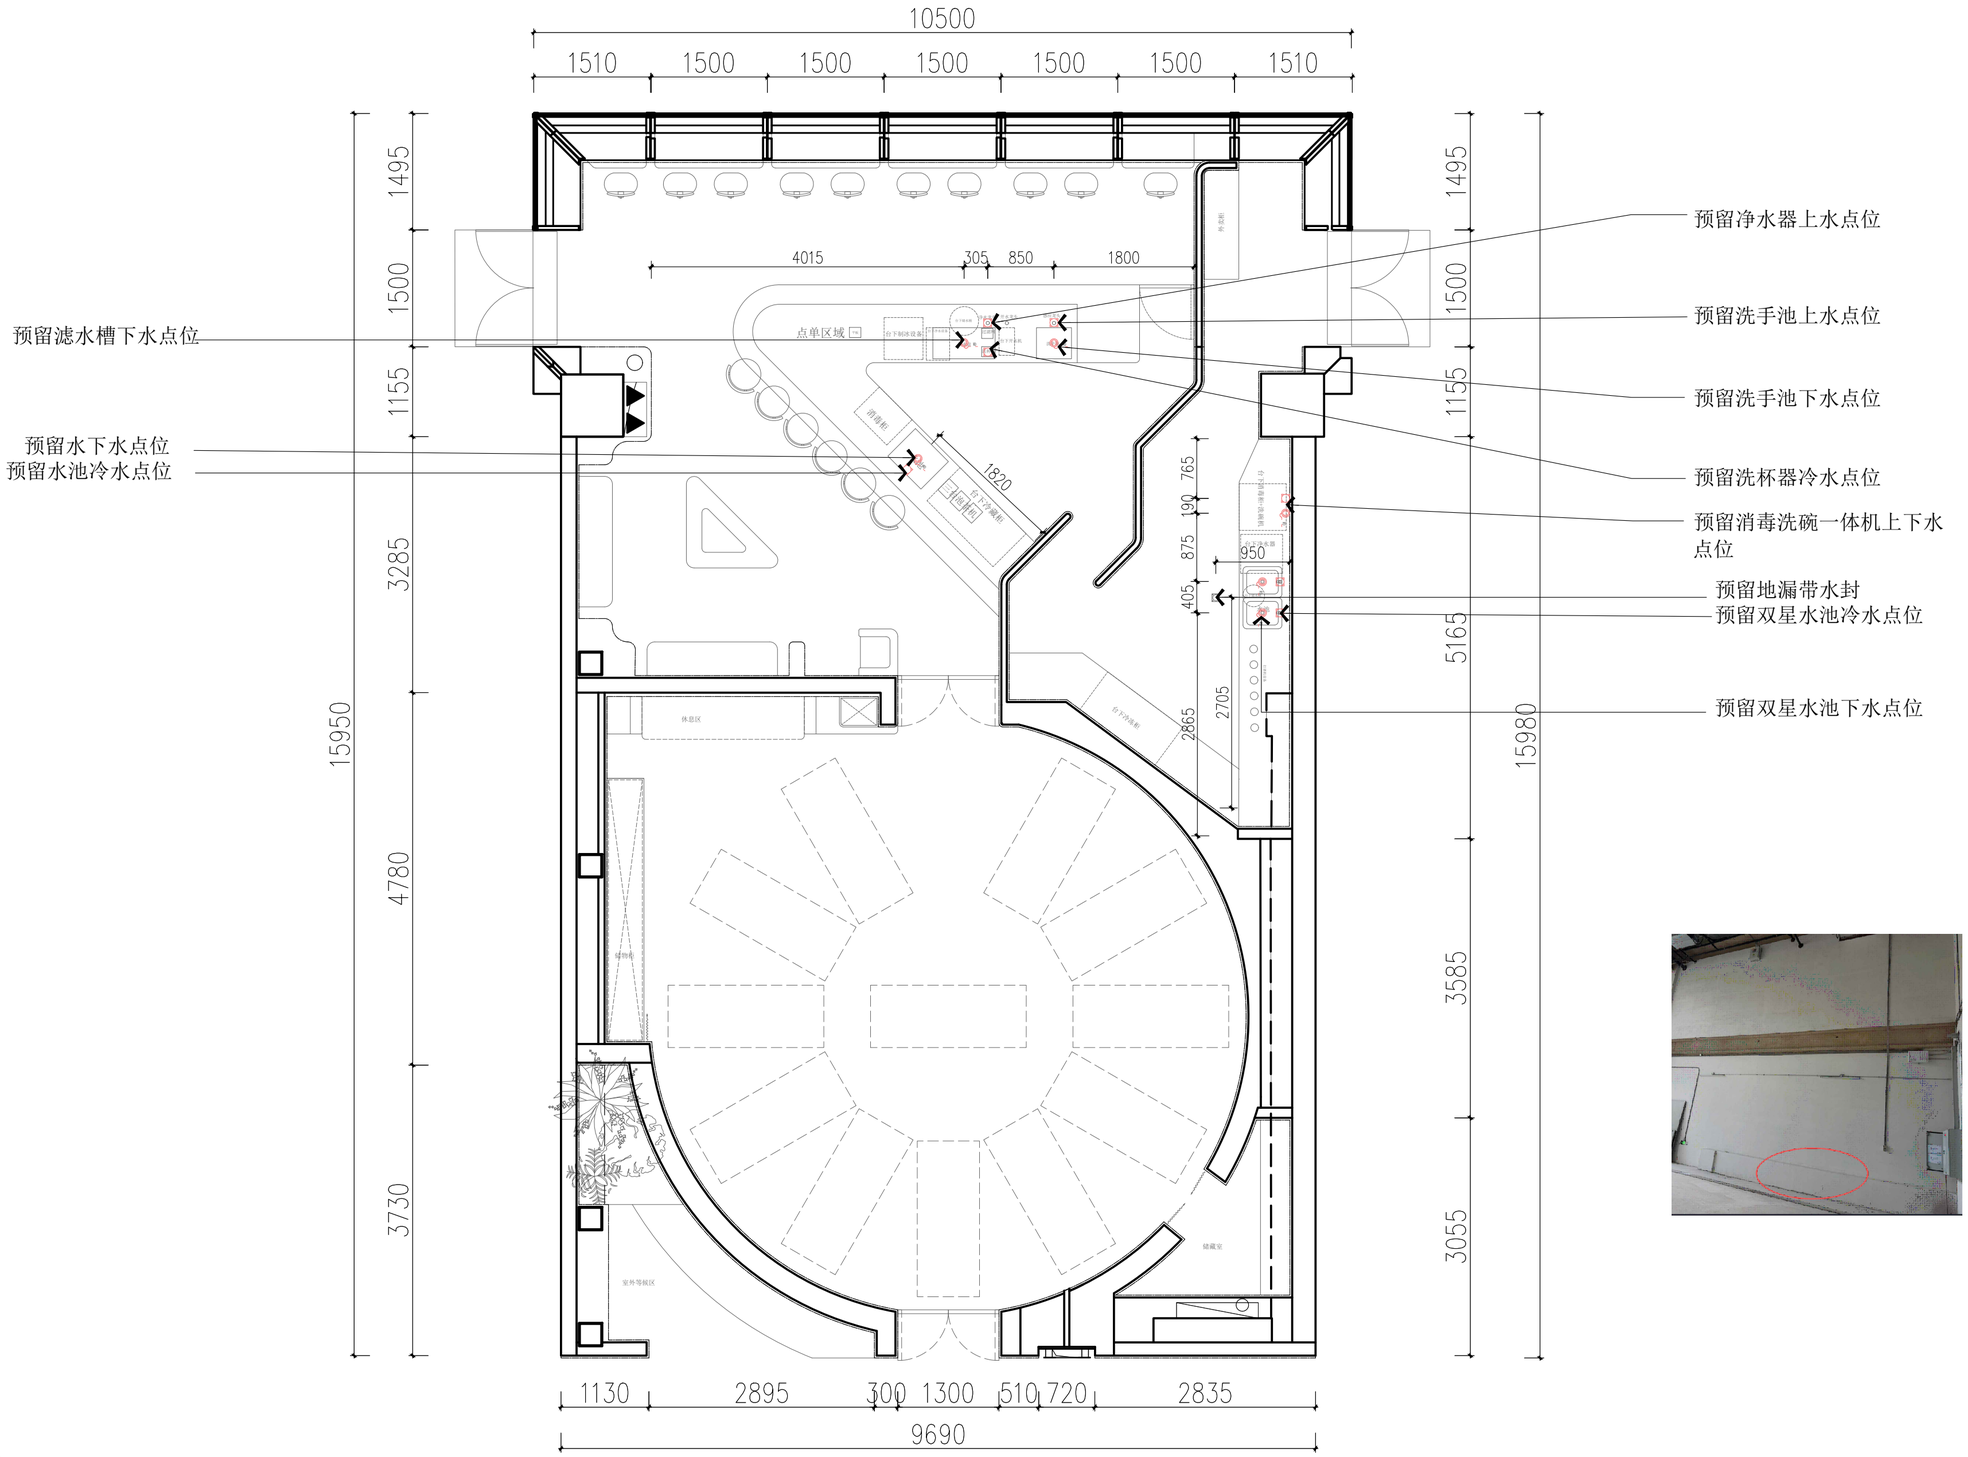

给排水图例:

symbol 符号	Name（名称）	
■	给水（热水管）	Water supply (hot water pipe)
□	给水（冷水管）	Water supply (cold water pipe)
⊗	排污管	sewage pipe
⊗	下水管	sewer pipe

注：给排水点位高度与系统详见给排水图纸。

(Please refer to the water supply and drainage drawings for details of water supply and drainage point heights and systems)

FD 1F FIXTURE/FURNISHING PLAN 给排水点位图 SCALE:1/75

会签 建筑 电气 结构 暖通 给排水 动力

ESSENZA ARMONIOSA
architecture
interiors

中国 杭州
TEL: 180 6796 1470
FAX: 180 6796 1470

图注：Exegesis

建设单位 Construction unit

设计单位 Engineering design company

顾问单位 Consultant unit

工程名称 project name

FIONA SHANGHAI

审 定		
审 核		
校 对		
项目负责人		
设 计		
制 图		

图 名

给排水点位图

图 号	PL-04
比 例	1:75
日 期	2026.08
专 业	装饰
设计阶段	施工图
版本编号	
设计编号	

出 图 盖 章


此设计图则之版权归杭州光几建筑室内设计有限公司所有 非得建筑师或设计师之书面批准 不得随意将任何部分翻印 切勿以比例量度此图 一切依图内数字所示为准承建人必须在工场核对图内所示数字之准则如发现有任何矛盾处应立即通知建筑师或设计师

ALL DESIGNS ARE THE SOLE PROPERTY OF HANGZHOU . LTD. AND I CANNOT BE USED WITHOUT WRITTEN PERMISSION.DO NOT SCALE DRAWING FIGURED DIMENSIONS ARE TO BE FOLLOWED. ALL MEASUREMENTS MUST BE CHECKED ON SITE BY THE CONTRACTOR. ANYDISCREPANCIES SHOULD BE REPORTED TO THE ARCHITECT OR DESIGNER

备注：室内地面完成面要与办公楼
内部地面齐平



5MM金属收边条选样（ 以实际选样为准）

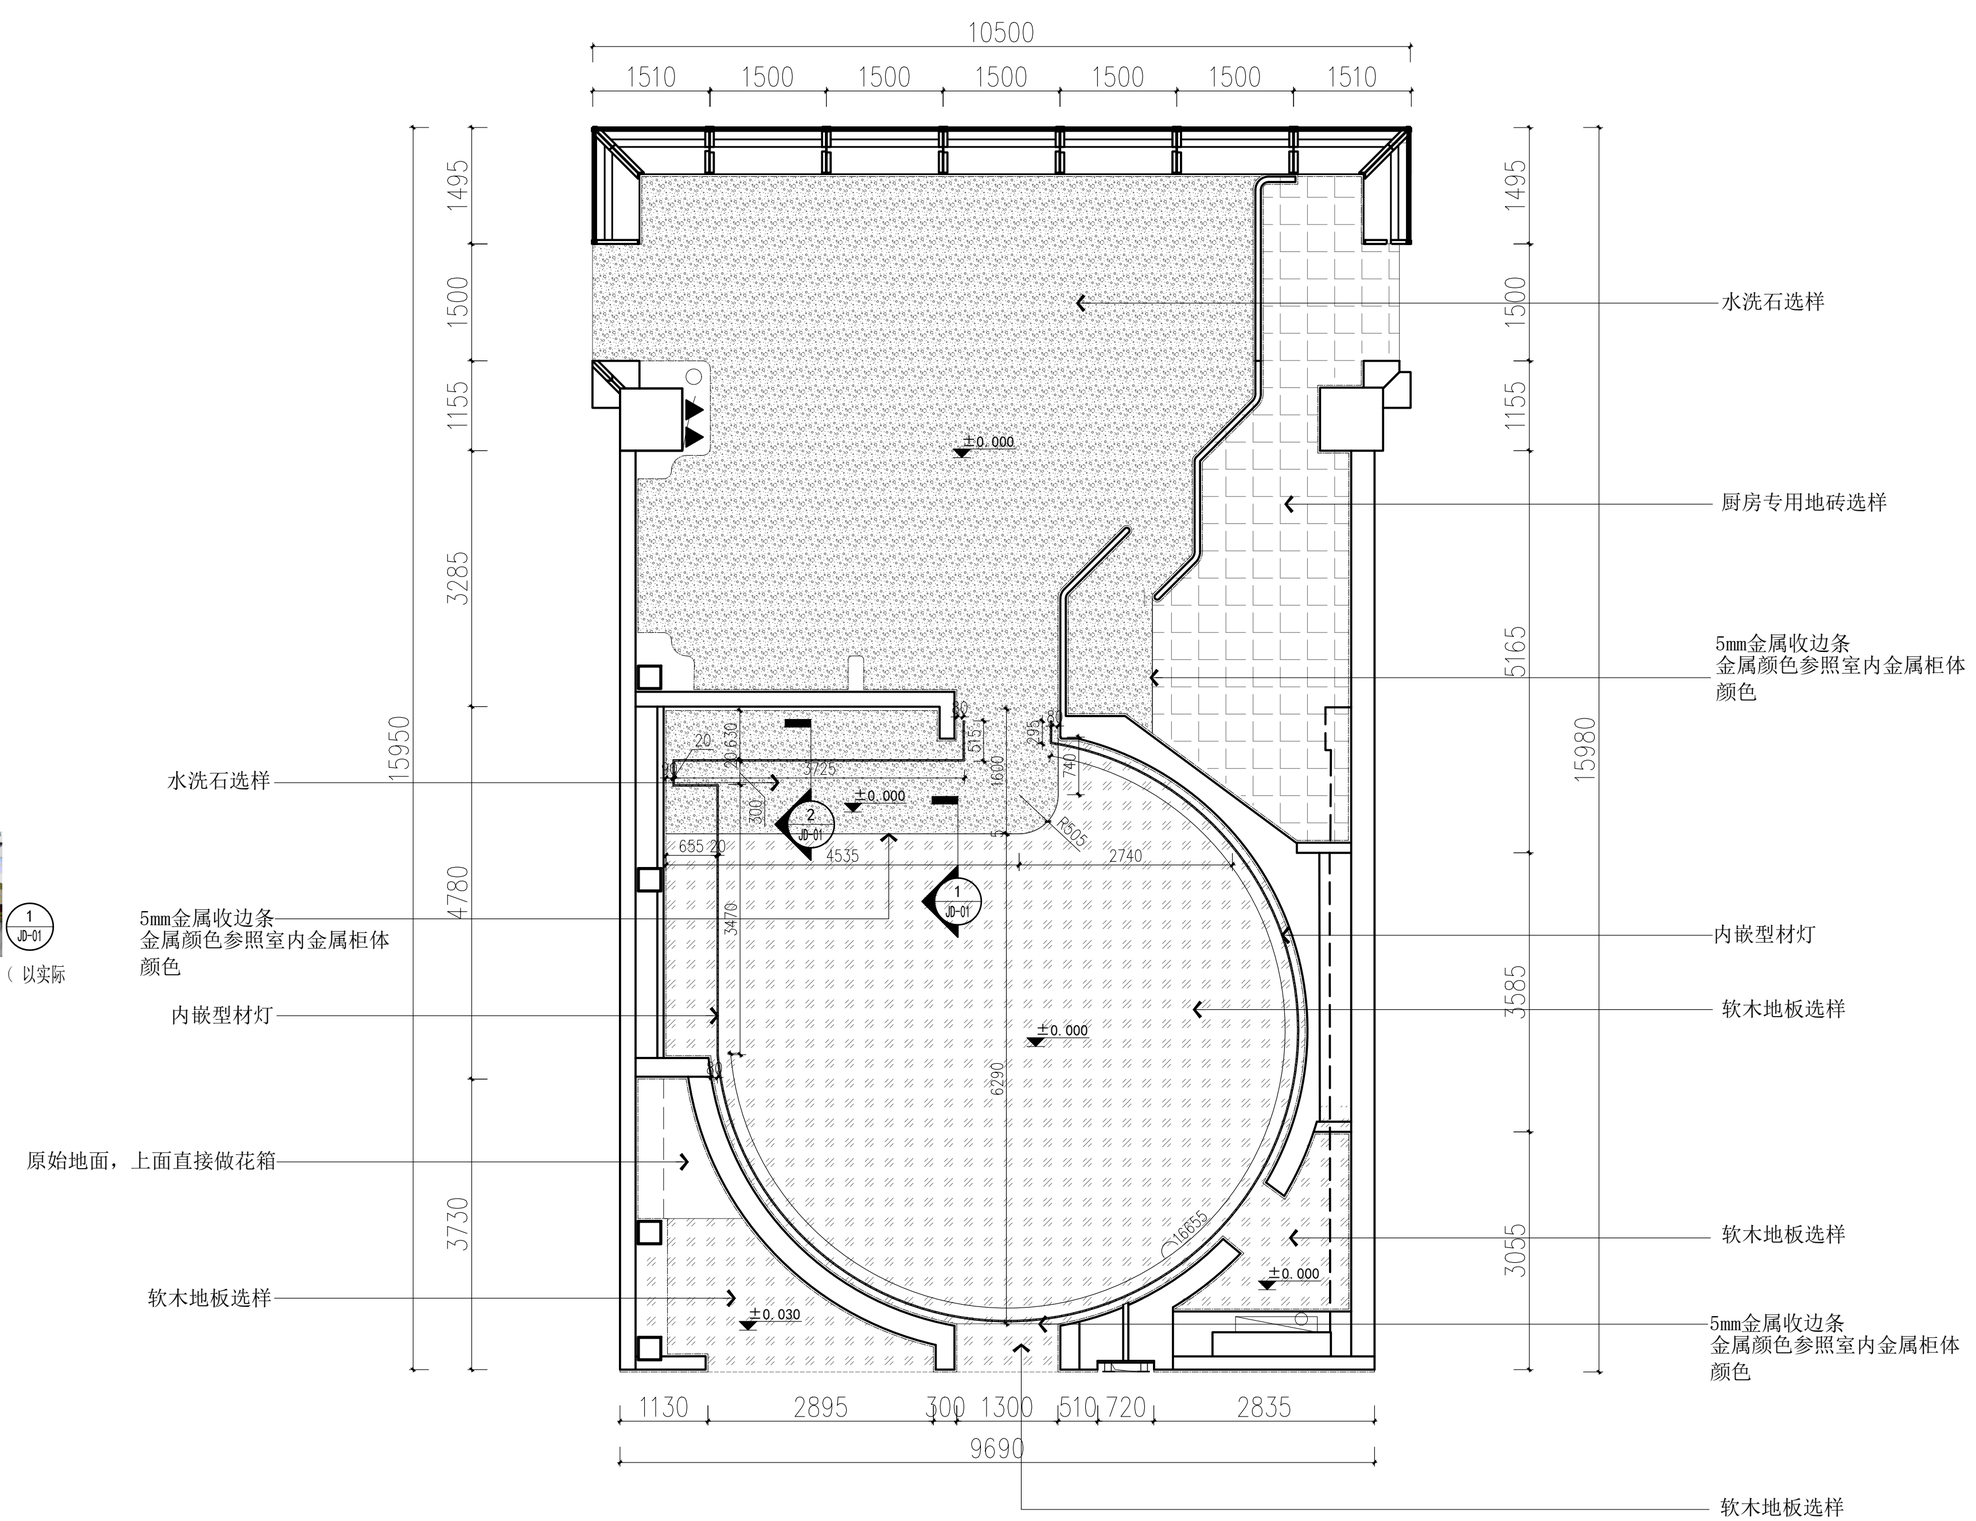

FC 1F FLOOR COVERING PLAN 地坪布置图 SCALE:1/75

会签 | 建筑 | 电气 | 结构 | 暖通 | 给排水 | 动力

ESSENZA ARMONIOSA
architecture
interiors

中国 杭州
TEL: 180 6796 1470
FAX: 180 6796 1470

图注：Exegesis

建设单位 Construction unit

设计单位 Engineering design company

顾问单位 Consultant unit

工程名称 project name

FIONA SHANGHAI

审 定		
审 核		
校 对		
项目负责人		
设 计		
制 图		

图 名

地坪布置图


图 号	PL-05
比 例	1:75
日 期	2026.08
专 业	装饰
设计阶段	施工图
版本编号	
设计编号	

出 图 盖 章

此设计图则之版权归杭州光几建筑室内设计有限公司所有 非得建筑师或设计师之书面批准 不得随意将任何部分翻印 切勿以比例量度此图 一切依图内数字所示为准承建人必须在工场核对图内所示数字之准则如发现有任何矛盾处应立即通知建筑师或设计师

ALL DESIGNS ARE THE SOLE PROPERTY OF HANGZHOU , LTD. AND CANNOT BE USED WITHOUT WRITTEN PERMISSION.DO NOT SCALE DRAWING FIGURED DIMENSIONS ARE TO BE FOLLOWED. ALL MEASUREMENTS MUST BE CHECKED ON SITE BY THE CONTRACTOR. ANYDISCREPANCIES SHOULD BE REPORTED TO THE ARCHITECT OR DESIGNER.

会签 | 建筑 | 电气 | 结构 | 暖通 | 给排水 | 动力

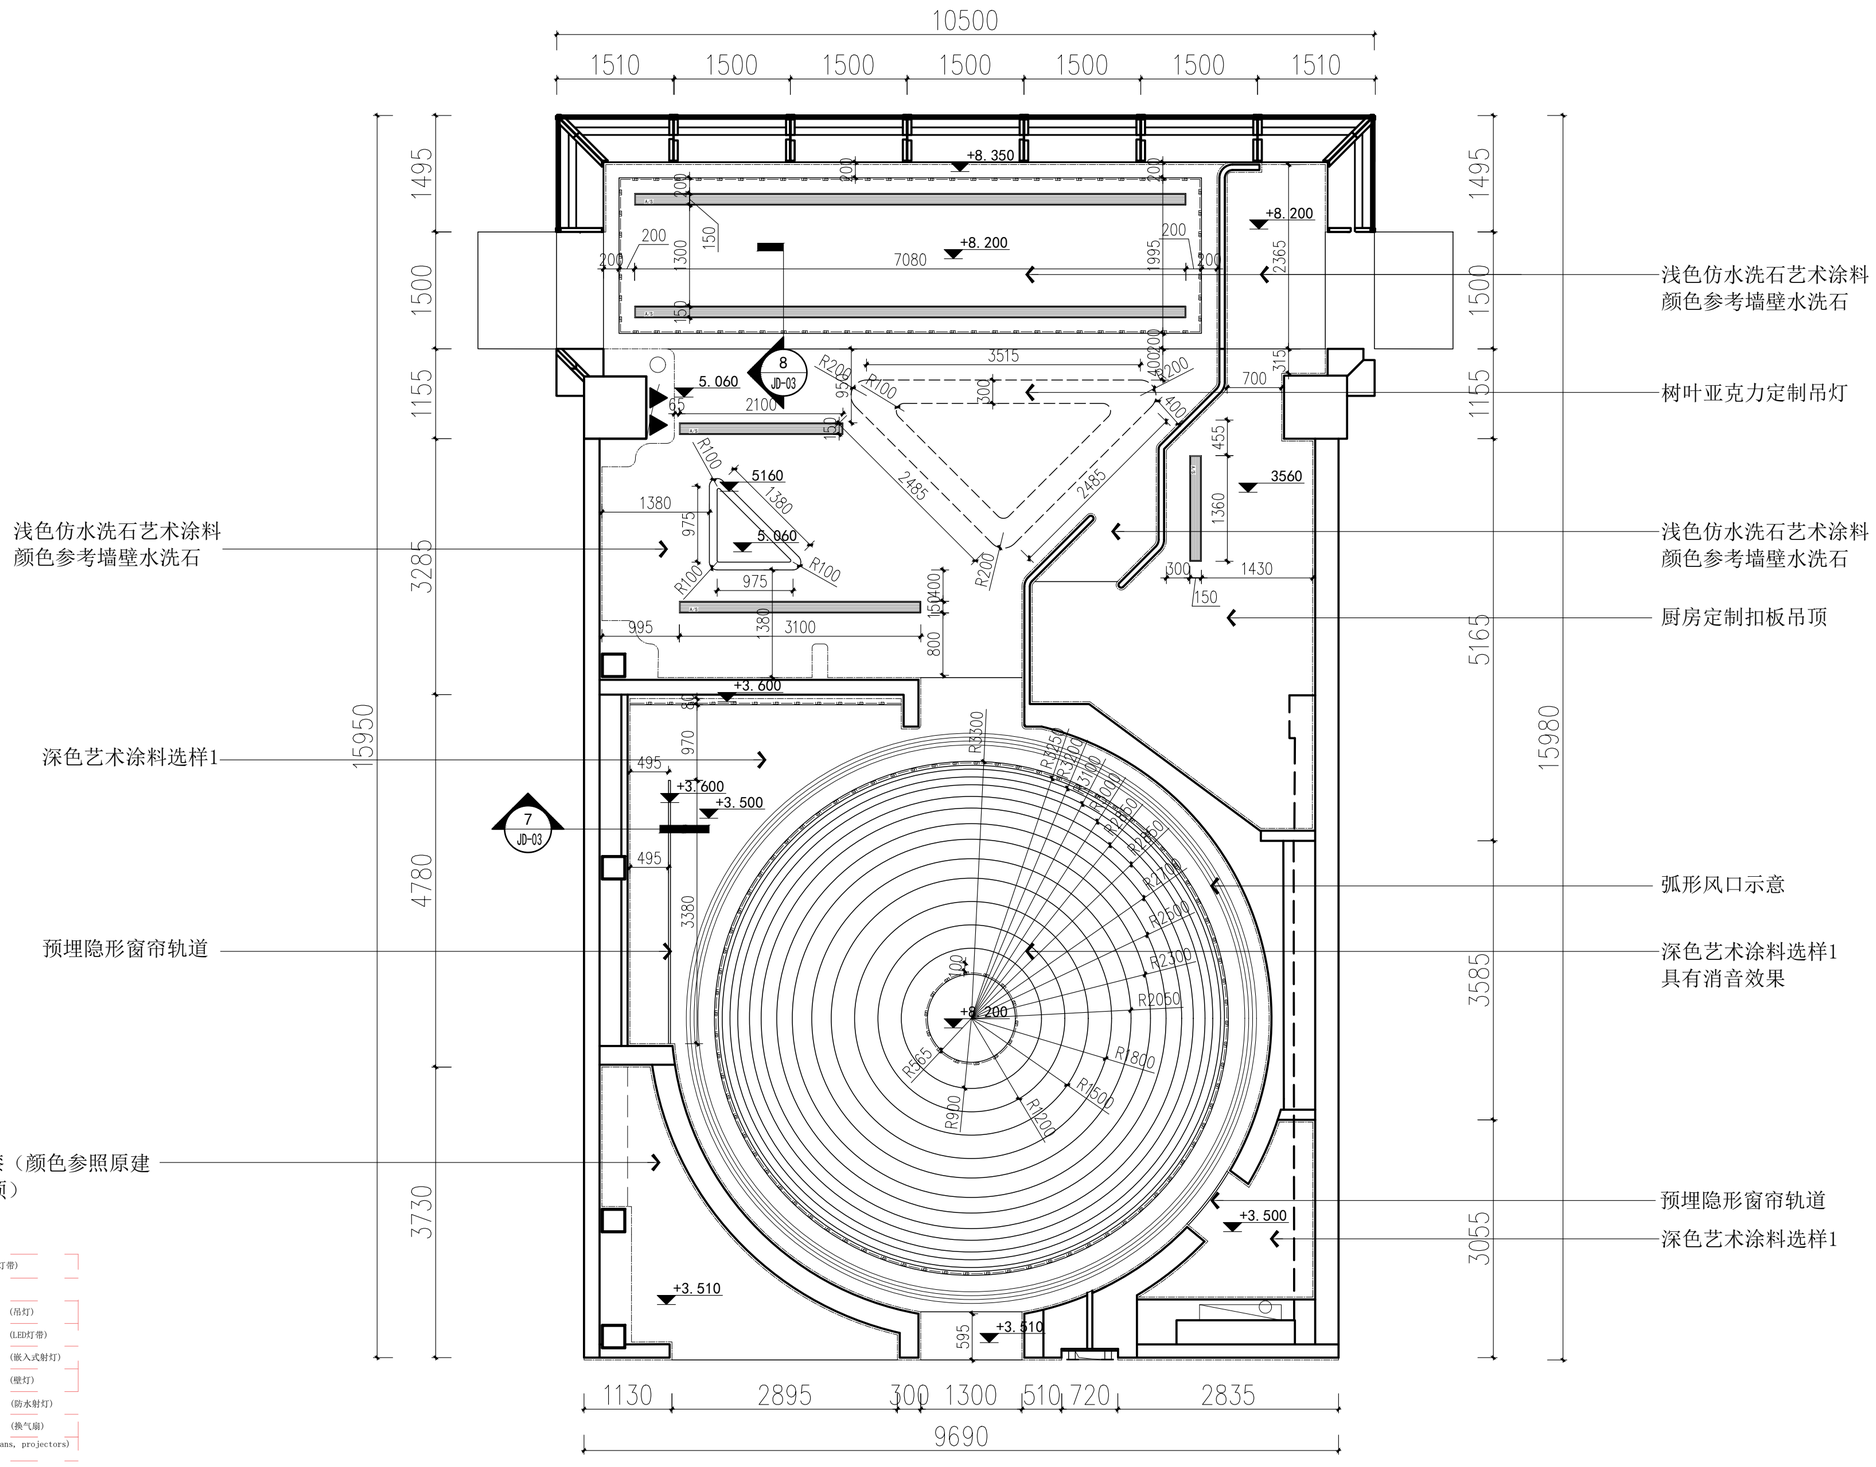

C-top lamps and light strips (C-顶面灯具、灯带)

legend (图例)	illustrate (说明)	
	chandelier	(吊灯)
	LEDlight strip	(LED灯带)
① ② ③	Recessed spotlight	(嵌入式射灯)
	Wall lamp	(壁灯)
	waterproof spotlight	(防水射灯)
A/E	ventilator	(换气扇)

C-Top equipment (air vents, ventilation fans, projectors)
C-顶面设备（风口，换气扇，投影仪）

Legend (图例)	Illustrate (说明)
A/S A/R	Side air outlet/return air outlet (侧向出风口/回风口)
A/S	Strip air outle (条形出风口)
A/R	Strip return air vent (条形回风口)

RC 1F REFLECTED CEILING PLAN 天花布置图 SCALE:1/75

ESSENZA ARMONIOSA
architecture
interiors

中国 杭州
TEL: 180 6796 1470
FAX: 180 6796 1470

图注：Exegesis

建设单位 Construction unit

设计单位 Engineering design company

顾问单位 Consultant unit

工程名称 project name

FIONA SHANGHAI

审 定		
审 核		
校 对		
项目负责人		
设 计		
制 图		

图 名

天花布置图

图 号	PL-06
比 例	1:75
日 期	2026.08
专 业	装饰
设计阶段	施工图
版本编号	
设计编号	

出 图 盖 章

此设计图则之版权归杭州光几建筑室内设计有限公司所有 非得建筑师或设计师之书面批准 不得随意将任何部分翻印 切勿以比例量度此图 一切依图内数字所示为准承建人必须在工场核对图内所示数字之准则如发现有任何矛盾处应立即通知建筑师或设计师

ALL DESIGNS ARE THE SOLE PROPERTY OF HANGZHOU , LTD. AND CANNOT BE USED WITHOUT WRITTEN PERMISSION.DO NOT SCALE DRAWING FIGURED DIMENSIONS ARE TO BE FOLLOWED ALL MEASUREMENTS MUST BE CHECKED ON SITE BY THE CONTRACTOR ANYDISCREPANCIES SHOULD BE REPORTED TO THE ARCHITECT OR DESIGNER

A3-420*297

会签 | 建筑 | 电气 | 结构 | 暖通 | 给排水 | 动力

预留1个五孔插座 H:135

吊顶预留电动遮阳帘和灯带电源

预留1个五孔插座 H:200

吧台内部预留净水器电源

吧台内部预留制冰设备电源

吧台预留2-3个五孔插座 H:870

墙面预留音响电源H:2050

吧台内部预留消毒柜设备电源

墙面预留LCD屏幕电源和网络

墙面预留层板灯带电源

预留踢脚灯带电源

吊顶预留灯带电源

墙面预留柜体灯带电源

墙面预留2个五孔插座 H：1200

预留墙面吊顶灯带电源

墙面预留2个五孔插座 +灯光+空调控制面板 H：1250

预留柜体电动伸缩衣架电源



电动伸缩衣架

预留地面内嵌灯带电源


预留花池灯光电源

预留墙面凹槽灯带电源 H:1000

预留踢脚线灯带电源

预留店招电源H:2200

预留卡座后方和下方灯带电源

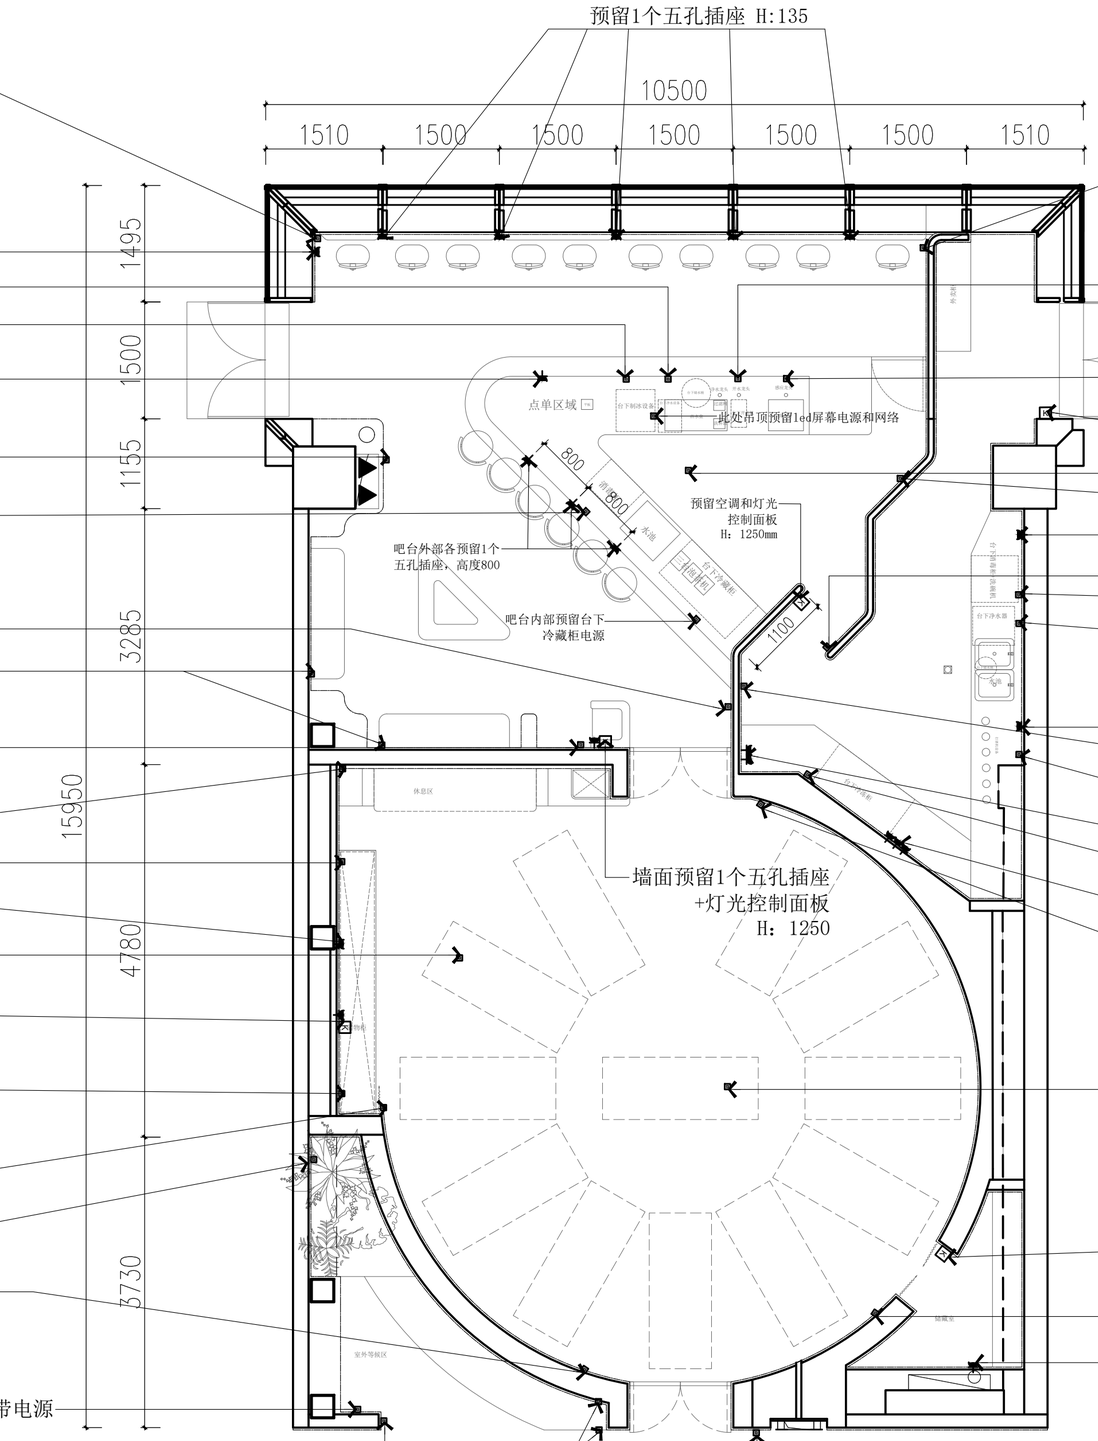

预留踢脚灯带电源

吧台内部预留开水器电源

预留灯光控制面板H：1250mm 吊顶预留吊灯电源

墙面预留音响电源H:2050

预留3个五孔插座 H：1000

墙面预留灯带电源

内部预留洗碗消毒一体柜设备电源

内部预留净水器电源

各预留1个五孔插座 H：1000

墙面预留LED屏连接电脑的电源和网络以及HDMI接口

吧台内部预留普康茶设备电源

预留俩个五孔插座 H：820

内部预留冰柜设备电源

各预留3个五孔插座 H：1000

预留墙面凹槽灯带电源 H:1000

预留吊顶灯带电源

预留灯光控制面板 H：1250mm

预留墙面凹槽灯带电源 H:1000

预留2个五孔插座 H:350

预留墙面上下灯带电源

1495
1500
1155
5165
15980
3585
3055

M-electromechanical point (M-机电点位)

M	Five-hole socket (with switch)	(五孔插座(带开关))
	Network Interface	(网络接口)
		网络接口
		电话接口
	Ground socket	(地面插座)
	Ceiling socket	(吊顶插座)
	Two-pole/three-pole single-phase socket	(二极/三极单相插座)
	Two-pole/three-pole socket with switch	(二极/三极带开关插座)
	Power supply	(电源)

RC 1F REFLECTED CEILING PLAN 机电点位图 SCALE:1/75

ESSENZA ARMONIOSA
architecture interiors

中国 杭州
TEL： 180 6796 1470
FAX： 180 6796 1470

图注：Exegesis

建设单位 Construction unit

设计单位 Engineering design company

顾问单位 Consultant unit

工程名称 project name

FIONA SHANGHAI

审 定		
审 核		
校 对		
项目负责人		
设 计		
制 图		

图 名 机电点位图

图 号	PL-07
比 例	1:75
日 期	2026.08
专 业	装饰
设计阶段	施工图
版本编号	
设计编号	

出 图 盖 章

此设计图则之版权归杭州光几建筑室内设计有限公司所有 非得建筑师或设计师之书面批准 不得随意将任何部分翻印 切勿以比例量度此图 一切依图内数字所示为准承建人必须在工场核对图内所示数字之准则如发现有任何矛盾处应立即通知建筑师或设计师


ALL DESIGNS ARE THE SOLE PROPERTY OF HANGZHOU , LTD. AND CANNOT BE USED WITHOUT WRITTEN PERMISSION.DO NOT SCALE DRAWING FIGURED DIMENSIONS ARE TO BE FOLLOWED. ALL MEASUREMENTS MUST BE CHECKED ON SITE BY THE CONTRACTOR. ANYDISCREPANCIES SHOULD BE REPORTED TO THE ARCHITECT OR DESIGNER.

A3-420*297

会签	
建筑	电气
结构	暖通
给排水	动力

备注：监控/音响具体点位，现场需根据甲方需求进行二次确认。

瑜伽教授音响需要接线到调音设备上

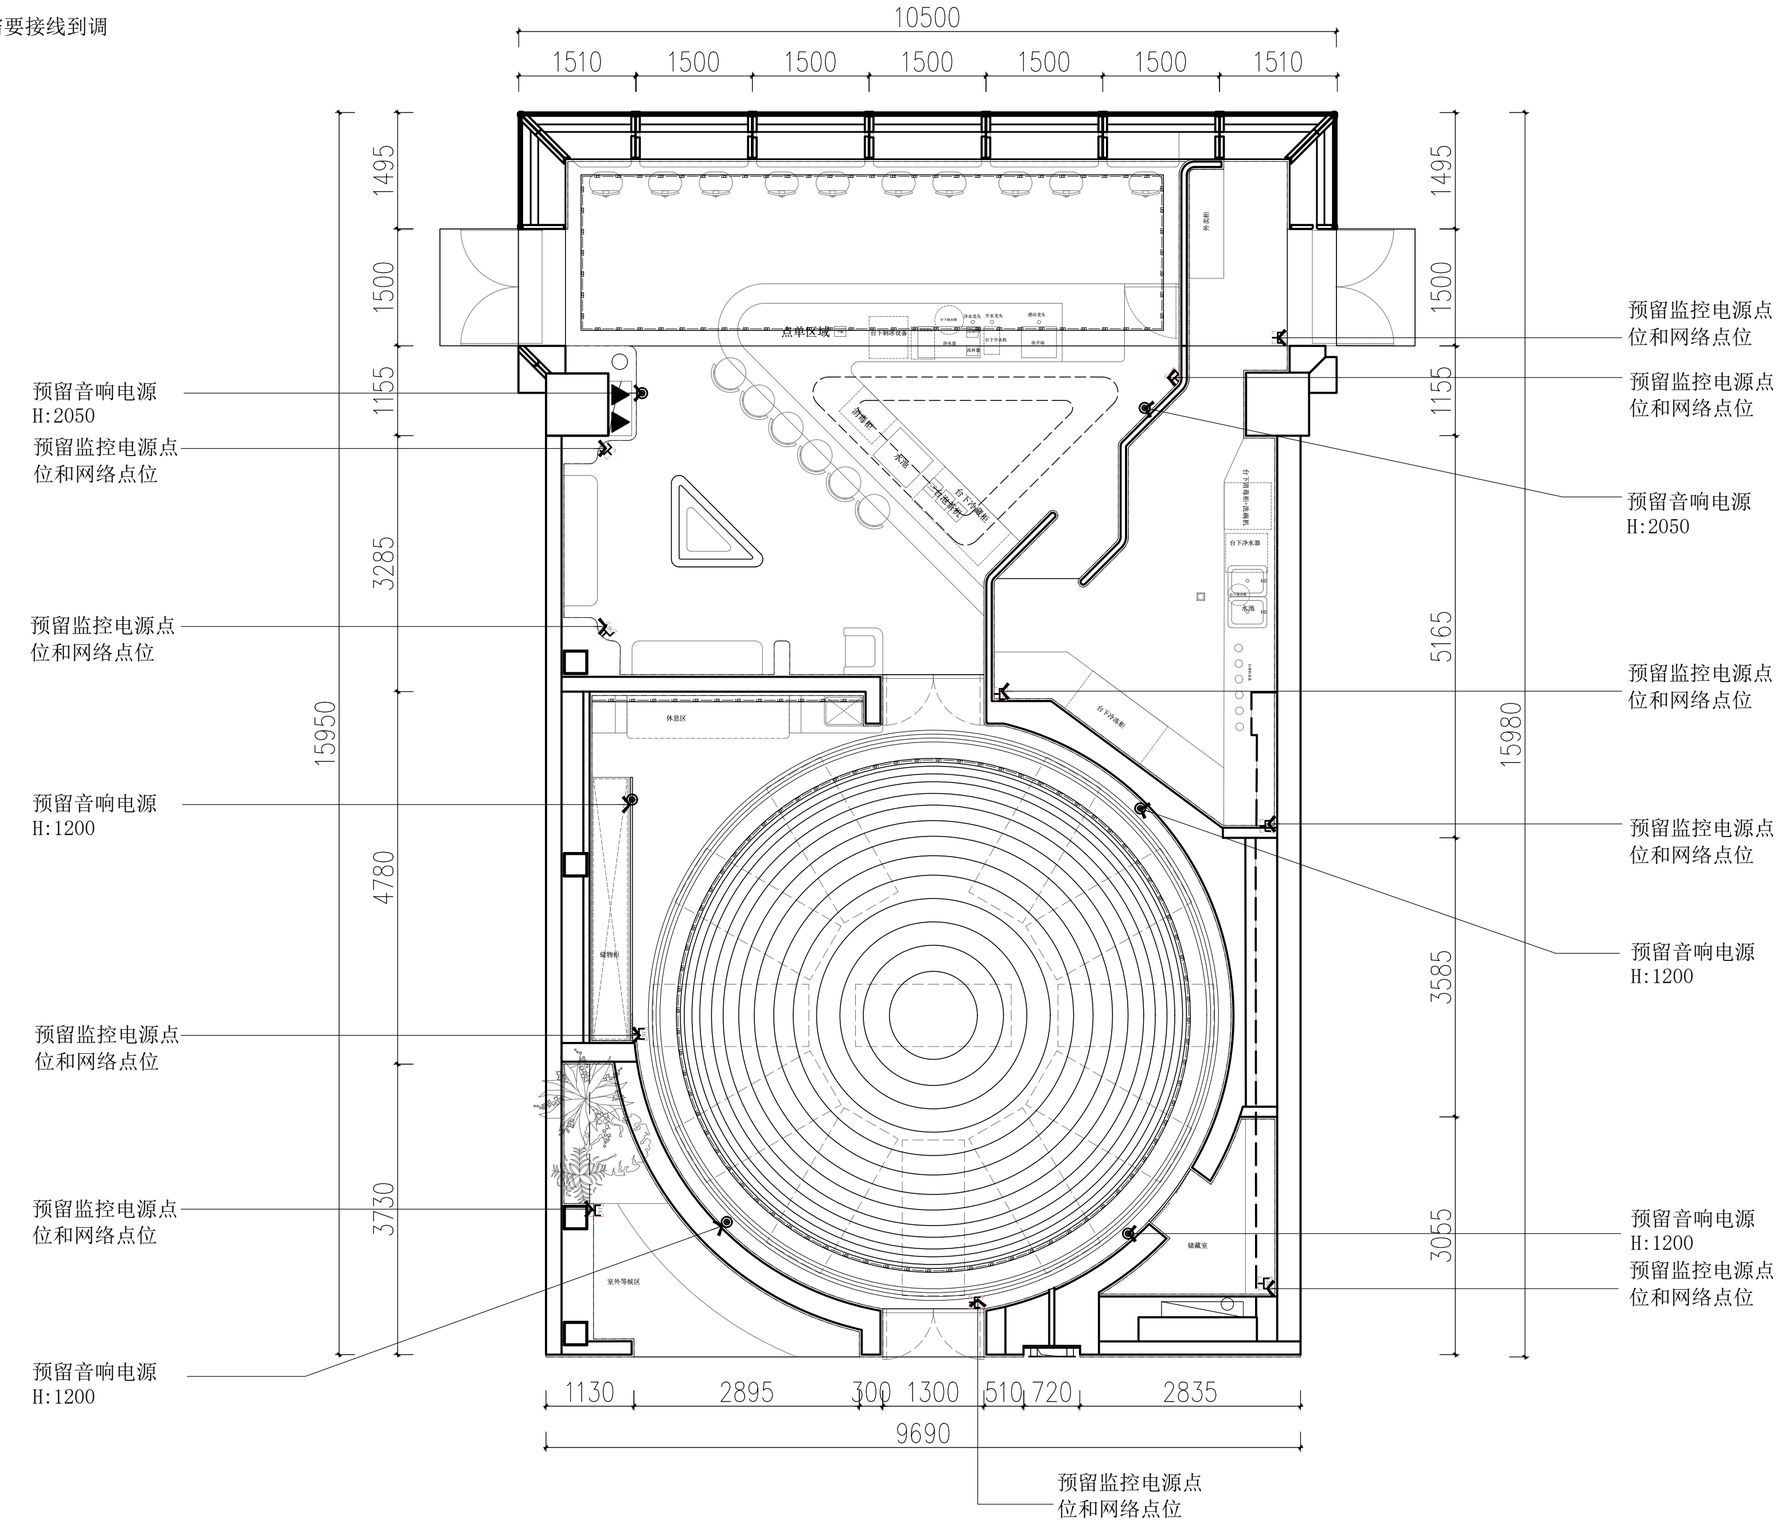

监控

监控

音响

RC 1F REFLECTED CEILING PLAN 监控点位图 SCALE:1/75

ESSENZA ARMONIOSA
architecture
interiors

中国 杭州
TEL: 180 6796 1470
FAX: 180 6796 1470

图注：Exegesis

建设单位 Construction unit

设计单位 Engineering design company

顾问单位 Consultant unit

工程名称 project name

FIONA SHANGHAI

审 定		
审 核		
校 对		
项目负责人		
设 计		
制 图		

图 名


监控点位+音响点位图

图 号	PL-08
比 例	1:75
日 期	2026.08
专 业	装饰
设计阶段	施工图
版本编号	
设计编号	

出 图 盖 章

此设计图则之版权归杭州光几建筑室内设计有限公司所有 非得建筑师或设计师之书面批准 不得随意将任何部分翻印 切勿以比例量度此图 一切依图内数字所示为准承建人必须在工场核对图内所示数字之准则如发现有任何矛盾处应立即通知建筑师或设计师

ALL DESIGNS ARE THE SOLE PROPERTY OF HANGZHOU , LTD. AND CANNOT BE USED WITHOUT WRITTEN PERMISSION.DO NOT SCALE DRAWING.FIGURED DIMENSIONS ARE TO BE FOLLOWED.ALL MEASUREMENTS MUST BE CHECKED ON SITE BY THE CONTRACTOR.ANYDISCREPANCIES SHOULD BE REPORTED TO THE ARCHITECT OR DESIGNER.

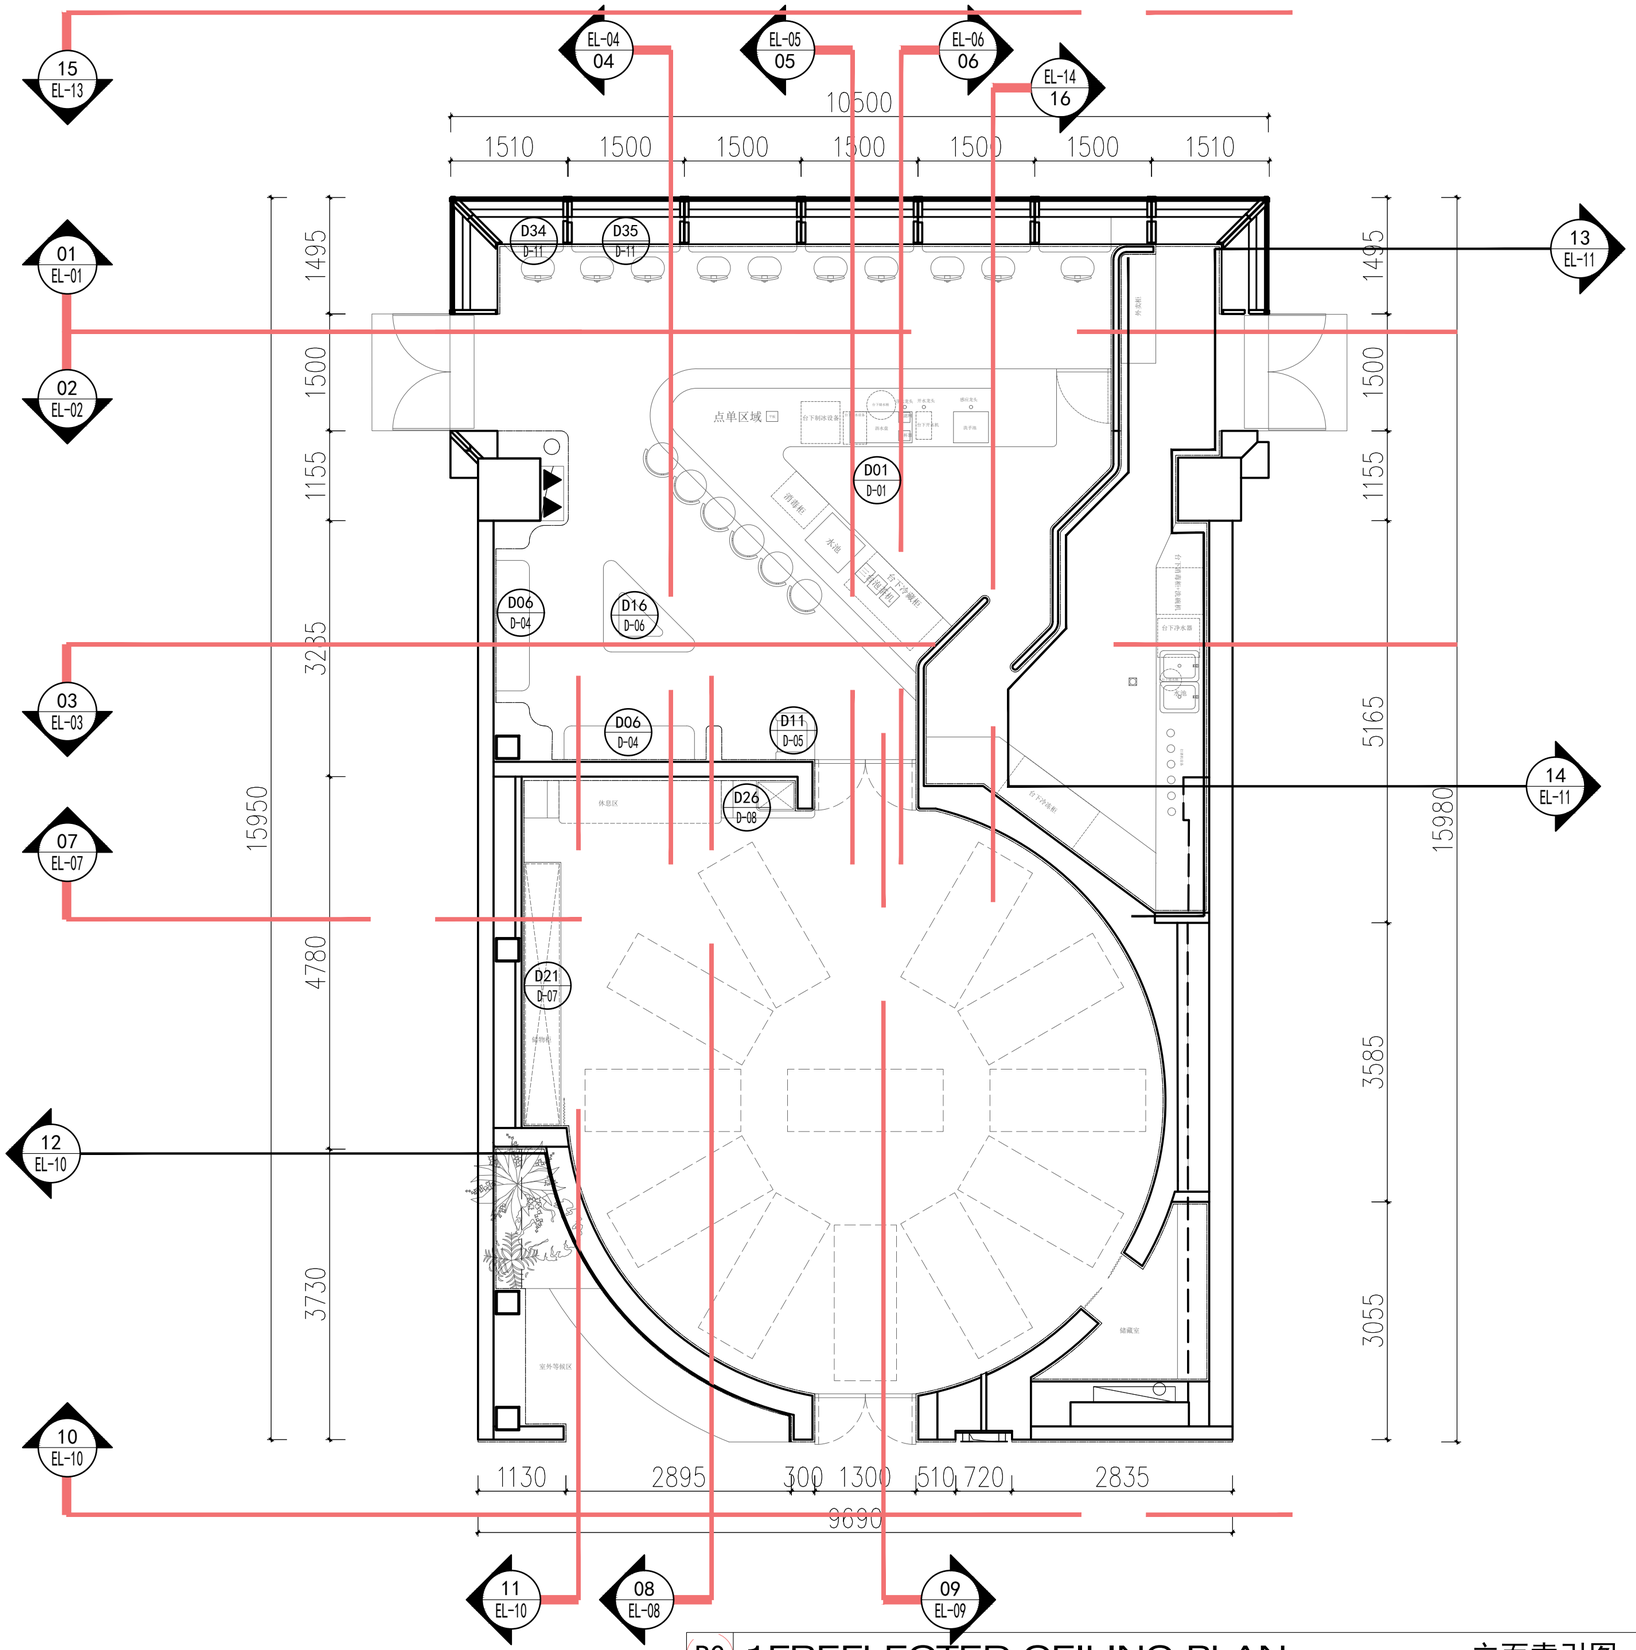

会签 | 建筑 | 电气 | 结构 | 暖通 | 给排水 | 动力

ESSENZA ARMONIOSA
architecture
interiors

中国 杭州
TEL: 180 6796 1470
FAX: 180 6796 1470

图注: Exegesis

建设单位 Construction unit

设计单位 Engineering design company

顾问单位 Consultant unit

工程名称 project name

FIONA SHANGHAI

审 定		
审 核		
校 对		
项目负责人		
设 计		
制 图		

图 名

立面索引图

图 号	PL-09
比 例	1:75
日 期	2026.08
专 业	装饰
设计阶段	施工图
版本编号	
设计编号	

出 图 盖 章


此设计图则之版权归杭州光几建筑室内设计有限公司所有 非得建筑师或设计师之书面批准 不得随意将任何部分翻印 切勿以比例量度此图 一切依图内数字所示为准承建人必须在工场核对图内所示数字之准则如发现有任何矛盾处应立即通知建筑师或设计师

ALL DESIGNS ARE THE SOLE PROPERTY OF HANGZHOU . LTD. AND I CANNOT BE USED WITHOUT WRITTEN PERMISSION.DO NOT SCALE DRAWING. FIGURED DIMENSIONS ARE TO BE FOLLOWED. ALL MEASUREMENTS MUST BE CHECKED ON SITE BY THE CONTRACTOR. ANYDISCREPANCIES SHOULD BE REPORTED TO THE ARCHITECT OR DESIGNER.

RC 1 FREFLECTED CEILING PLAN 立面索引图 SCALE:1/75

A3-420*297

备注：所有立面尺寸仅供参考，实际要以现场实际尺寸为准，施工方需审核图纸，如图纸与现场不符，需要及时向设计方反馈问题。

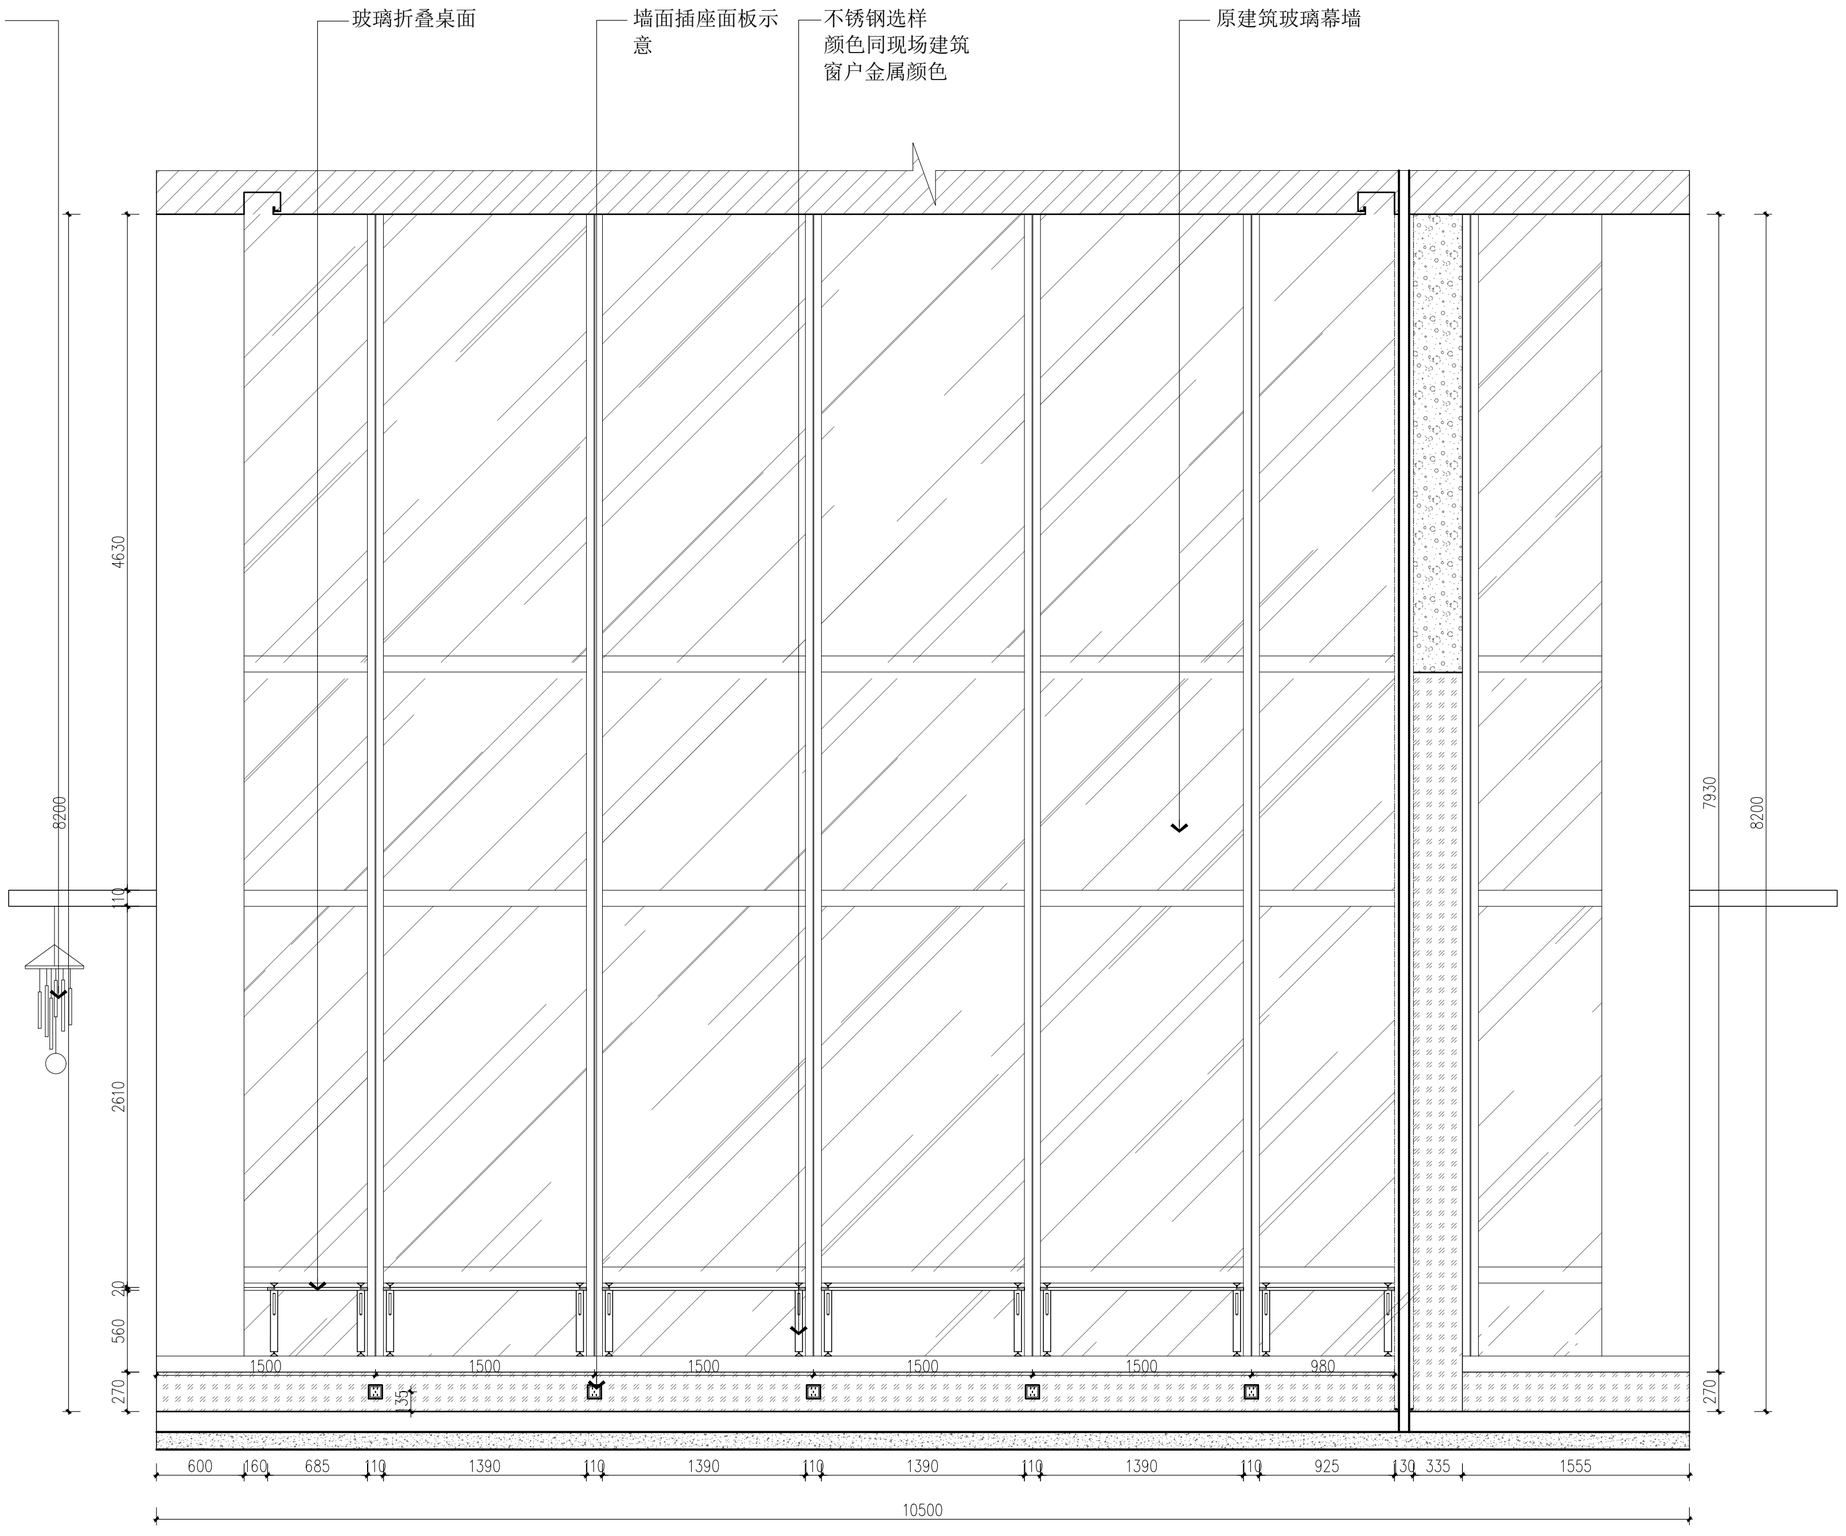

1 ELEVATION 立面图 SCALE:1/40

会签 建筑 电气 结构 暖通 给排水 动力

ESSENZA ARMONIOSA
architecture interiors

中国 杭州
TEL: 180 6796 1470
FAX: 180 6796 1470

图注：Exegesis

建设单位 Construction unit

设计单位 Engineering design company

顾问单位 Consultant unit

工程名称 project name

FIONA SHANGHAI

审 定		
审 核		
校 对		
项目负责人		
设 计		
制 图		

图 名

立面图


图 号	EL-01
比 例	1:40
日 期	2026.08
专 业	装饰
设计阶段	施工图
版本编号	
设计编号	

出 图 盖 章

此设计图则之版权归杭州光几建筑室内设计有限公司所有 非得建筑师或设计师之书面批准 不得随意将任何部分翻印 切勿以比例量度此图 一切依图内数字所示为准承建人必须在工场核对图内所示数字之准则如发现有任何矛盾处应立即通知建筑师或设计师

ALL DESIGNS ARE THE SOLE PROPERTY OF HANGZHOU , LTD. AND CANNOT BE USED WITHOUT WRITTEN PERMISSION.DO NOT SCALE DRAWING FIGURED DIMENSIONS ARE TO BE FOLLOWED ALL MEASUREMENTS MUST BE CHECKED ON SITE BY THE CONTRACTOR ANYDISCREPANCIES SHOULD BE REPORTED TO THE ARCHITECT OR DESIGNER

A3-420*297

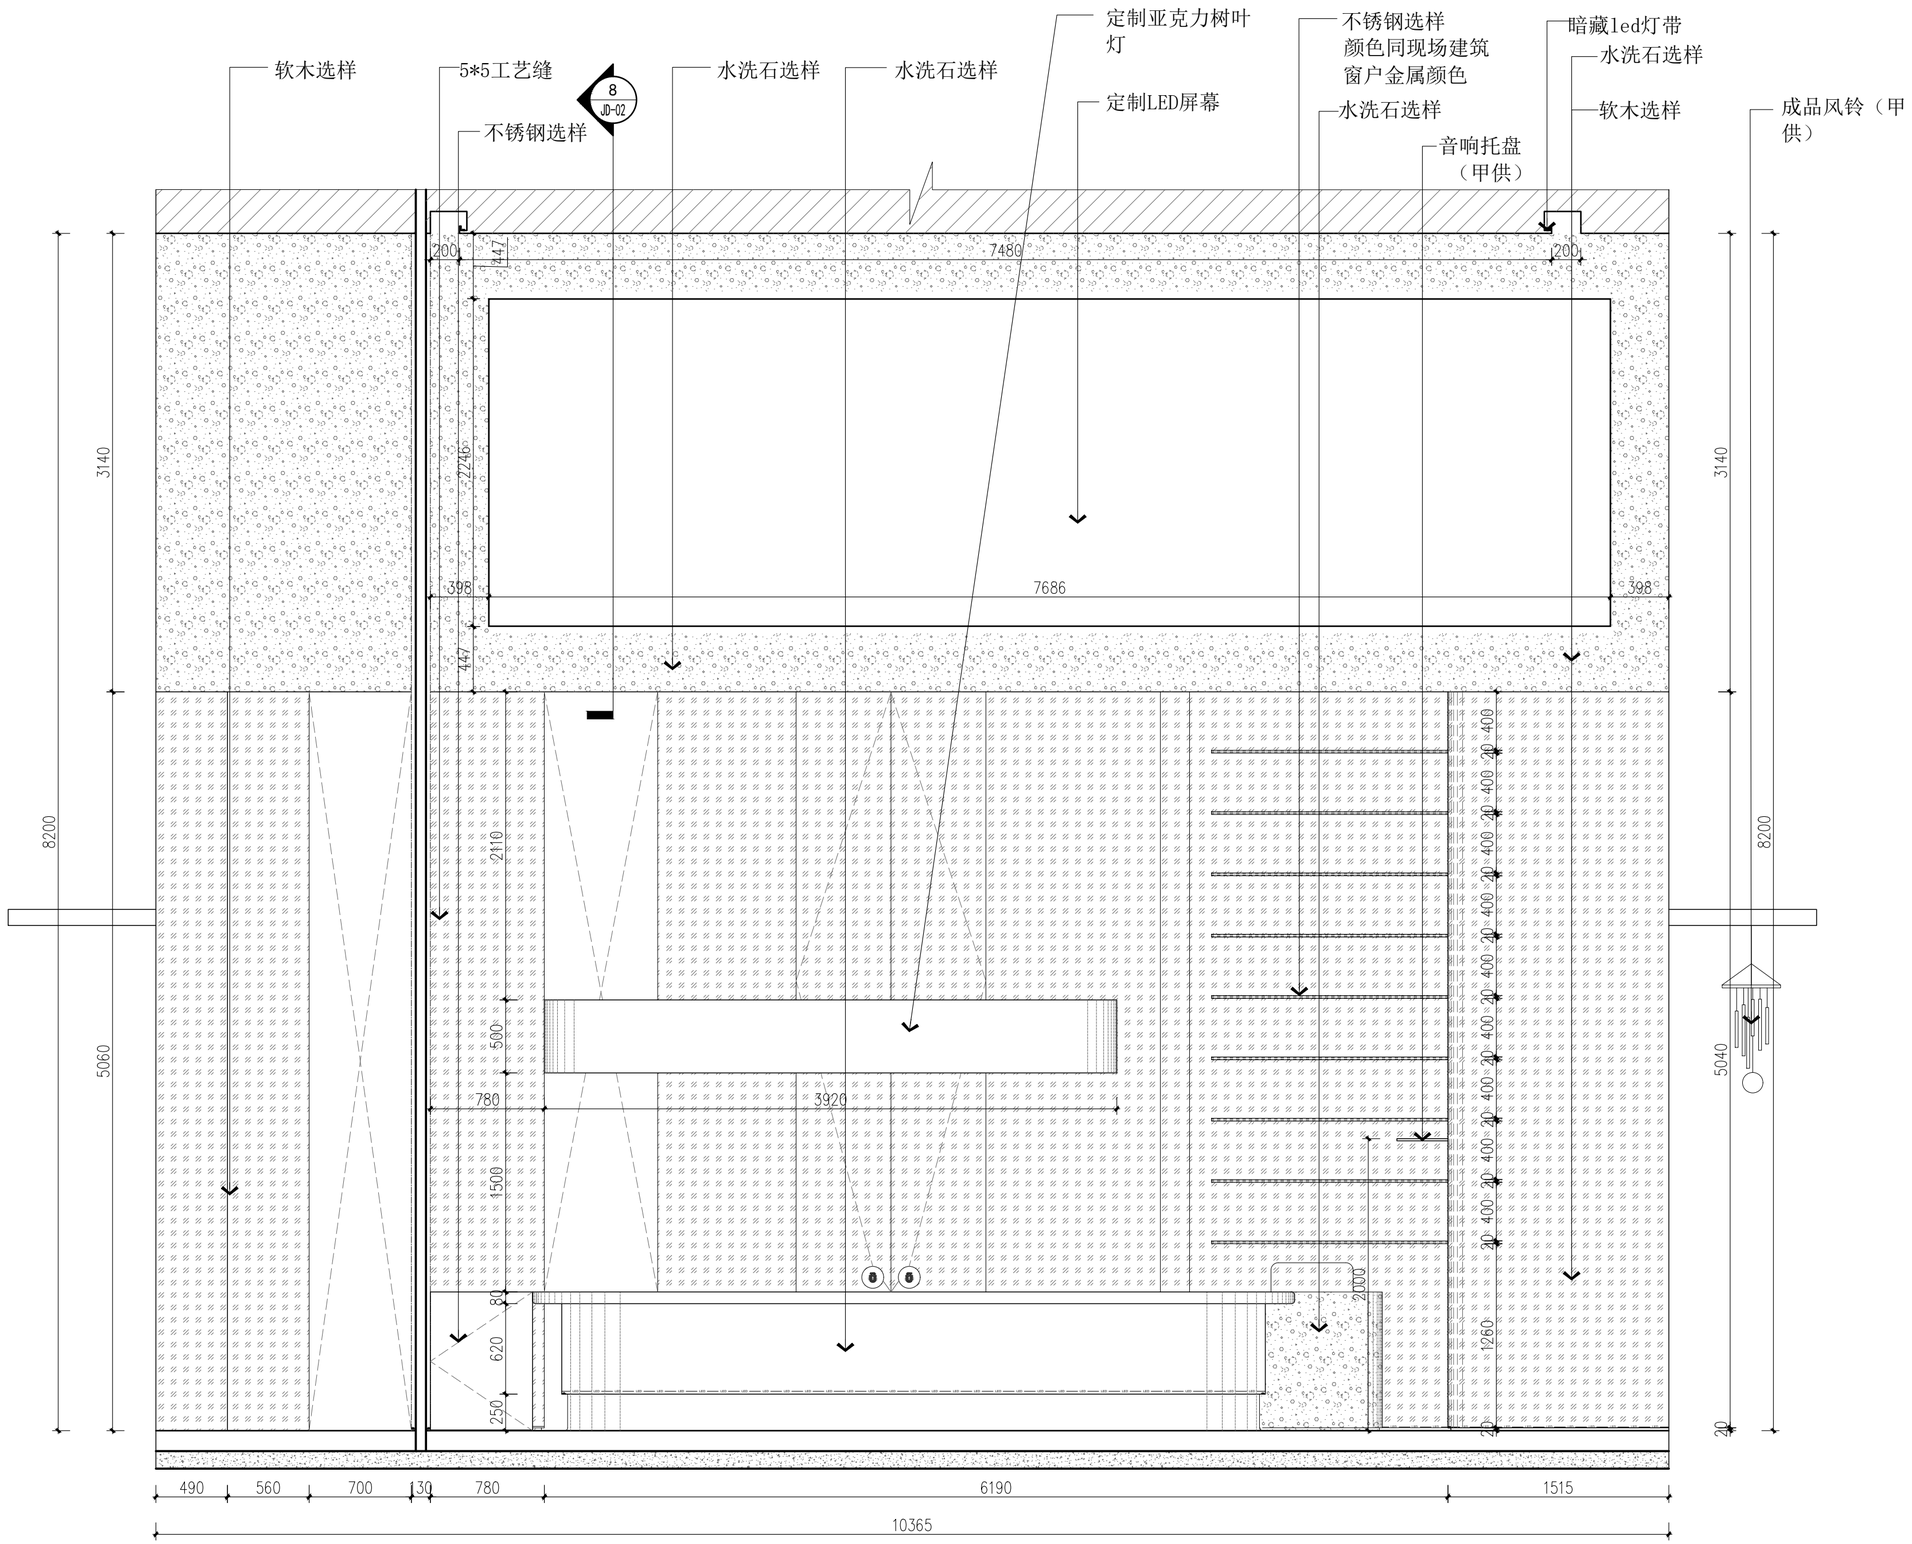

2 ELEVATION 立面图 SCALE:1/40

会签 建筑 电气 结构 暖通 给排水 动力

ESSENZA ARMONIOSA
architecture interiors

中国 杭州
TEL: 180 6796 1470
FAX: 180 6796 1470

图注: Exegesis

建设单位 Construction unit

设计单位 Engineering design company

顾问单位 Consultant unit

工程名称 project name

FIONA SHANGHAI

审 定		
审 核		
校 对		
项目负责人		
设 计		
制 图		

图 名 立面图

图 号	EL-02
比 例	1:40
日 期	2026.08
专 业	装饰
设计阶段	施工图
版本编号	
设计编号	


出 图 盖 章

此设计图则之版权归杭州光几建筑室内设计有限公司所有 非得建筑师或设计师之书面批准 不得随意将任何部分翻印 切勿以比例量度此图 一切依图内数字所示为准承建人必须在工场核对图内所示数字之准则如发现有任何矛盾处应立即通知建筑师或设计师

ALL DESIGNS ARE THE SOLE PROPERTY OF HANGZHOU + LTD. AND CANNOT BE USED WITHOUT WRITTEN PERMISSION.DO NOT SCALE DRAWING. FIGURED DIMENSIONS ARE TO BE FOLLOWED. ALL MEASUREMENTS MUST BE CHECKED ON SITE BY THE CONTRACTOR. ANYDISCREPANCIES SHOULD BE REPORTED TO THE ARCHITECT OR DESIGNER.

A3-420*297

会签 | 建筑 | 电气 | 结构 | 暖通 | 给排水 | 动力

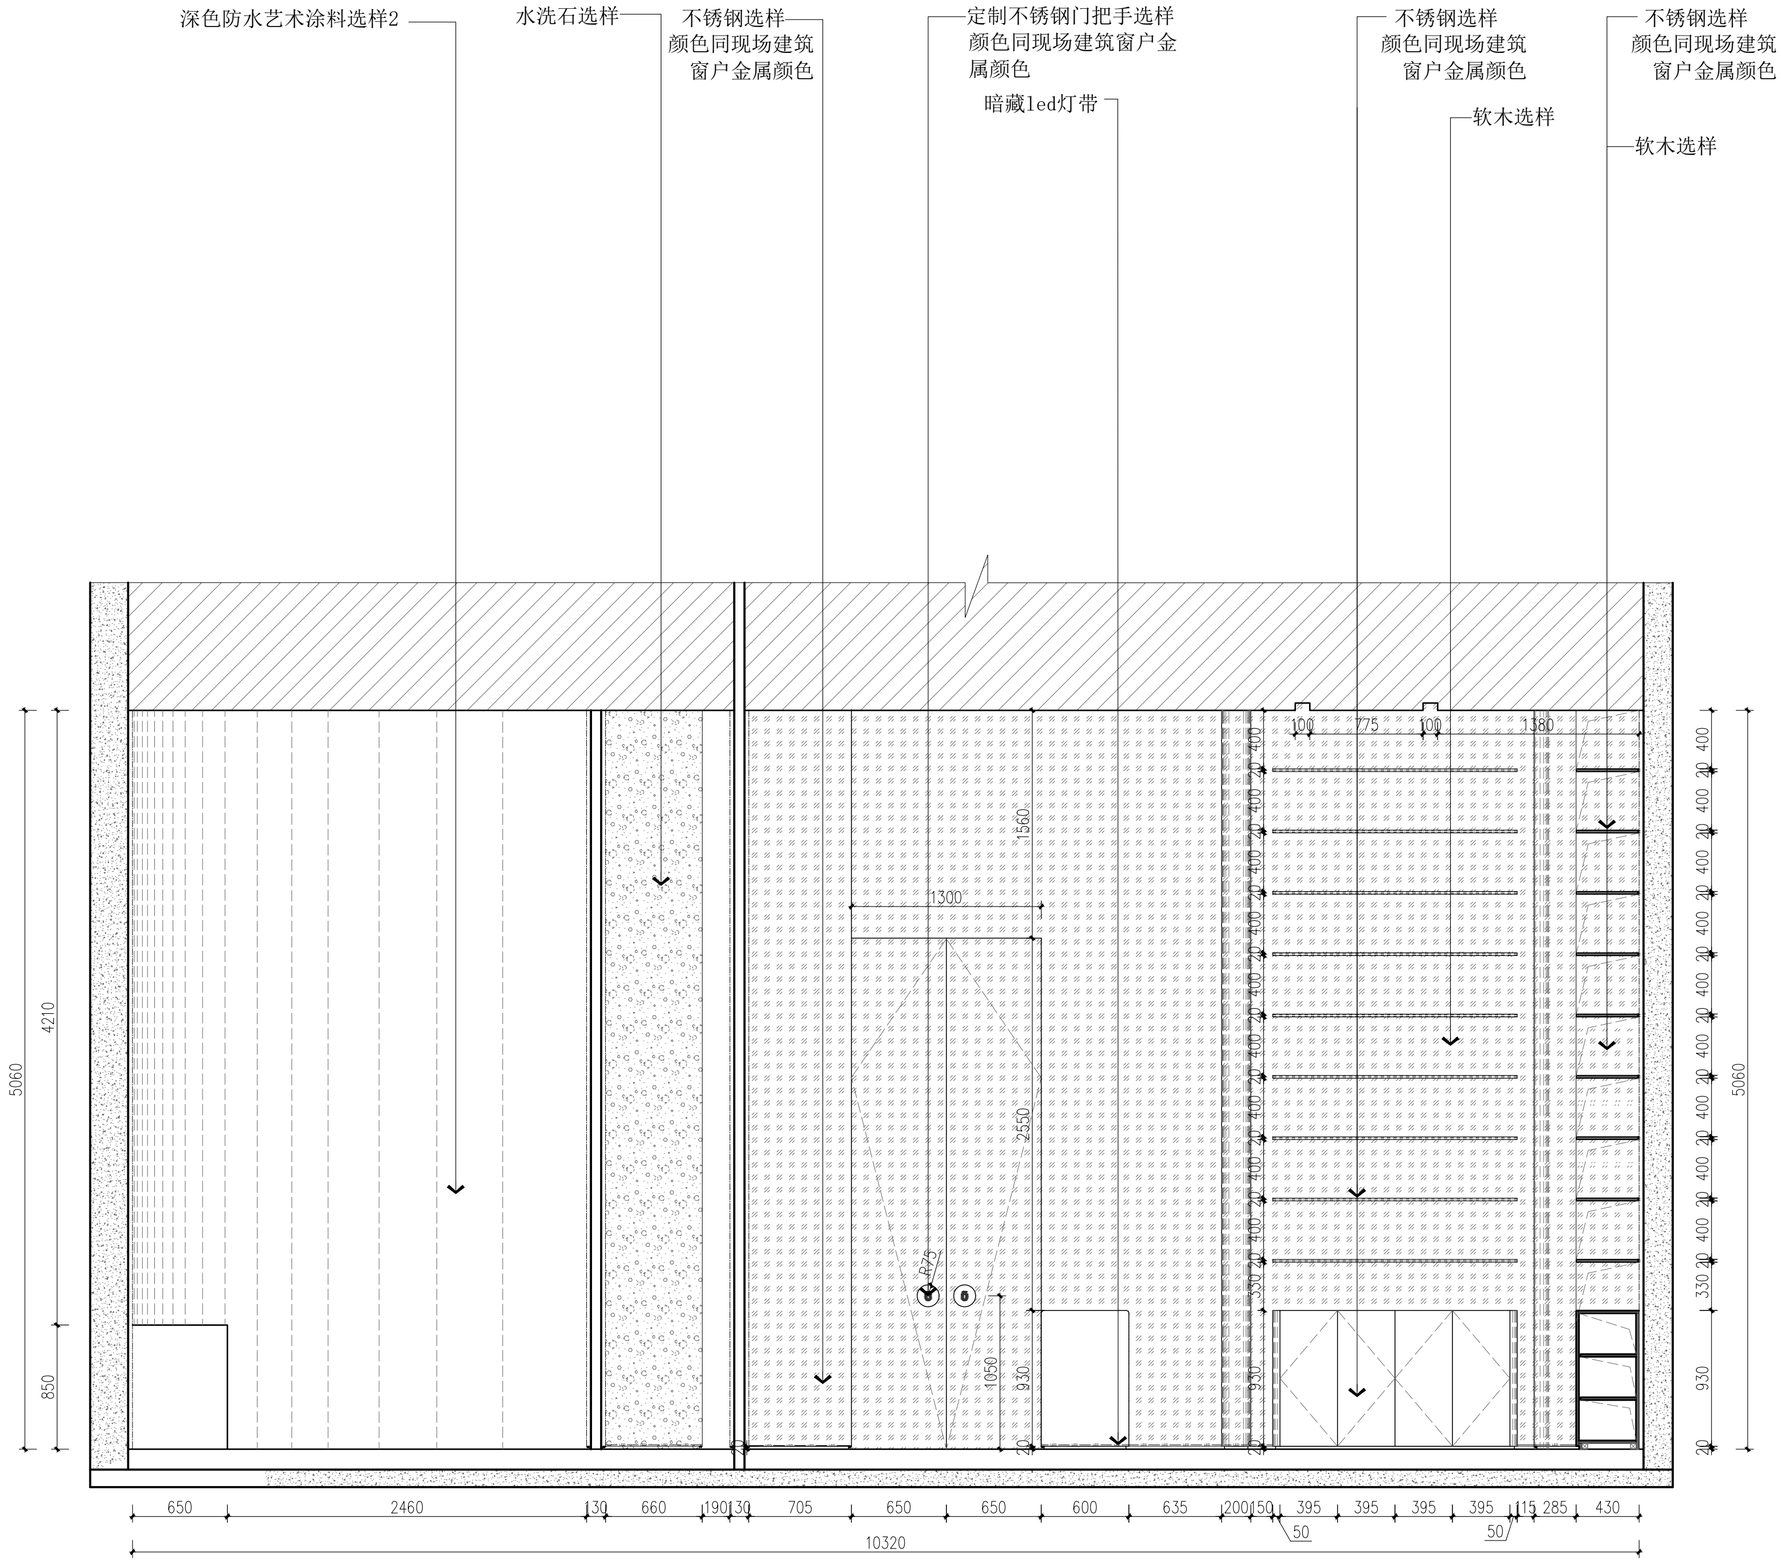

3 ELEVATION 立面图 SCALE:1/40

ESSENZA ARMONIOSA
architecture interiors

中国 杭州
TEL: 180 6796 1470
FAX: 180 6796 1470

图注: Exegesis

建设单位 Construction unit

设计单位 Engineering design company

顾问单位 Consultant unit

工程名称 project name

FIONA SHANGHAI

审 定		
审 核		
校 对		
项目负责人		
设 计		
制 图		

图 名

立面图


图 号	EL-03
比 例	1:40
日 期	2026.08
专 业	装饰
设计阶段	施工图
版本编号	
设计编号	

出 图 盖 章

此设计图则之版权归杭州光几建筑室内设计有限公司所有 非得建筑师或设计师之书面批准 不得随意将任何部分翻印 切勿以比例量度此图 一切依图内数字所示为准承建人必须在工场核对图内所示数字之准则如发现有任何矛盾处应立即通知建筑师或设计师

ALL DESIGNS ARE THE SOLE PROPERTY OF HANGZHOU , LTD. AND CANNOT BE USED WITHOUT WRITTEN PERMISSION.DO NOT SCALE DRAWING FIGURED DIMENSIONS ARE TO BE FOLLOWED ALL MEASUREMENTS MUST BE CHECKED ON SITE BY THE CONTRACTOR ANYDISCREPANCIES SHOULD BE REPORTED TO THE ARCHITECT OR DESIGNER

A3-420*297

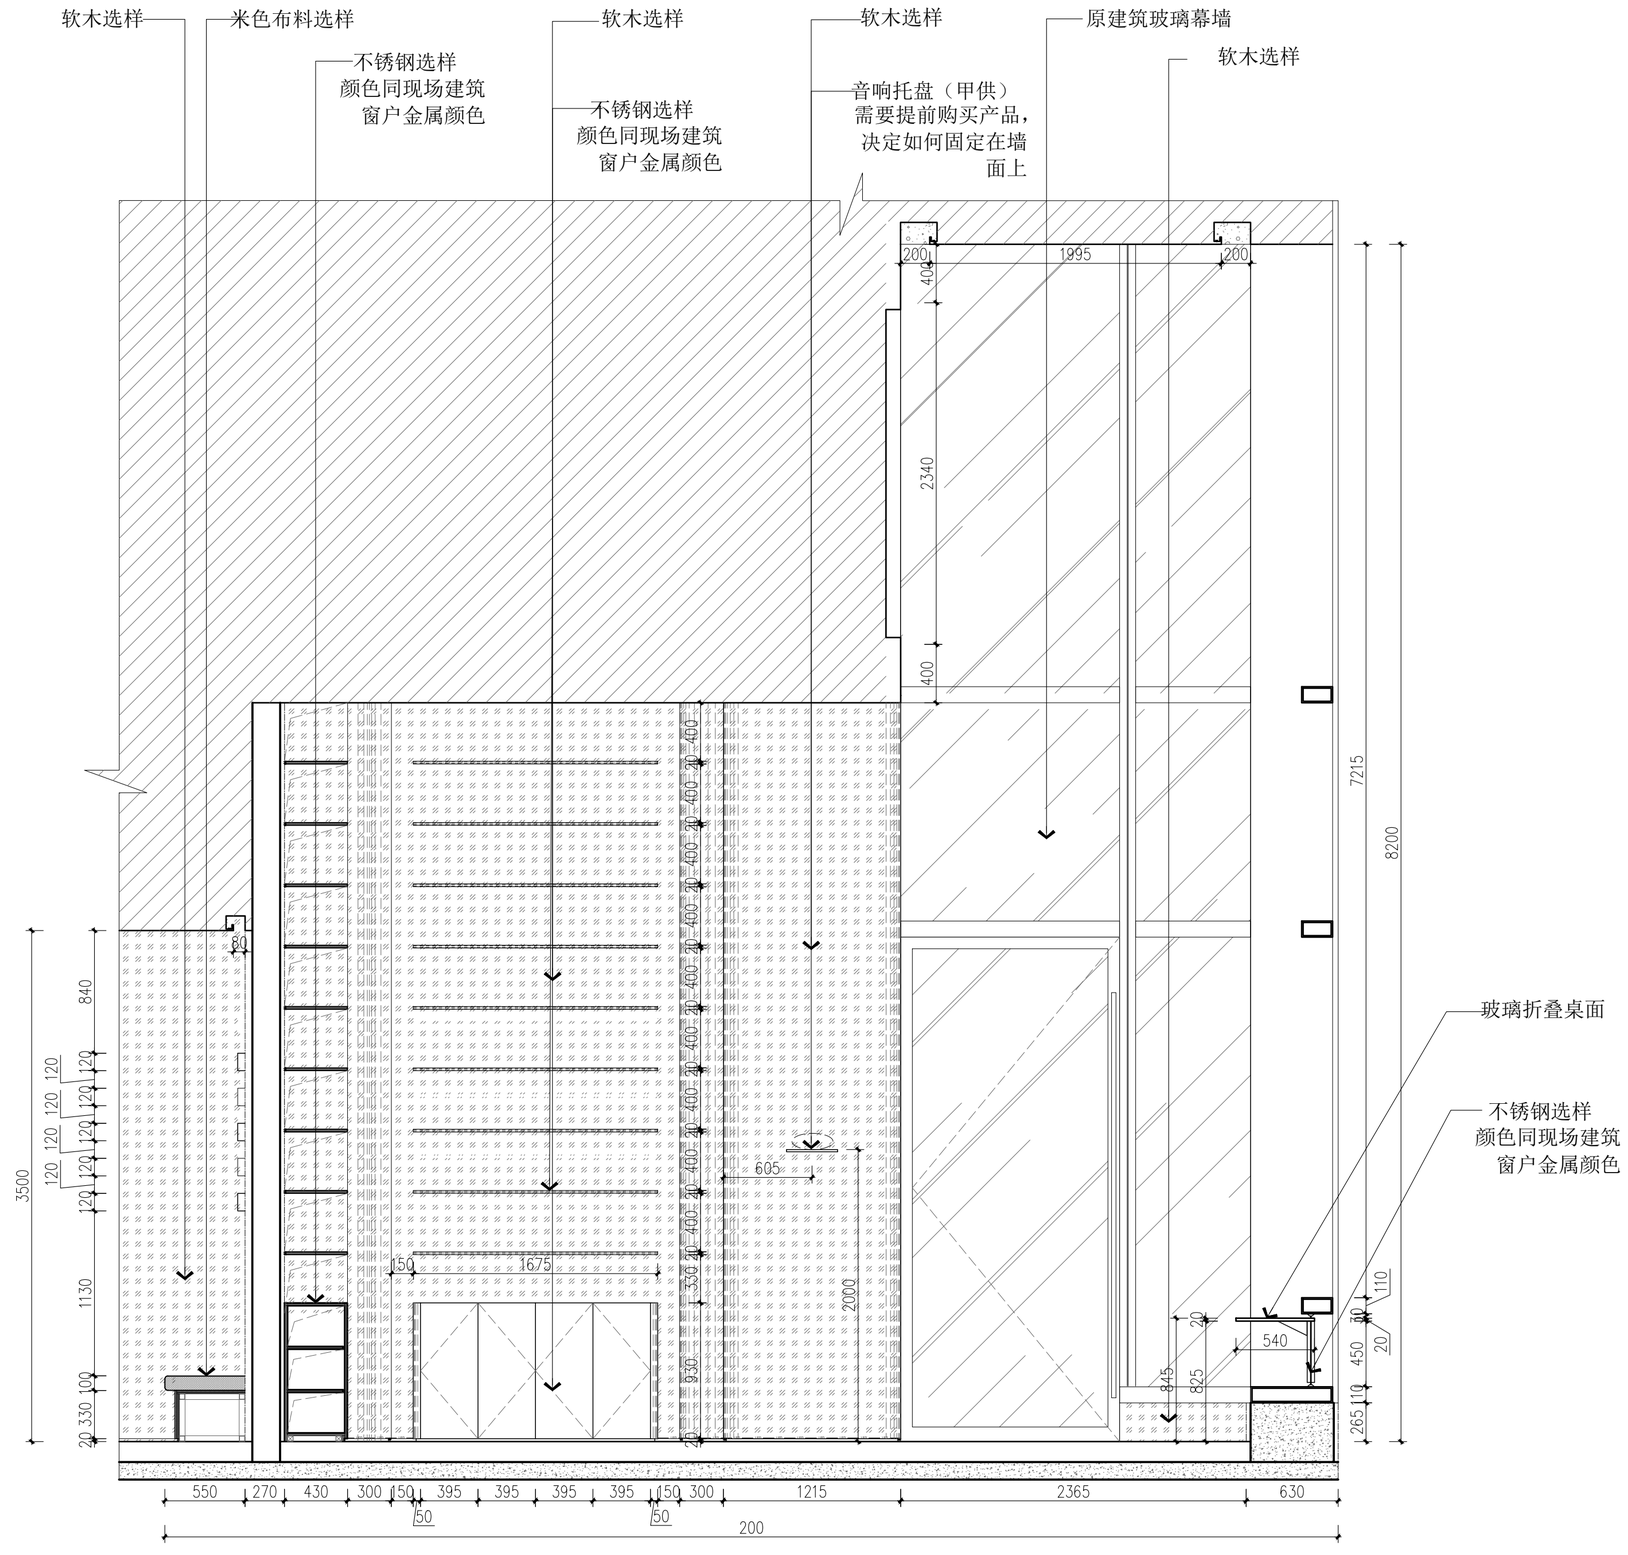

4 ELEVATION 立面图 SCALE:1/40

会签 建筑 电气 结构 暖通 给排水 动力

ESSENZA ARMONIOSA
architecture
interiors

中国 杭州
TEL: 180 6796 1470
FAX: 180 6796 1470

图注: Exegesis

建设单位 Construction unit

设计单位 Engineering design company

顾问单位 Consultant unit

工程名称 project name

FIONA SHANGHAI

审 定		
审 核		
校 对		
项目负责人		
设 计		
制 图		

图 名

立面图


图 号	EL-04
比 例	1:40
日 期	2026.08
专 业	装饰
设计阶段	施工图
版本编号	
设计编号	

出 图 盖 章

此设计图则之版权归杭州光几建筑室内设计有限公司所有 非得建筑师或设计师之书面批准 不得随意将任何部分翻印 切勿以比例量度此图 一切依图内数字所示为准承建人必须在工场核对图内所示数字之准则如发现有任何矛盾处应立即通知建筑师或设计师

ALL DESIGNS ARE THE SOLE PROPERTY OF HANGZHOU , LTD. AND CANNOT BE USED WITHOUT WRITTEN PERMISSION.DO NOT SCALE DRAWING FIGURED DIMENSIONS ARE TO BE FOLLOWED ALL MEASUREMENTS MUST BE CHECKED ON SITE BY THE CONTRACTOR ANYDISCREPANCIES SHOULD BE REPORTED TO THE ARCHITECT OR DESIGNER

A3-420*297

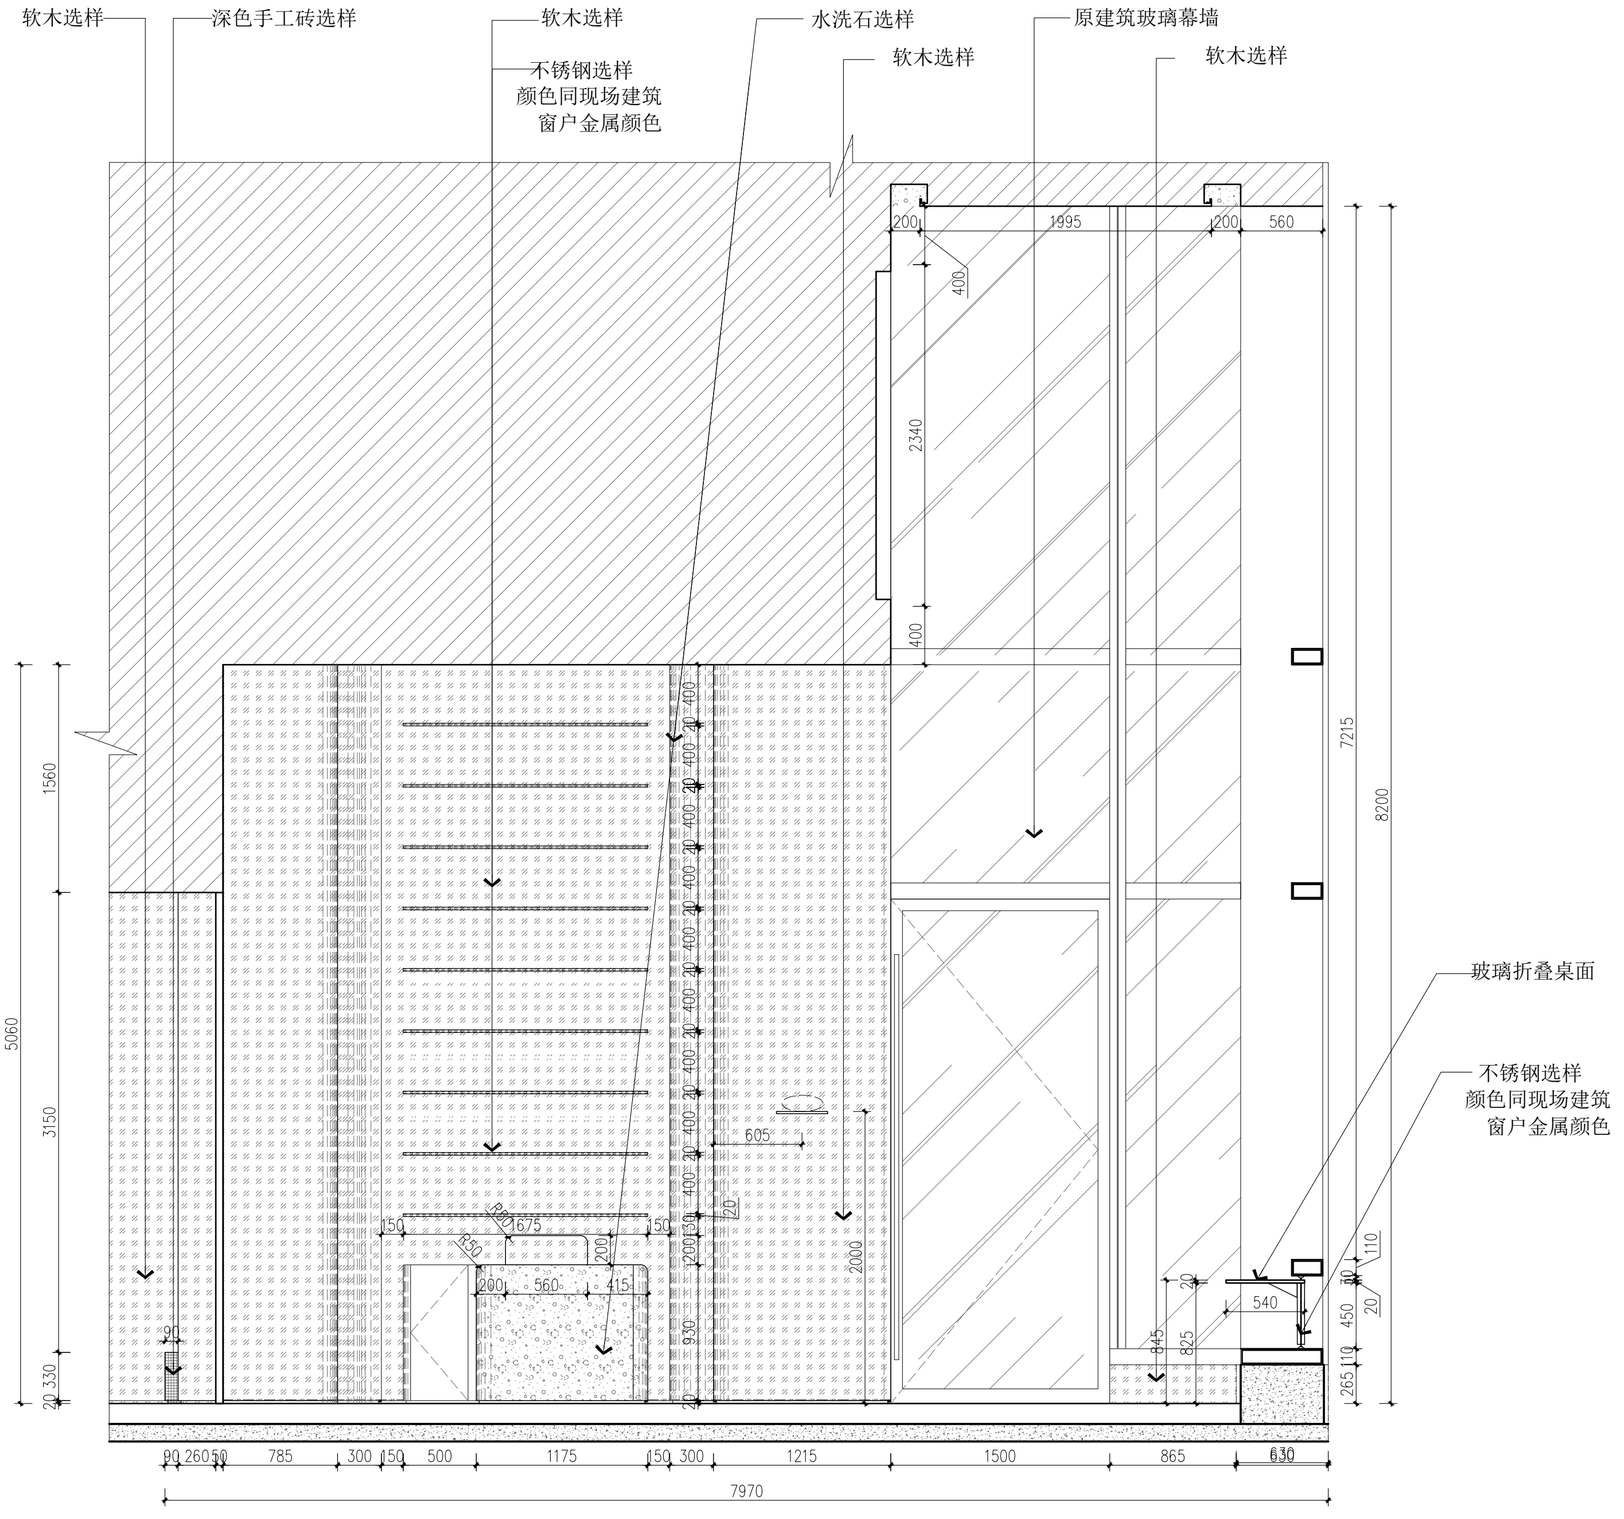

5 ELEVATION 立面图 SCALE:1/40

会签 | 建筑 | 电气 | 结构 | 暖通 | 给排水 | 动力

ESSENZA ARMONIOSA
architecture interiors

中国 杭州
TEL: 180 6796 1470
FAX: 180 6796 1470

图注: Exegesis

建设单位 Construction unit

设计单位 Engineering design company

顾问单位 Consultant unit

工程名称 project name

FIONA SHANGHAI

审 定		
审 核		
校 对		
项目负责人		
设 计		
制 图		

图 名 立面图

图 号	EL-05
比 例	1:40
日 期	2026.08
专 业	装饰
设计阶段	施工图
版本编号	
设计编号	


出 图 盖 章

此设计图则之版权归杭州光几建筑室内设计有限公司所有 非得建筑师或设计师之书面批准 不得随意将任何部分翻印 切勿以比例量度此图 一切依图内数字所示为准承建人必须在工场核对图内所示数字之准则如发现有任何矛盾处应立即通知建筑师或设计师

ALL DESIGNS ARE THE SOLE PROPERTY OF HANGZHOU , LTD. AND CANNOT BE USED WITHOUT WRITTEN PERMISSION.DO NOT SCALE DRAWING. FIGURED DIMENSIONS ARE TO BE FOLLOWED. ALL MEASUREMENTS MUST BE CHECKED ON SITE BY THE CONTRACTOR. ANYDISCREPANCIES SHOULD BE REPORTED TO THE ARCHITECT OR DESIGNER.

A3-420*297

会签 | 建筑 | 电气 | 结构 | 暖通 | 给排水 | 动力

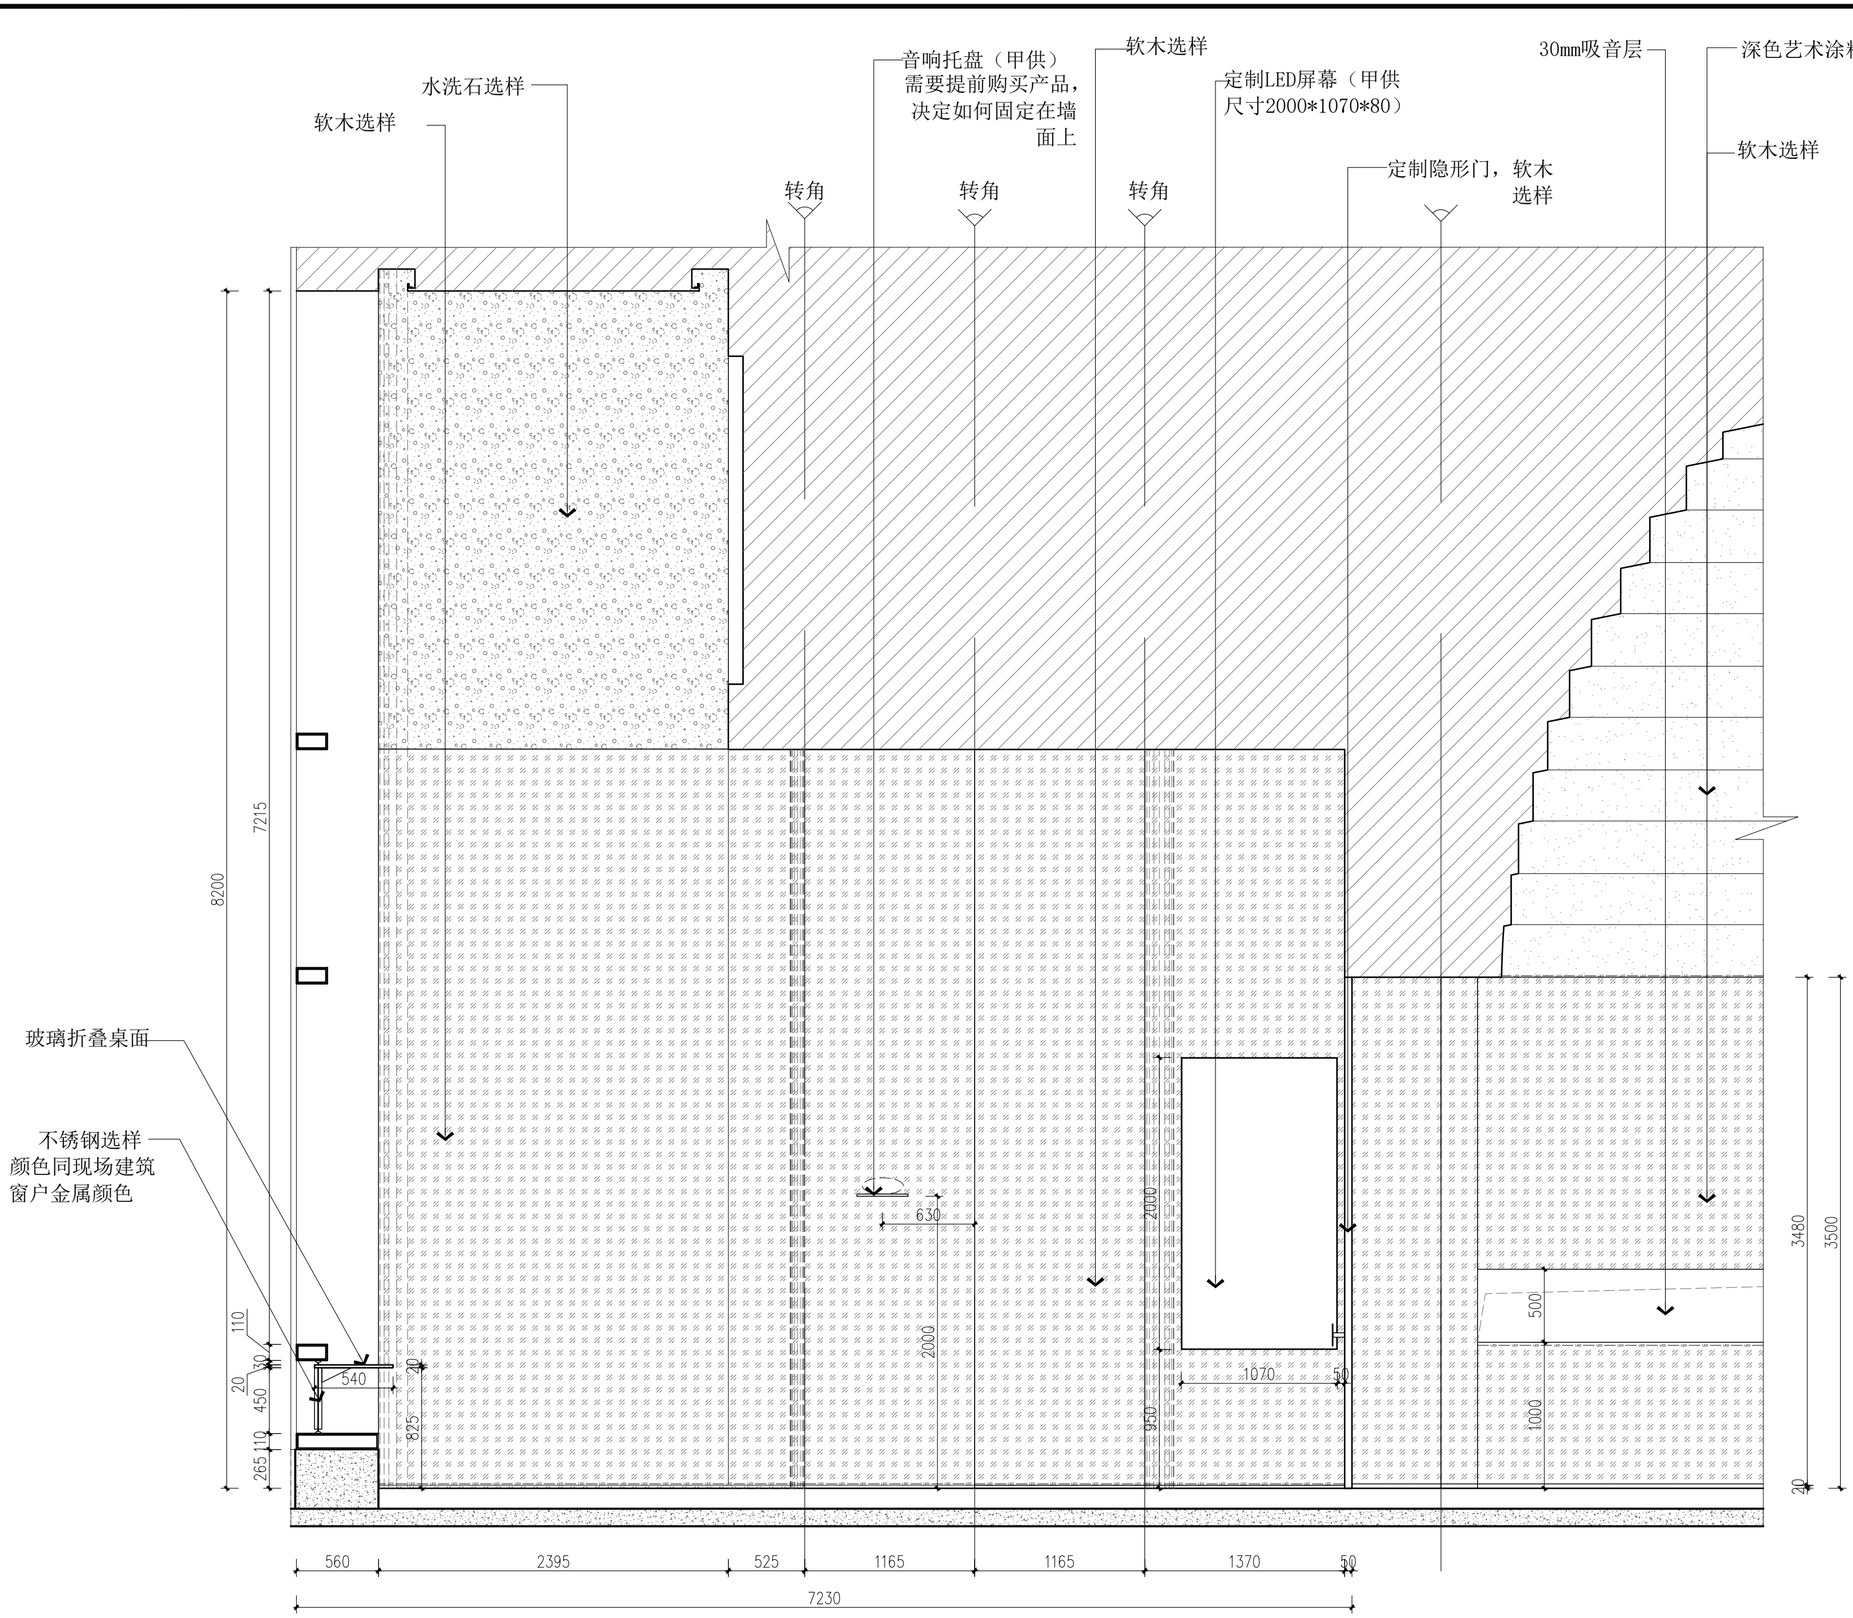

6 ELEVATION 立面图 SCALE:1/40

ESSENZA ARMONIOSA
architecture
interiors

中国 杭州
TEL: 180 6796 1470
FAX: 180 6796 1470

图注：Exegesis

建设单位 Construction unit

设计单位 Engineering design company

顾问单位 Consultant unit

工程名称 project name

FIONA SHANGHAI

审 定		
审 核		
校 对		
项目负责人		
设 计		
制 图		

图 名
立面图

图 号	EL-06
比 例	1:40
日 期	2026.08
专 业	装饰
设计阶段	施工图
版本编号	
设计编号	


出 图 盖 章

此设计图则之版权归杭州光几建筑室内设计有限公司所有 非得建筑师或设计师之书面批准 不得随意将任何部分翻印 切勿以比例量度此图 一切依图内数字所示为准承建人必须在工场核对图内所示数字之准则如发现有任何矛盾处应立即通知建筑师或设计师

ALL DESIGNS ARE THE SOLE PROPERTY OF HANGZHOU + LTD. AND CANNOT BE USED WITHOUT WRITTEN PERMISSION.DO NOT SCALE DRAWING FIGURED DIMENSIONS ARE TO BE FOLLOWED ALL MEASUREMENTS MUST BE CHECKED ON SITE BY THE CONTRACTOR ANYDISCREPANCIES SHOULD BE REPORTED TO THE ARCHITECT OR DESIGNER

A3-420*297

会签 | 建筑 | 电气 | 结构 | 暖通 | 给排水 | 动力

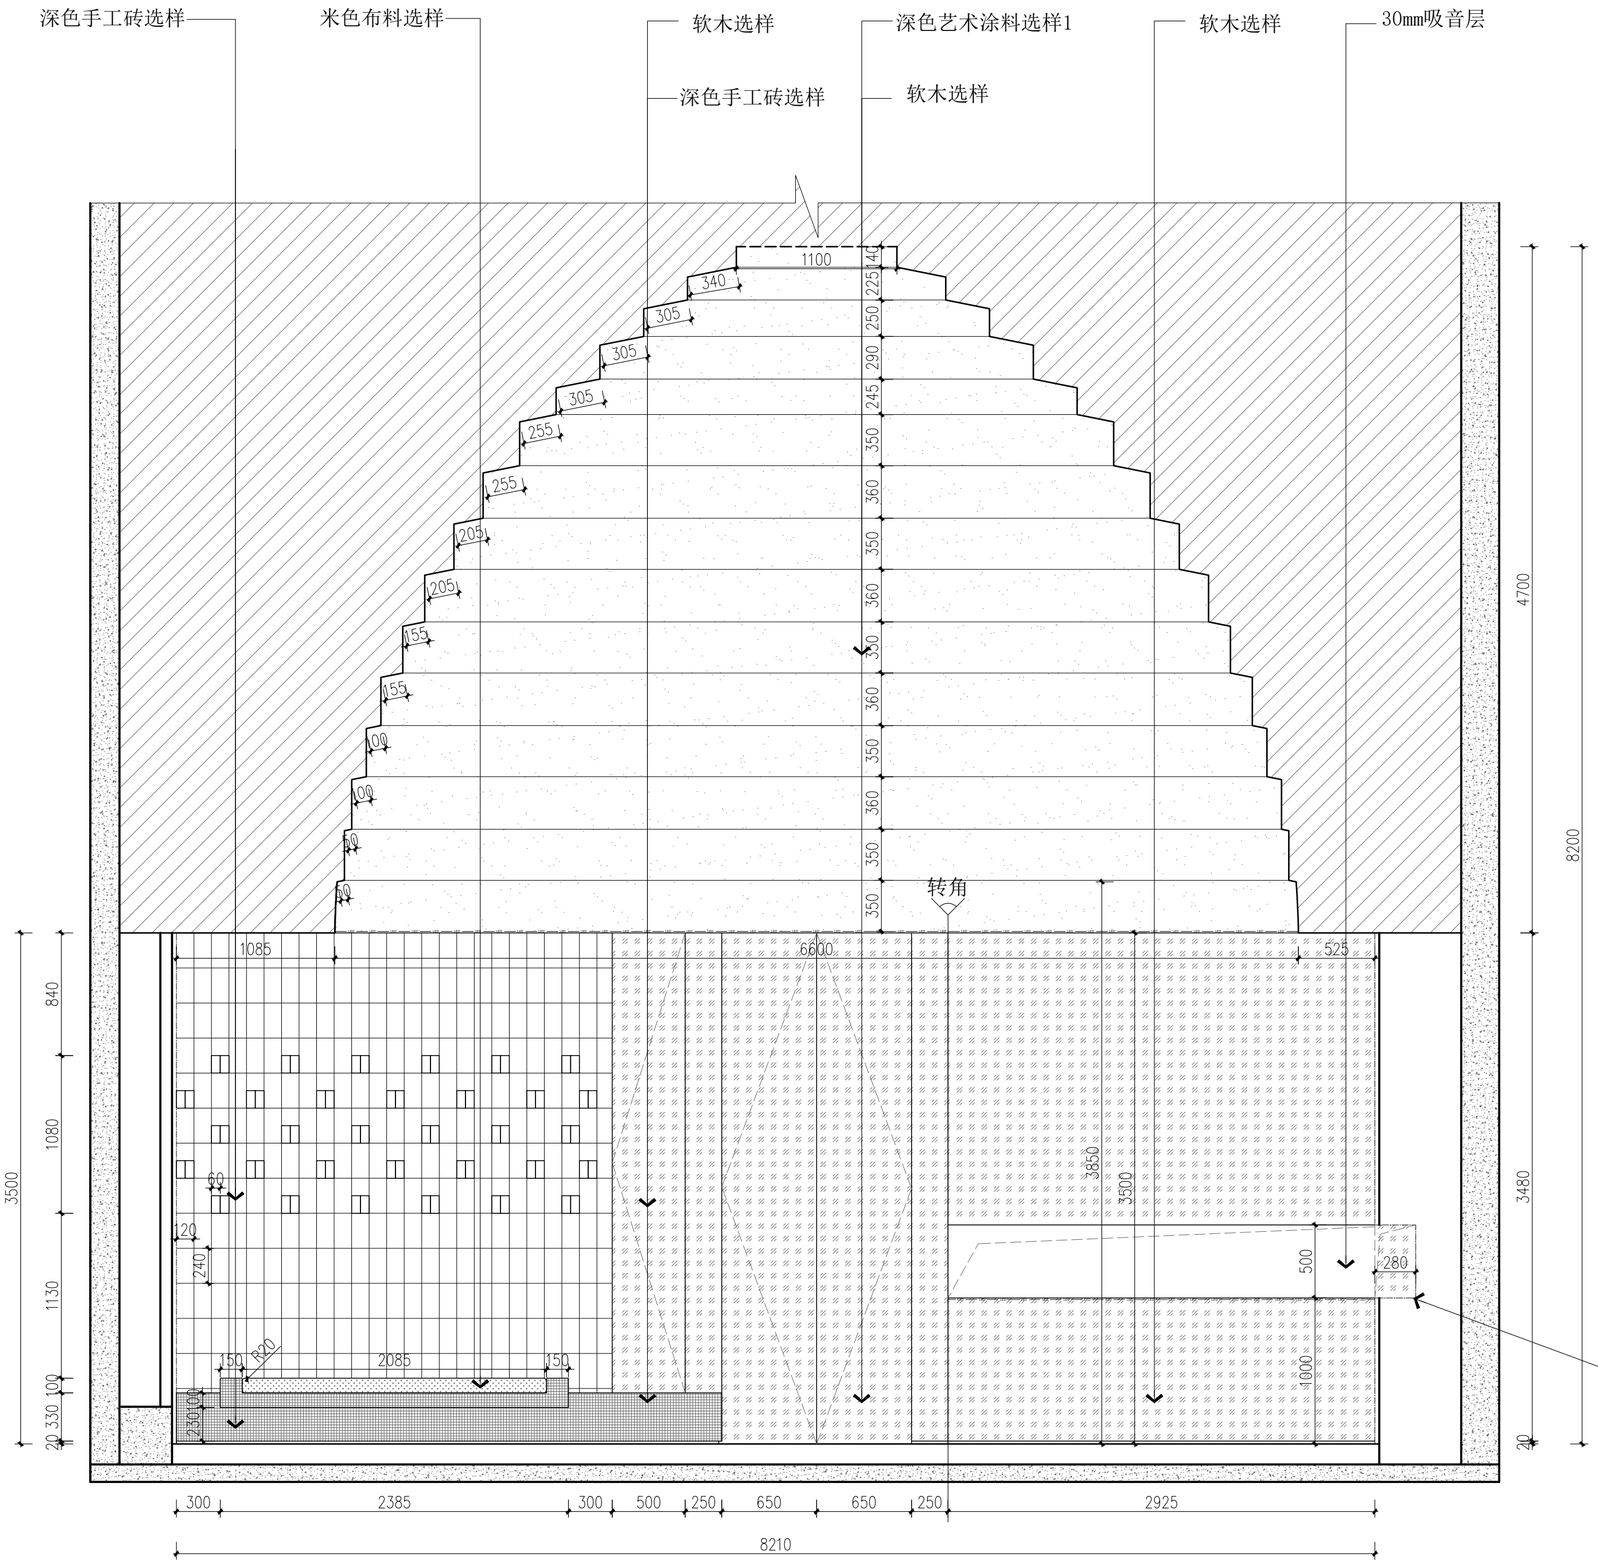

7 ELEVATION 立面图 SCALE:1/40

ESSENZA ARMONIOSA
architecture interiors

中国 杭州
TEL: 180 6796 1470
FAX: 180 6796 1470

图注: Exegesis

建设单位 Construction unit

设计单位 Engineering design company

顾问单位 Consultant unit

工程名称 project name

FIONA SHANGHAI

审 定		
审 核		
校 对		
项目负责人		
设 计		
制 图		

图 名

立面图

图 号	EL-07
比 例	1:40
日 期	2026.08
专 业	装饰
设计阶段	施工图
版本编号	
设计编号	

出 图 盖 章

此设计图则之版权归杭州光几建筑室内设计有限公司所有 非得建筑师或设计师之书面批准 不得随意将任何部分翻印 切勿以比例量度此图 一切依图内数字所示为准承建人必须在工场核对图内所示数字之准则如发现有任何矛盾处应立即通知建筑师或设计师

ALL DESIGNS ARE THE SOLE PROPERTY OF HANGZHOU , LTD. AND CANNOT BE USED WITHOUT WRITTEN PERMISSION.DO NOT SCALE DRAWING FIGURED DIMENSIONS ARE TO BE FOLLOWED ALL MEASUREMENTS MUST BE CHECKED ON SITE BY THE CONTRACTOR ANYDISCREPANCIES SHOULD BE REPORTED TO THE ARCHITECT OR DESIGNER


A3-420*297

会签

建筑 | 电气

结构 | 暖通

给排水 | 动力

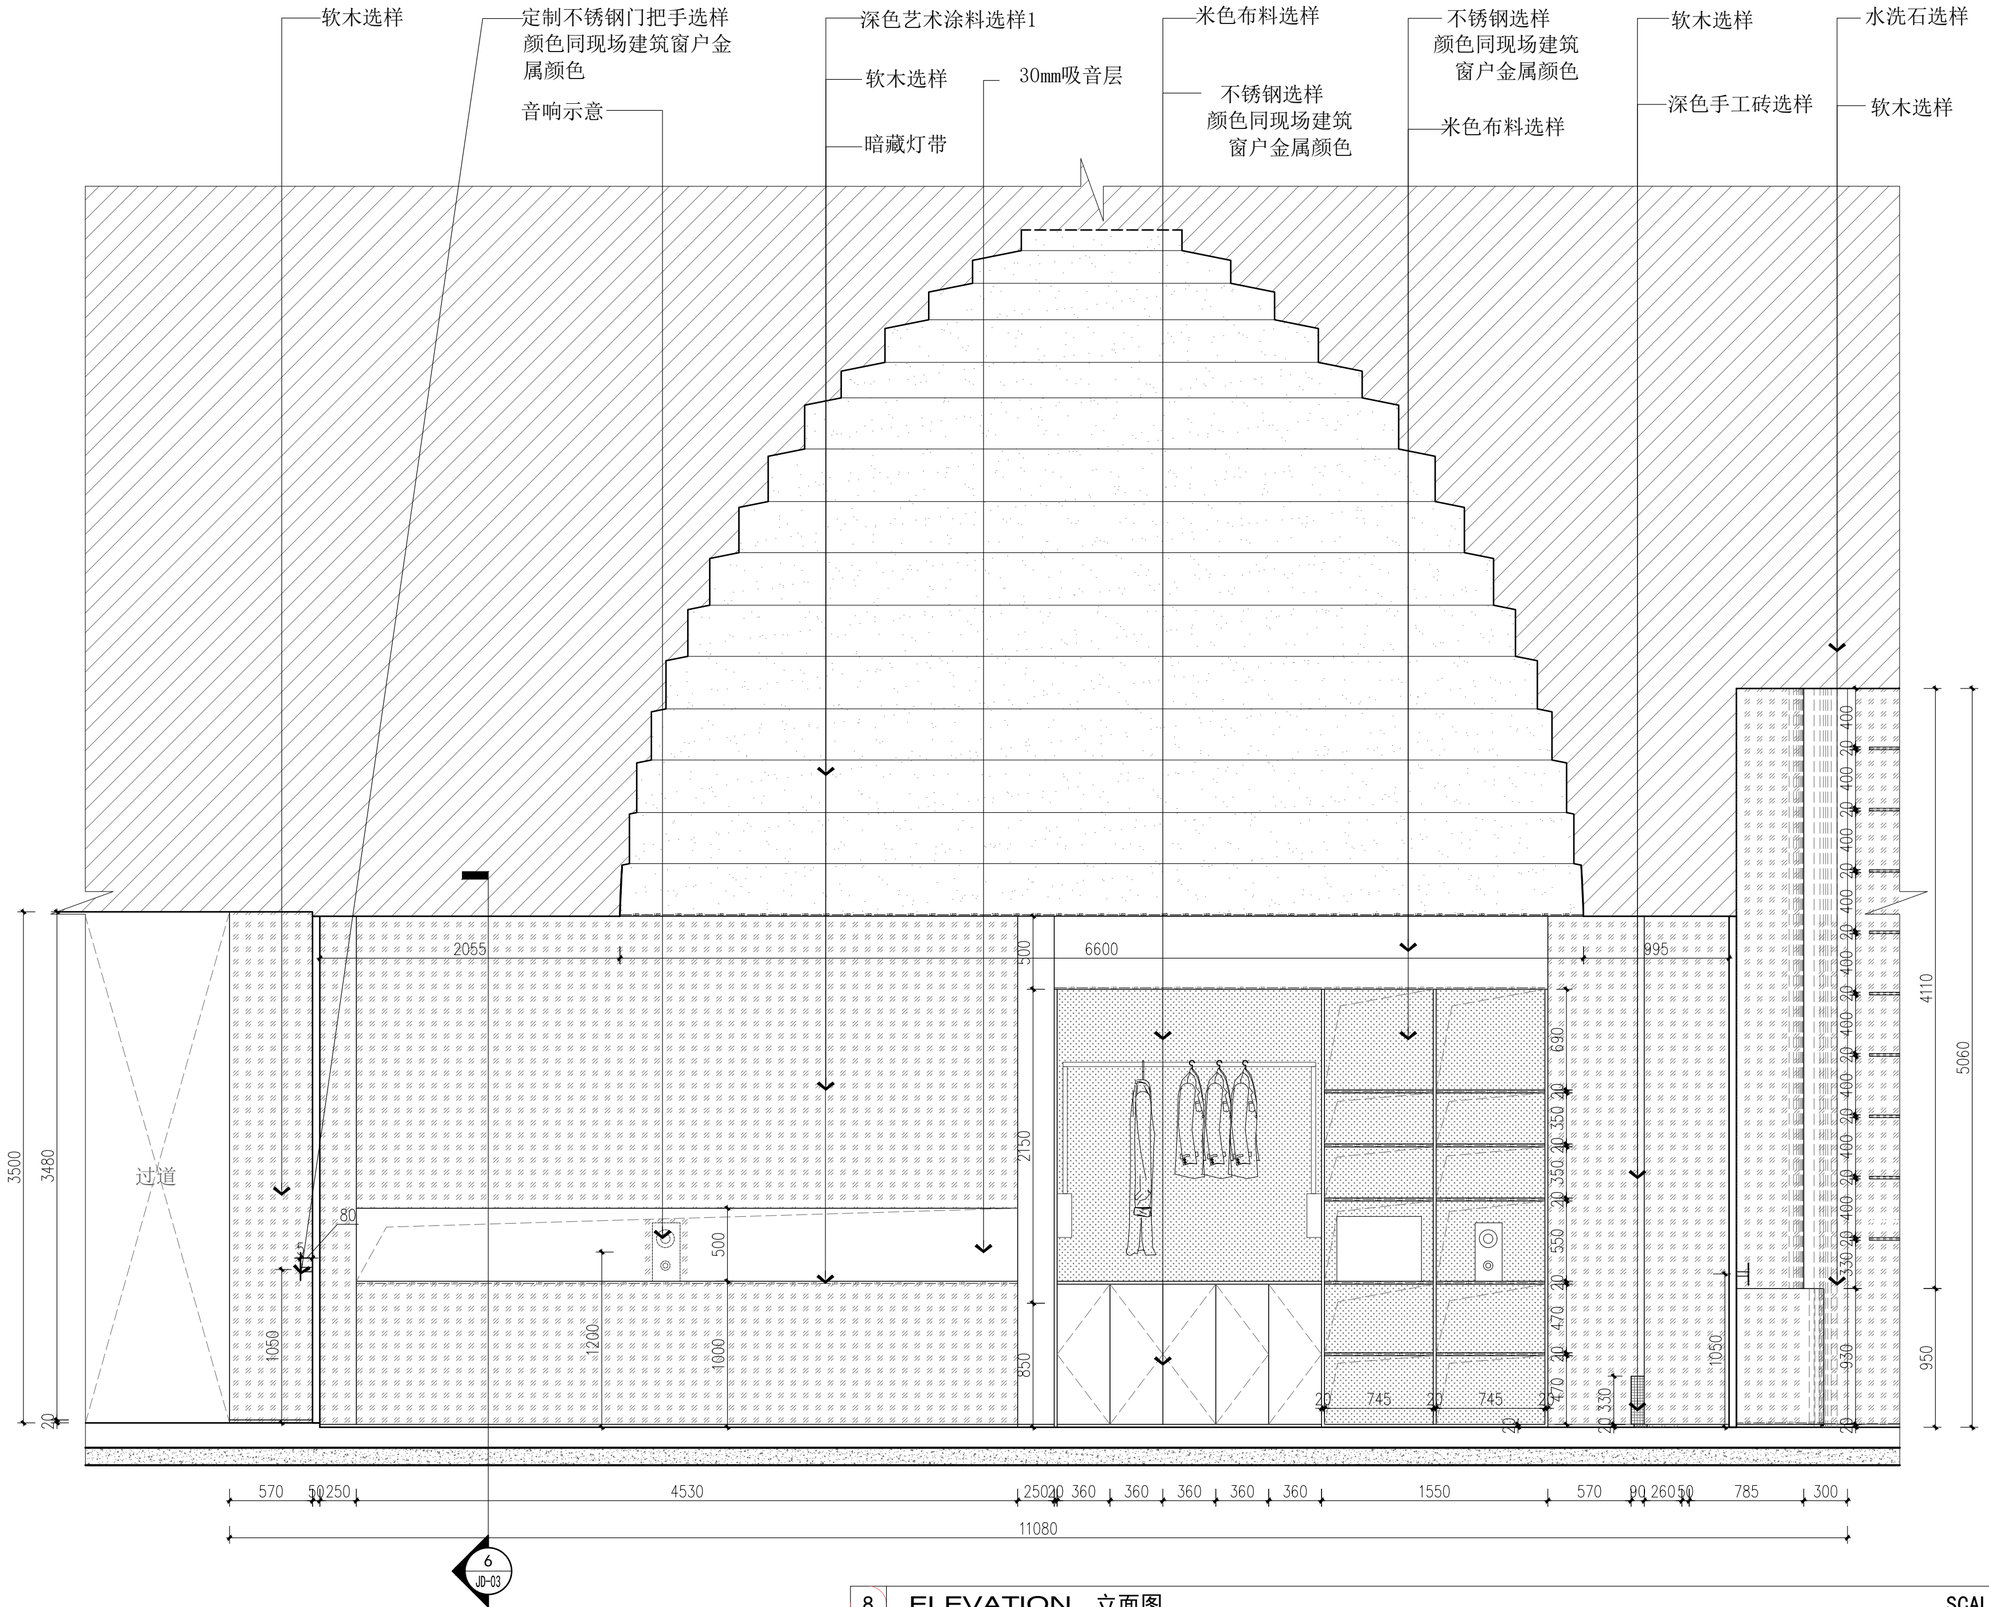

8 ELEVATION 立面图 SCALE:1/40

ESSENZA ARMONIOSA
architecture interiors

中国 杭州
TEL: 180 6796 1470
FAX: 180 6796 1470

图注: Exegesis

建设单位 Construction unit

设计单位 Engineering design company

顾问单位 Consultant unit

工程名称 project name

FIONA SHANGHAI

审 定		
审 核		
校 对		
项目负责人		
设 计		
制 图		

图 名: 立面图

图 号	EL-08
比 例	1:40
日 期	2026.08
专 业	装饰
设计阶段	施工图
版本编号	
设计编号	


出 图 盖 章

此设计图则之版权归杭州光几建筑室内设计有限公司所有 非得建筑师或设计师之书面批准 不得随意将任何部分翻印 切勿以比例量度此图 一切依图内数字所示为准承建人必须在工场核对图内所示数字之准则如发现有任何矛盾处应立即通知建筑师或设计师

ALL DESIGNS ARE THE SOLE PROPERTY OF HANGZHOU , LTD. AND CANNOT BE USED WITHOUT WRITTEN PERMISSION.DO NOT SCALE DRAWING FIGURED DIMENSIONS ARE TO BE FOLLOWED.ALL MEASUREMENTS MUST BE CHECKED ON SITE BY THE CONTRACTOR ANYDISCREPANCIES SHOULD BE REPORTED TO THE ARCHITECT OR DESIGNER.

A3-420*297

会签 | 建筑 | 电气 | 结构 | 暖通 | 给排水 | 动力

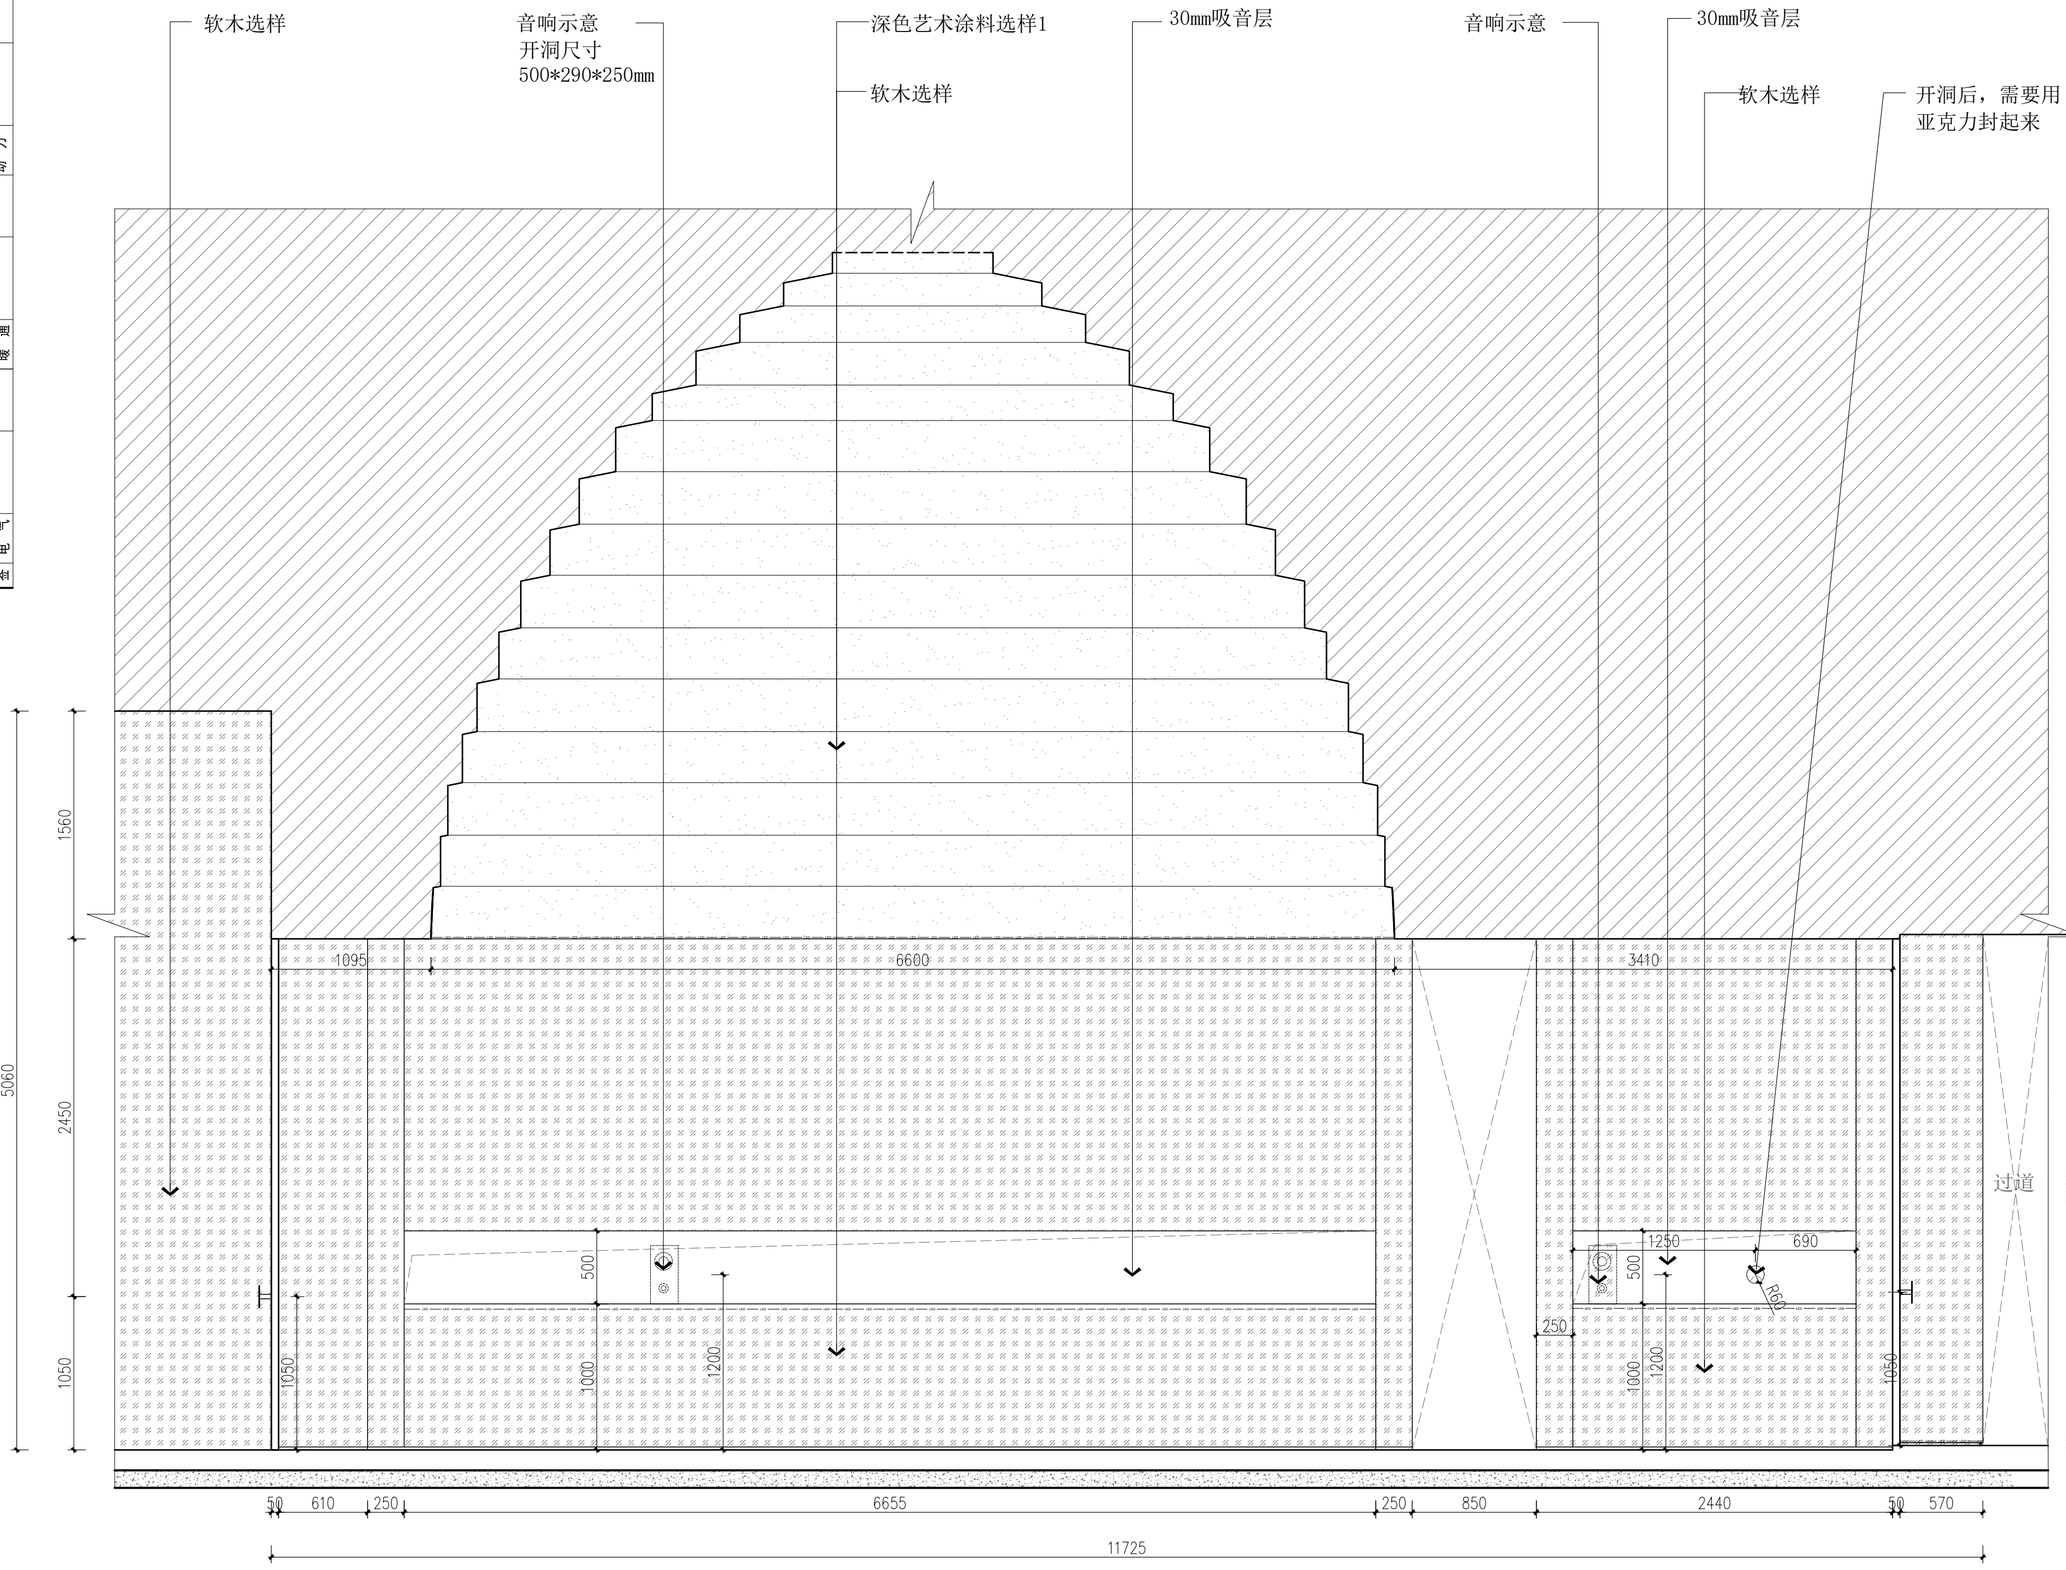

9 ELEVATION 立面图 SCALE:1/40

ESSENZA ARMONIOSA
architecture interiors

中国 杭州
TEL: 180 6796 1470
FAX: 180 6796 1470

图注: Exegesis

建设单位 Construction unit

设计单位 Engineering design company

顾问单位 Consultant unit

工程名称 project name

FIONA SHANGHAI

审 定		
审 核		
校 对		
项目负责人		
设 计		
制 图		

图 名 立面图

图 号	EL-09
比 例	1:40
日 期	2026.08
专 业	装饰
设计阶段	施工图
版本编号	
设计编号	


出 图 盖 章

此设计图则之版权归杭州光几建筑室内设计有限公司所有 非得建筑师或设计师之书面批准 不得随意将任何部分翻印 切勿以比例量度此图 一切依图内数字所示为准承建人必须在工场核对图内所示数字之准则如发现有任何矛盾处应立即通知建筑师或设计师


ALL DESIGNS ARE THE SOLE PROPERTY OF HANGZHOU , LTD, AND CANNOT BE USED WITHOUT WRITTEN PERMISSION.DO NOT SCALE DRAWING FIGURED DIMENSIONS ARE TO BE FOLLOWED ALL MEASUREMENTS MUST BE CHECKED ON SITE BY THE CONTRACTOR ANYDISCREPANCIES SHOULD BE REPORTED TO THE ARCHITECT OR DESIGNER

A3-420*297


会签 | 建筑 | 电气 | 结构 | 暖通 | 给排水 | 动力

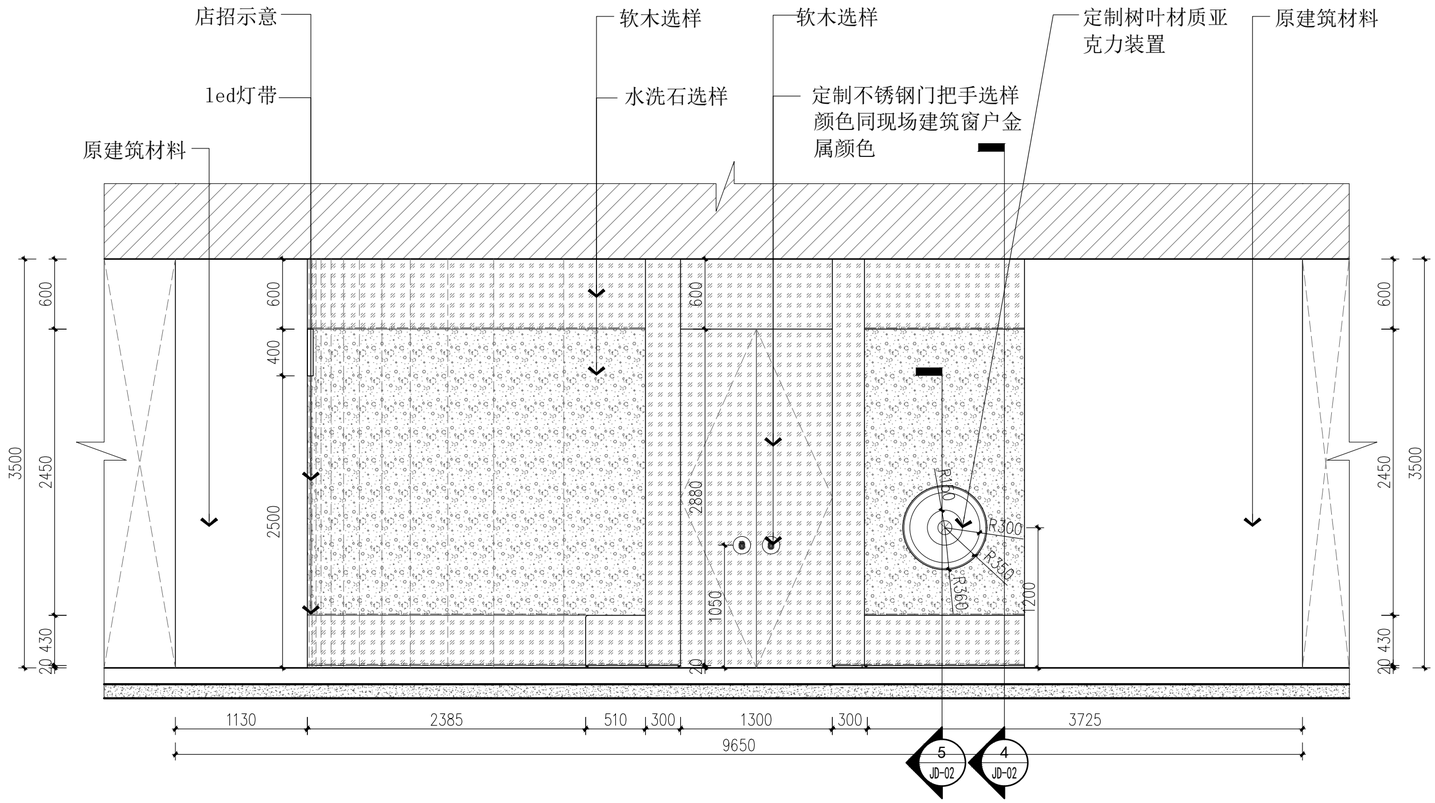

10 ELEVATION 立面图 SCALE:1/40

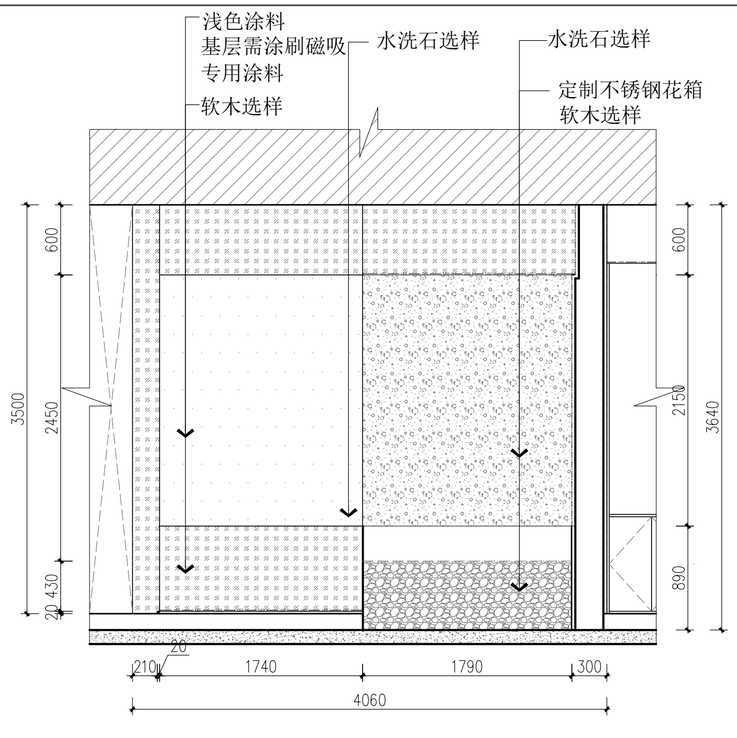

11 ELEVATION 立面图 SCALE:1/50

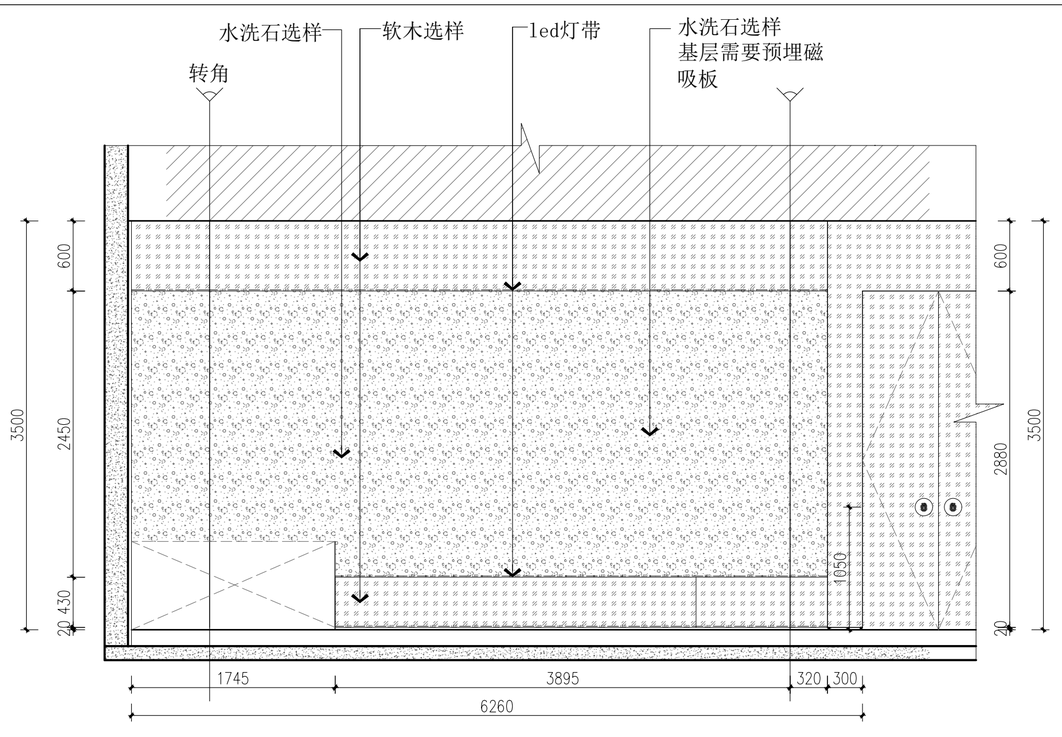

12 ELEVATION 立面图 SCALE:1/50

ESSENZA ARMONIOSA
architecture interiors

中国 杭州
TEL: 180 6796 1470
FAX: 180 6796 1470

图注: Exegesis

建设单位 Construction unit

设计单位 Engineering design company

顾问单位 Consultant unit

工程名称 project name

FIONA SHANGHAI

审 定		
审 核		
校 对		
项目负责人		
设 计		
制 图		

图 名

立面图


图 号	EL-10
比 例	
日 期	2026.08
专 业	装饰
设计阶段	施工图
版本编号	
设计编号	

出 图 盖 章

此设计图则之版权归杭州光几建筑室内设计有限公司所有 非得建筑师或设计师之书面批准 不得随意将任何部分翻印 切勿以比例量度此图 一切依图内数字所示为准承建人必须在工场核对图内所示数字之准则如发现有任何矛盾处应立即通知建筑师或设计师

ALL DESIGNS ARE THE SOLE PROPERTY OF HANGZHOU , LTD. AND CANNOT BE USED WITHOUT WRITTEN PERMISSION.DO NOT SCALE DRAWING FIGURED DIMENSIONS ARE TO BE FOLLOWED ALL MEASUREMENTS MUST BE CHECKED ON SITE BY THE CONTRACTOR ANYDISCREPANCIES SHRULD BE REPORTED TO THE ARCHITECT OR DESIGNER

A3-420*297

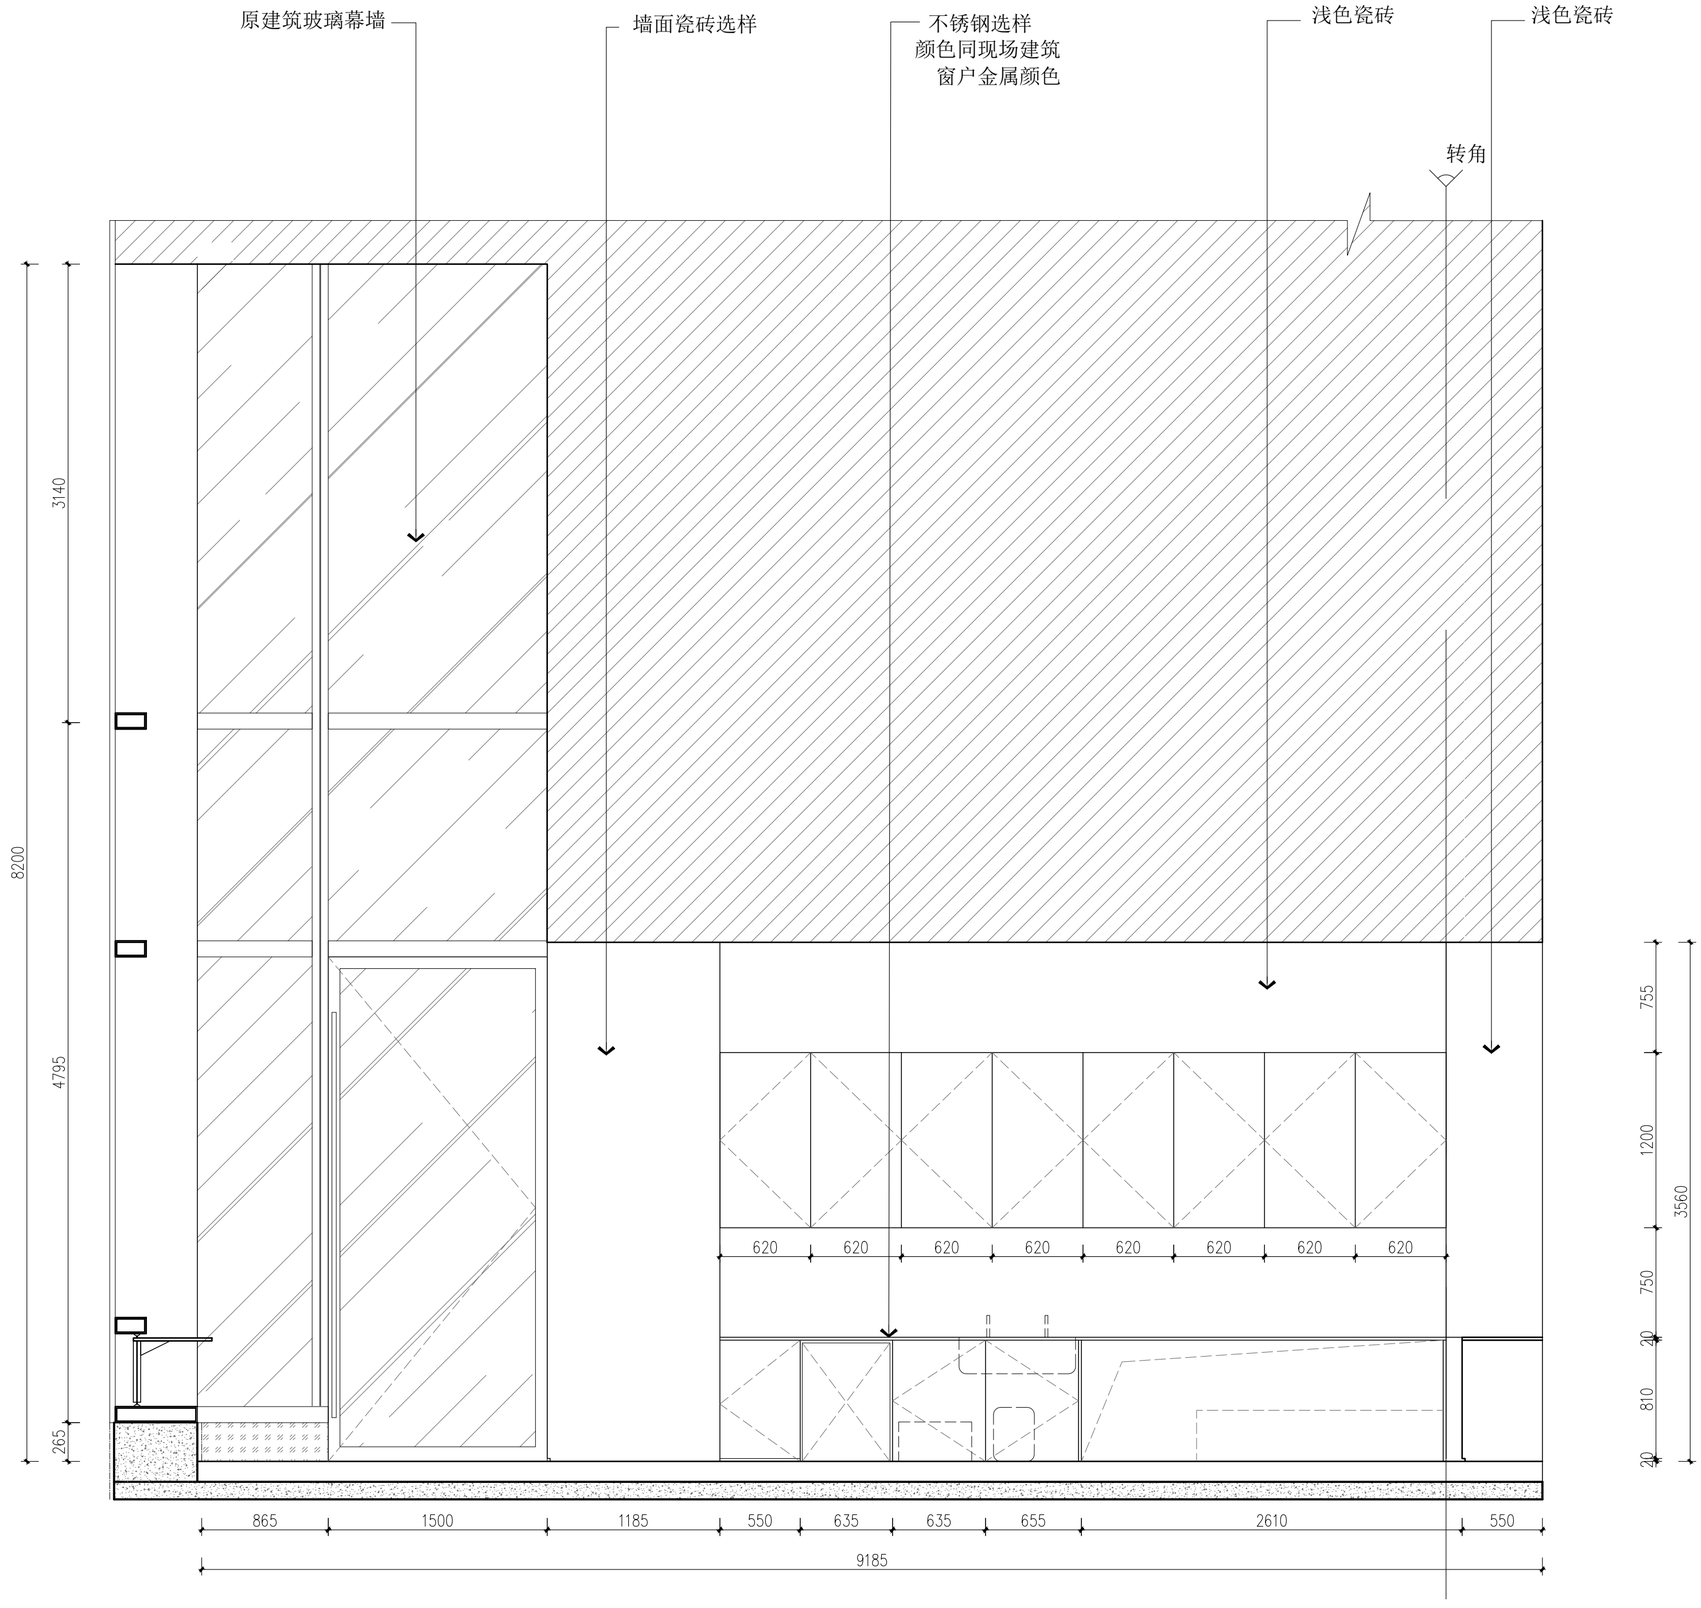

会签 | 建筑 电气 | 结构 暖通 | 给排水 动力

ESSENZA ARMONIOSA
architecture
interiors

中国 杭州
TEL: 180 6796 1470
FAX: 180 6796 1470

图注: Exegesis

建设单位 Construction unit

设计单位 Engineering design company

顾问单位 Consultant unit

工程名称 project name

FIONA SHANGHAI

审 定		
审 核		
校 对		
项目负责人		
设 计		
制 图		

图 名

立面图

图 号	EL-11
比 例	
日 期	2026.08
专 业	装饰
设计阶段	施工图
版本编号	
设计编号	


出 图 盖 章

此设计图则之版权归杭州光几建筑室内设计有限公司所有 非得建筑师或设计师之书面批准 不得随意将任何部分翻印 切勿以比例量度此图 一切依图内数字所示为准承建人必须在工场核对图内所示数字之准则如发现有任何矛盾处应立即通知建筑师或设计师

ALL DESIGNS ARE THE SOLE PROPERTY OF HANGZHOU , LTD. AND CANNOT BE USED WITHOUT WRITTEN PERMISSION.DO NOT SCALE DRAWING FIGURED DIMENSIONS ARE TO BE FOLLOWED. ALL MEASUREMENTS MUST BE CHECKED ON SITE BY THE CONTRACTOR. ANYDISCREPANCIES SHOULD BE REPORTED TO THE ARCHITECT OR DESIGNER.

13 ELEVATION 立面图

SCALE:1/40

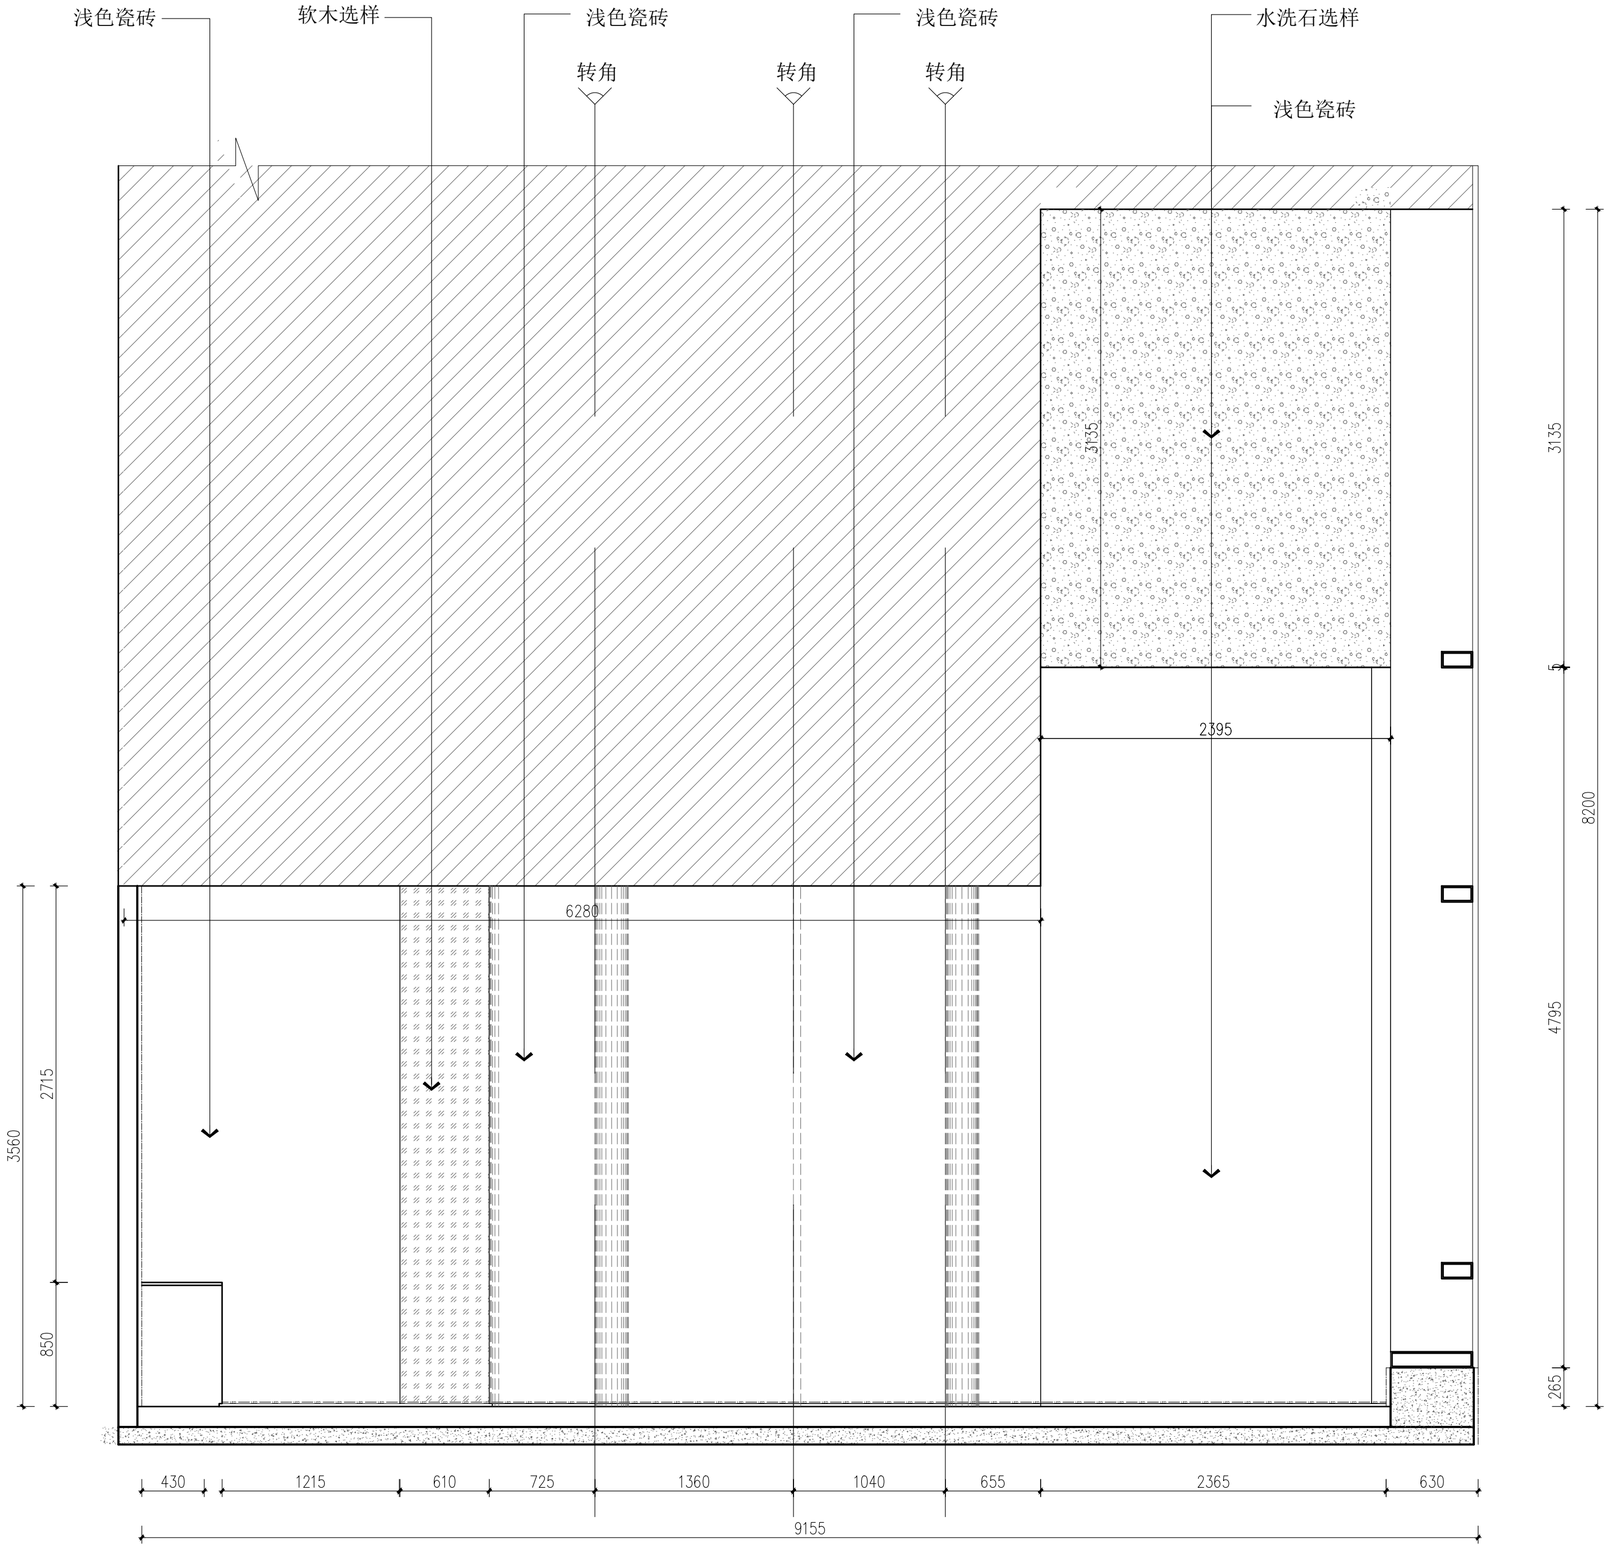

会签 | 建筑 | 电气 | 结构 | 暖通 | 给排水 | 动力

ESSENZA ARMONIOSA
architecture interiors

中国 杭州
TEL: 180 6796 1470
FAX: 180 6796 1470

图注：Exegesis

建设单位 Construction unit

设计单位 Engineering design company

顾问单位 Consultant unit

工程名称 project name

FIONA SHANGHAI

审 定		
审 核		
校 对		
项目负责人		
设 计		
制 图		

图 名

立面图

图 号	EL-12
比 例	
日 期	2026.08
专 业	装饰
设计阶段	施工图
版本编号	
设计编号	


出 图 盖 章

此设计图则之版权归杭州光几建筑室内设计有限公司所有 非得建筑师或设计师之书面批准 不得随意将任何部分翻印 切勿以比例量度此图 一切依图内数字所示为准承建人必须在工场核对图内所示数字之准则如发现有任何矛盾处应立即通知建筑师或设计师

ALL DESIGNS ARE THE SOLE PROPERTY OF HANGZHOU + LTD. AND CANNOT BE USED WITHOUT WRITTEN PERMISSION.DO NOT SCALE DRAWING FIGURED DIMENSIONS ARE TO BE FOLLOWED ALL MEASUREMENTS MUST BE CHECKED ON SITE BY THE CONTRACTOR ANYDISCREPANCIES SHOULD BE REPORTED TO THE ARCHITECT OR DESIGNER

A3-420*297

备注：室外品牌logo制作前，需要现场进行复尺，按照现场尺度制作，该图尺寸仅作参考

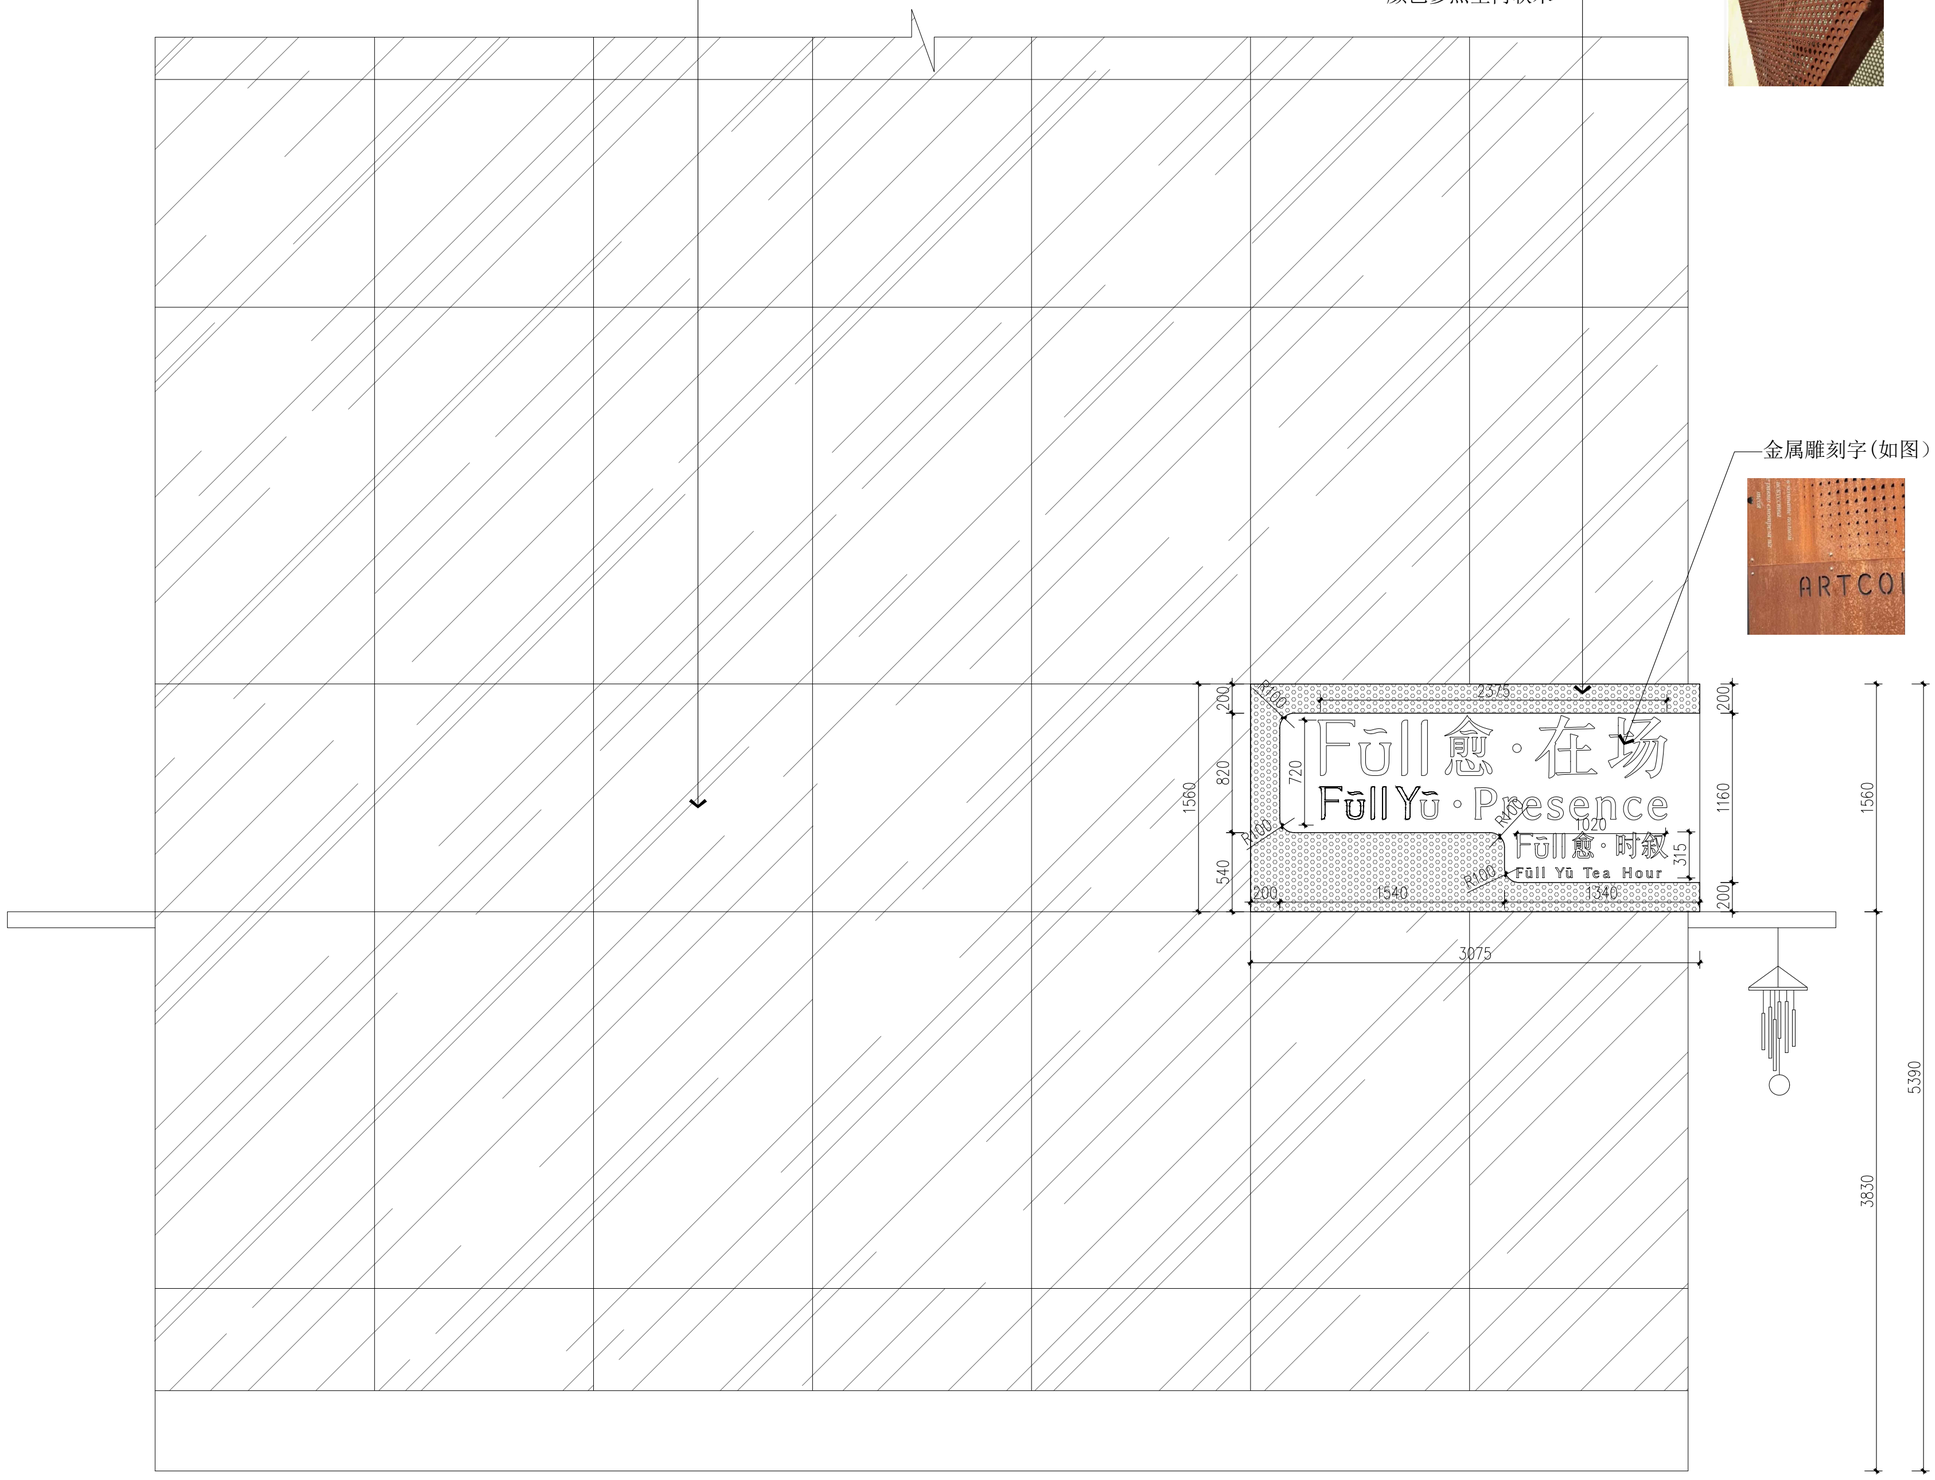

会签 | 建筑 电气 | 结构 暖通 | 给排水 动力

ESSENZA ARMONIOSA
architecture interiors

中国 杭州
TEL: 180 6796 1470
FAX: 180 6796 1470

图注：Exegesis

建设单位 Construction unit

设计单位 Engineering design company

顾问单位 Consultant unit

工程名称 project name

FIONA SHANGHAI

审 定		
审 核		
校 对		
项目负责人		
设 计		
制 图		

图 名

立面图

图 号	EL-13
比 例	1:40
日 期	2026.08
专 业	装饰
设计阶段	施工图
版本编号	
设计编号	


出 图 盖 章

此设计图则之版权归杭州光几建筑室内设计有限公司所有 非得建筑师或设计师之书面批准 不得随意将任何部分翻印 切勿以比例量度此图 一切依图内数字所示为准承建人必须在工场核对图内所示数字之准则如发现有任何矛盾处应立即通知建筑师或设计师

ALL DESIGNS ARE THE SOLE PROPERTY OF HANGZHOU , LTD. AND CANNOT BE USED WITHOUT WRITTEN PERMISSION.DO NOT SCALE DRAWING FIGURED DIMENSIONS ARE TO BE FOLLOWED. ALL MEASUREMENTS MUST BE CHECKED ON SITE BY THE CONTRACTOR. ANYDISCREPANCIES SHOULD BE REPORTED TO THE ARCHITECT OR DESIGNER.

A3-420*297

会签 | 建筑 | 电气 | 结构 | 暖通 | 给排水 | 动力

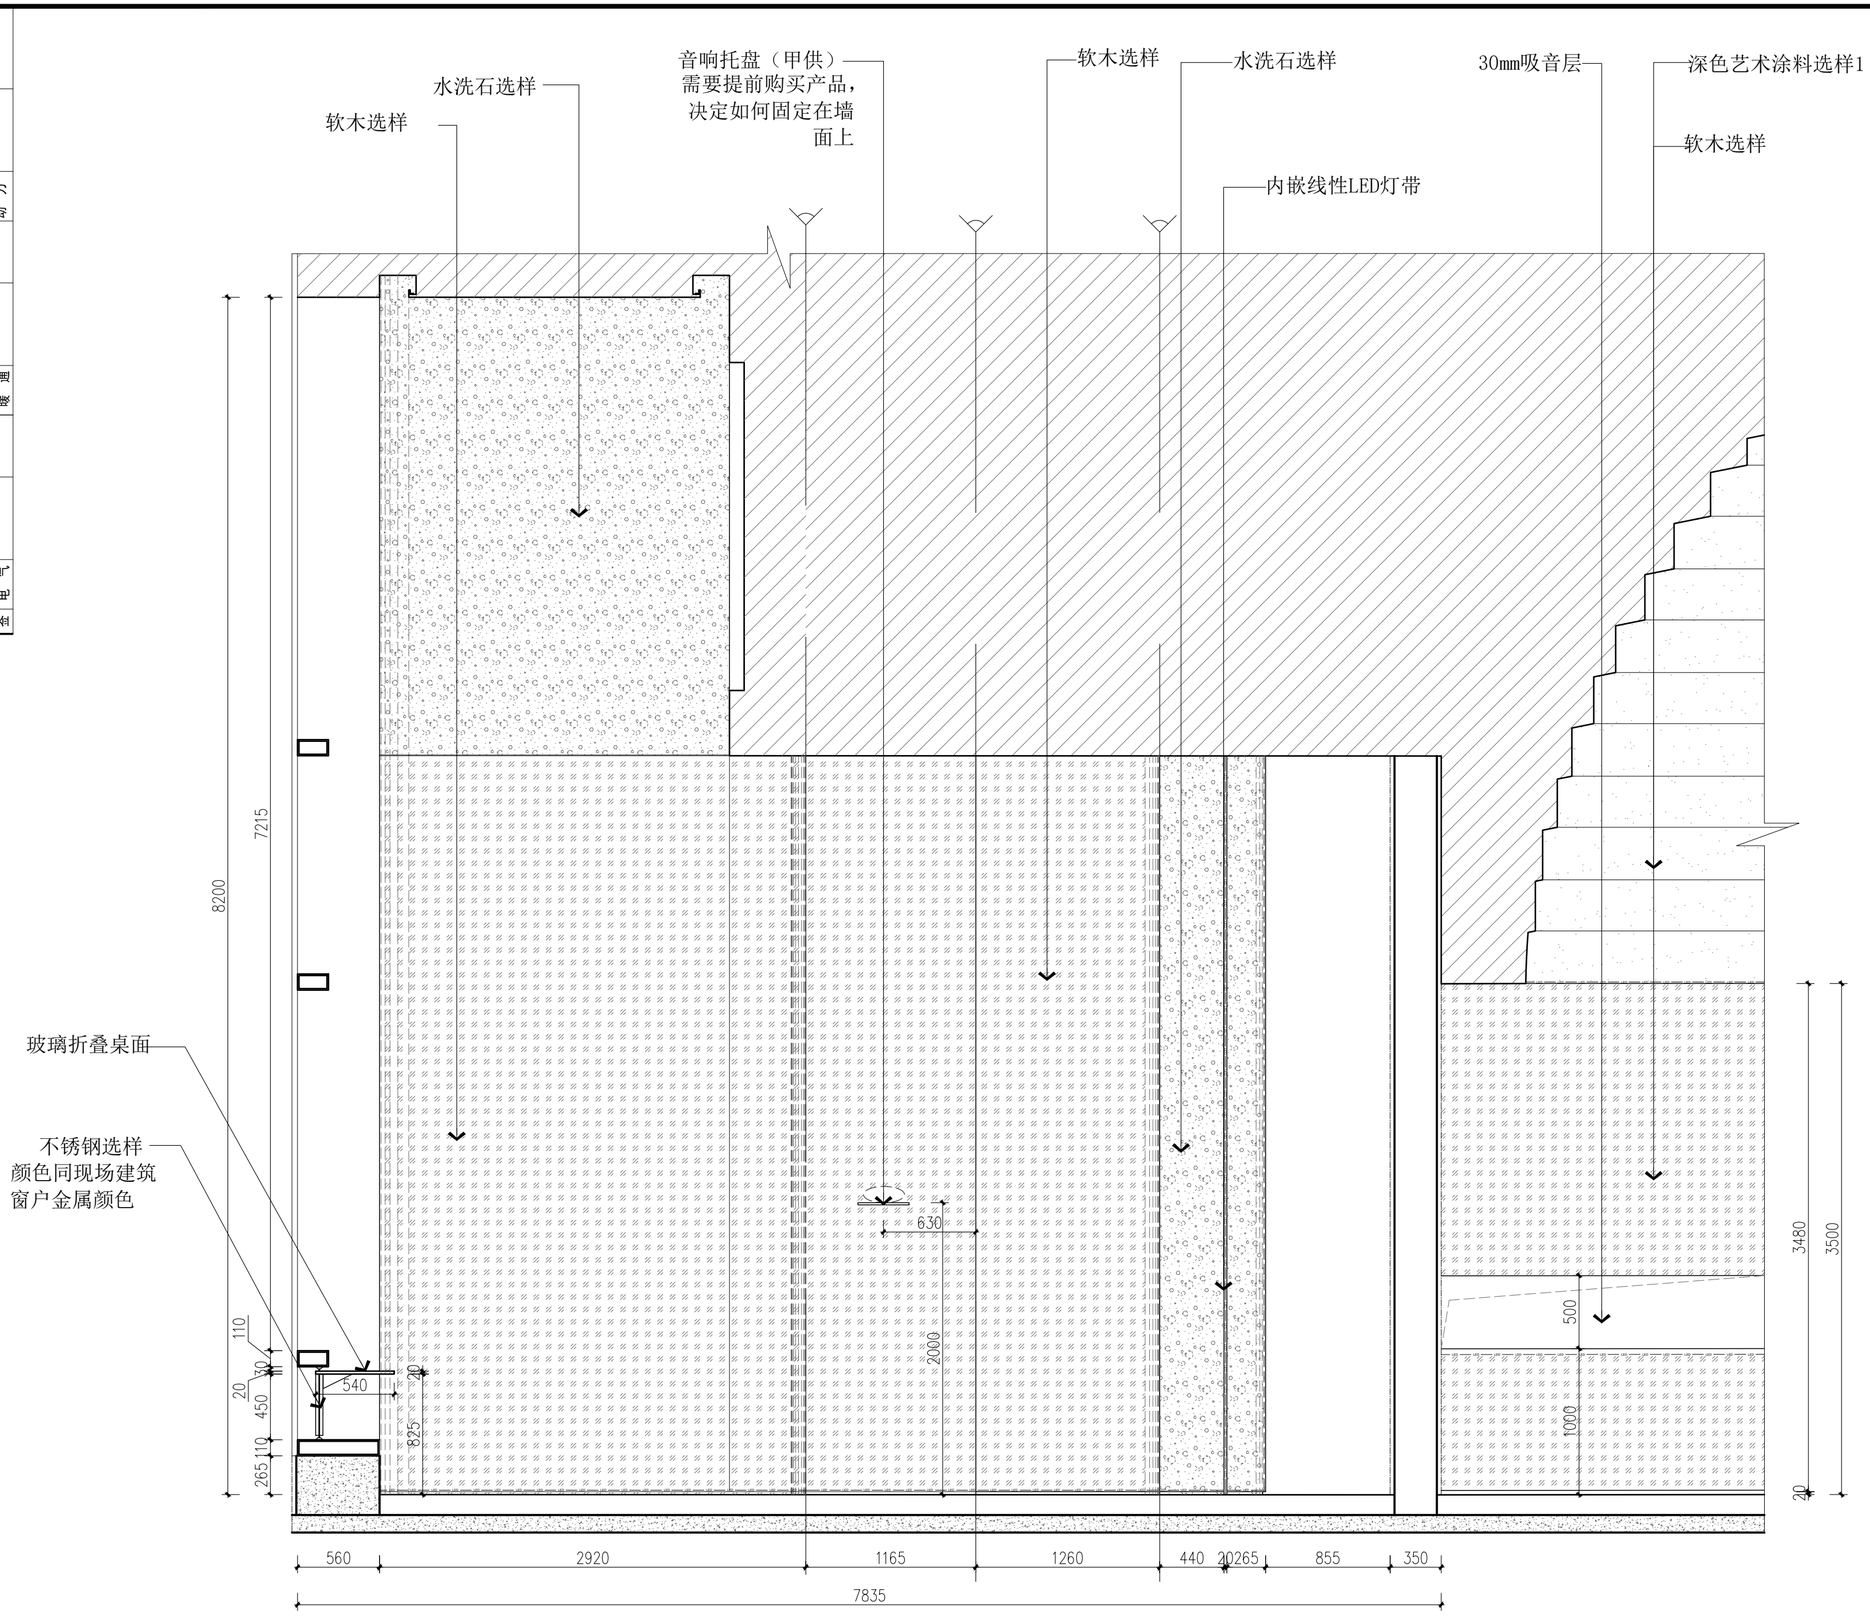

16 ELEVATION 立面图 SCALE:1/40

ESSENZA ARMONIOSA
architecture
interiors

中国 杭州
TEL: 180 6796 1470
FAX: 180 6796 1470

图注: Exegesis

建设单位 Construction unit

设计单位 Engineering design company

顾问单位 Consultant unit

工程名称 project name

FIONA SHANGHAI

审 定		
审 核		
校 对		
项目负责人		
设 计		
制 图		

图 名

立面图

图 号	EL-14
比 例	1:40
日 期	2026.08
专 业	装饰
设计阶段	施工图
版本编号	
设计编号	


出 图 盖 章

此设计图则之版权归杭州光几建筑室内设计有限公司所有 非得建筑师或设计师之书面批准 不得随意将任何部分翻印 切勿以比例量度此图 一切依图内数字所示为准承建人必须在工场核对图内所示数字之准则如发现有任何矛盾处应立即通知建筑师或设计师

ALL DESIGNS ARE THE SOLE PROPERTY OF HANGZHOU , LTD. AND CANNOT BE USED WITHOUT WRITTEN PERMISSION.DO NOT SCALE DRAWING FIGURED DIMENSIONS ARE TO BE FOLLOWED. ALL MEASUREMENTS MUST BE CHECKED ON SITE BY THE CONTRACTOR. ANYDISCREPANCIES SHOULD BE REPORTED TO THE ARCHITECT OR DESIGNER.

A3-420*297

备注：所有大样图需要专业厂家深化，吧台上下设备开洞尺寸，需确认购买设备以后，根据设备具体尺寸去开口

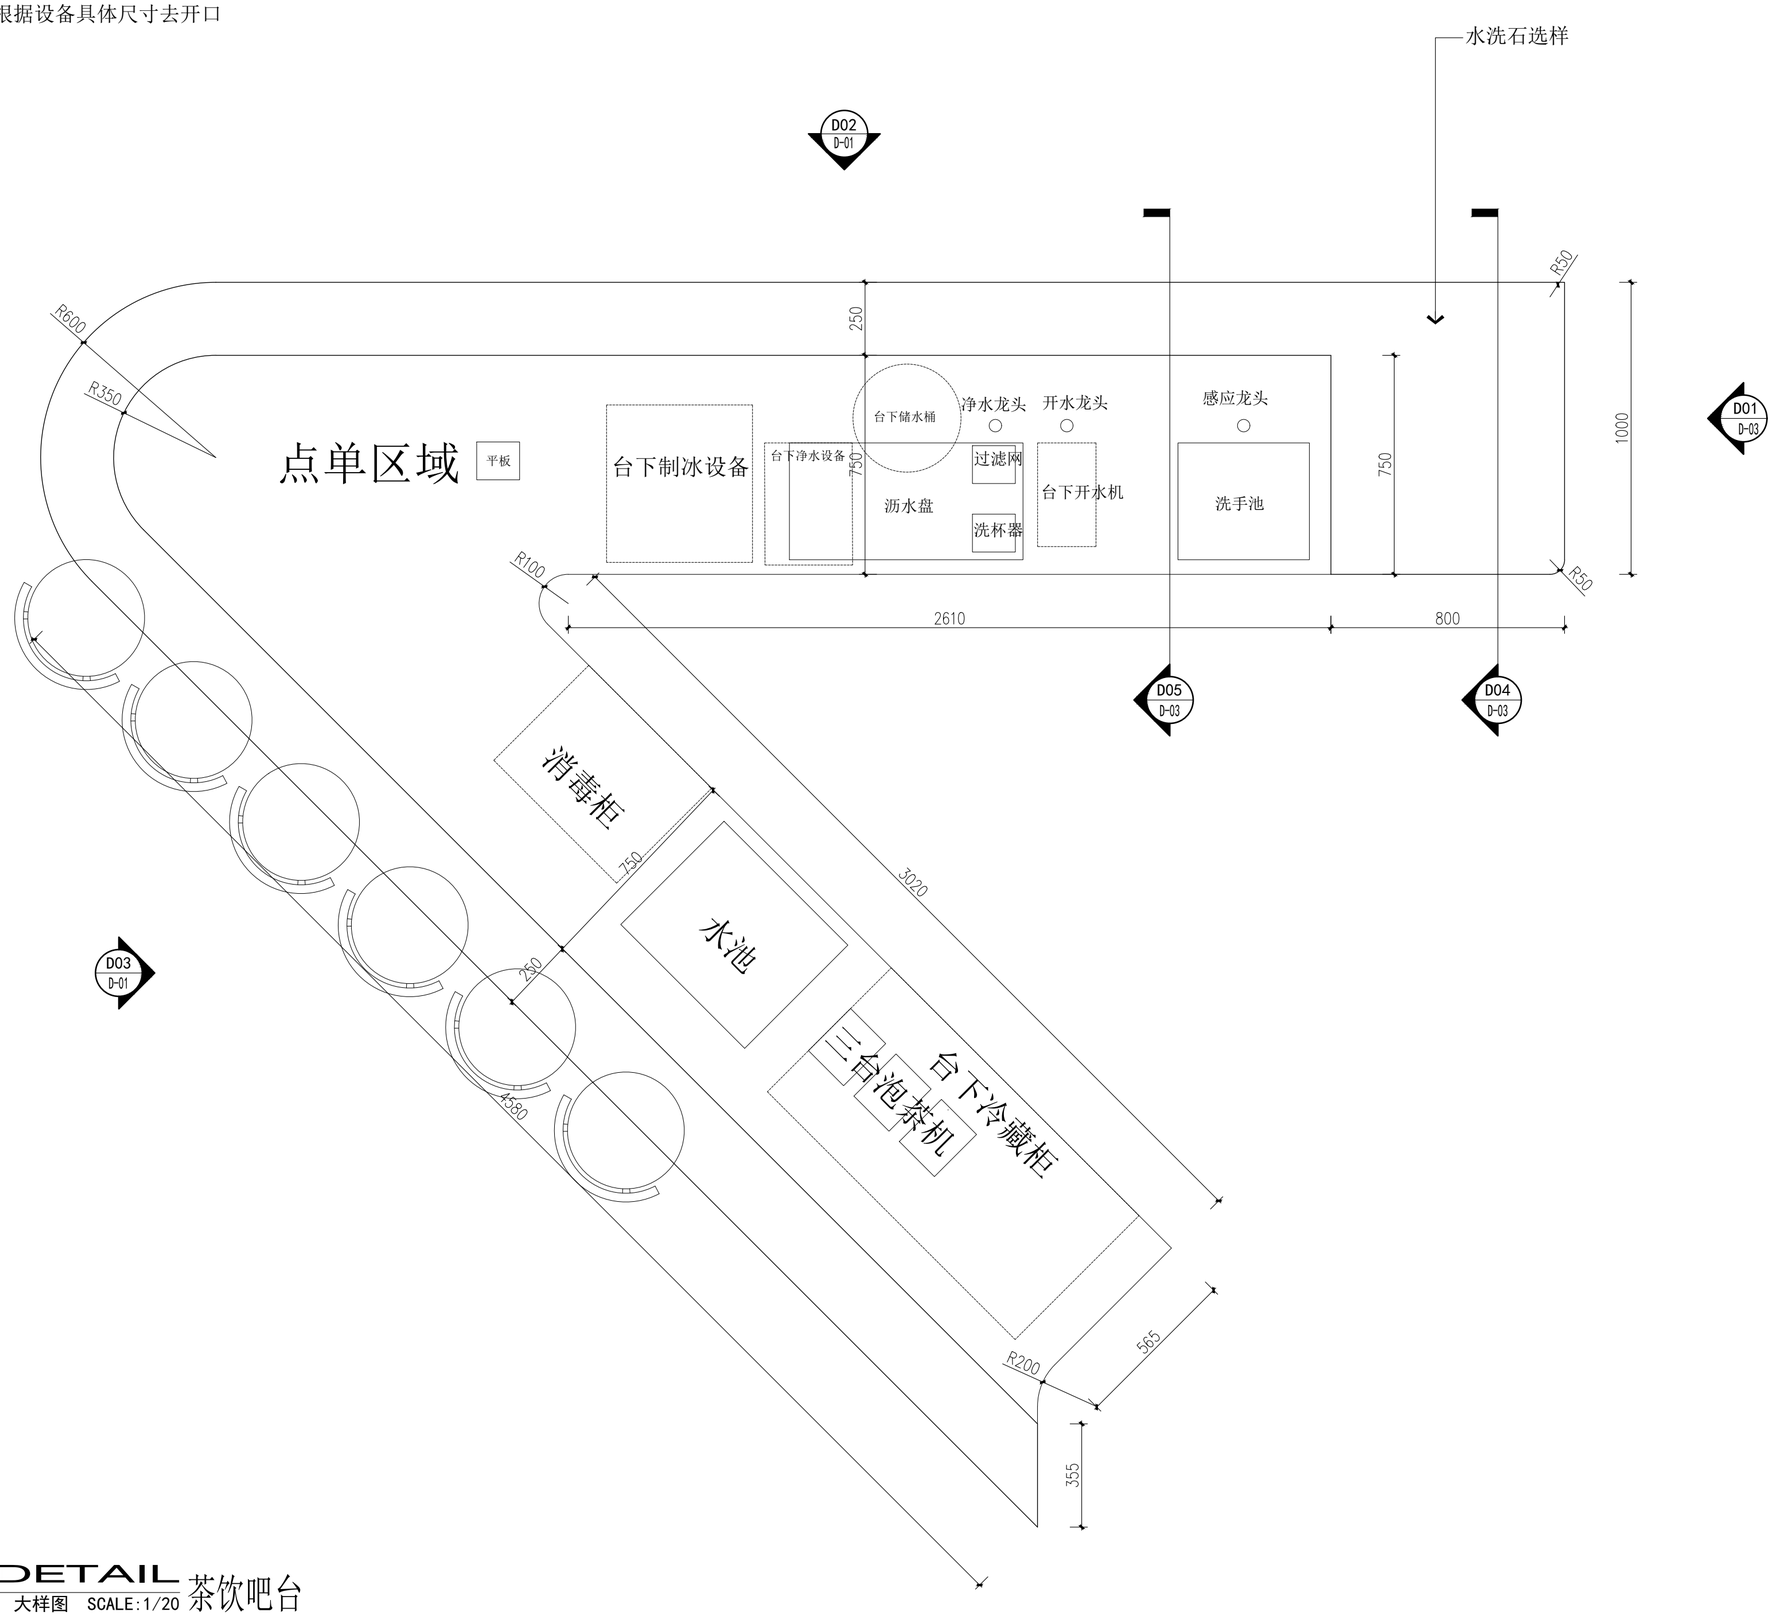

D01 DETAIL 茶饮吧台
大样图 SCALE:1/20

会签	建筑	电气
	结构	暖通
	给排水	动力

ESSENZA ARMONIOSA
architecture
interiors

中国 杭州
TEL: 180 6796 1470
FAX: 180 6796 1470

图注：Exegesis

建设单位 Construction unit

设计单位 Engineering design company

顾问单位 Consultant unit

工程名称 project name

FIONA SHANGHAI

审 定		
审 核		
校 对		
项目负责人		
设 计		
制 图		

图 名
大样图


图 号	D-01
比 例	1:20
日 期	2026.08
专 业	装饰
设计阶段	施工图
版本编号	
设计编号	

出 图 盖 章

此设计图则之版权归杭州光几建筑室内设计有限公司所有 非得建筑师或设计师之书面批准 不得随意将任何部分翻印 切勿以比例量度此图 一切依图内数字所示为准承建人必须在工场核对图内所示数字之准则如发现有任何矛盾处应立即通知建筑师或设计师

ALL DESIGNS ARE THE SOLE PROPERTY OF HANGZHOU , LTD. AND CANNOT BE USED WITHOUT WRITTEN PERMISSION.DO NOT SCALE DRAWING FIGURED DIMENSIONS ARE TO BE FOLLOWED ALL MEASUREMENTS MUST BE CHECKED ON SITE BY THE CONTRACTOR ANYDISCREPANCIES SHOULD BE REPORTED TO THE ARCHITECT OR DESIGNER


A3-420*297

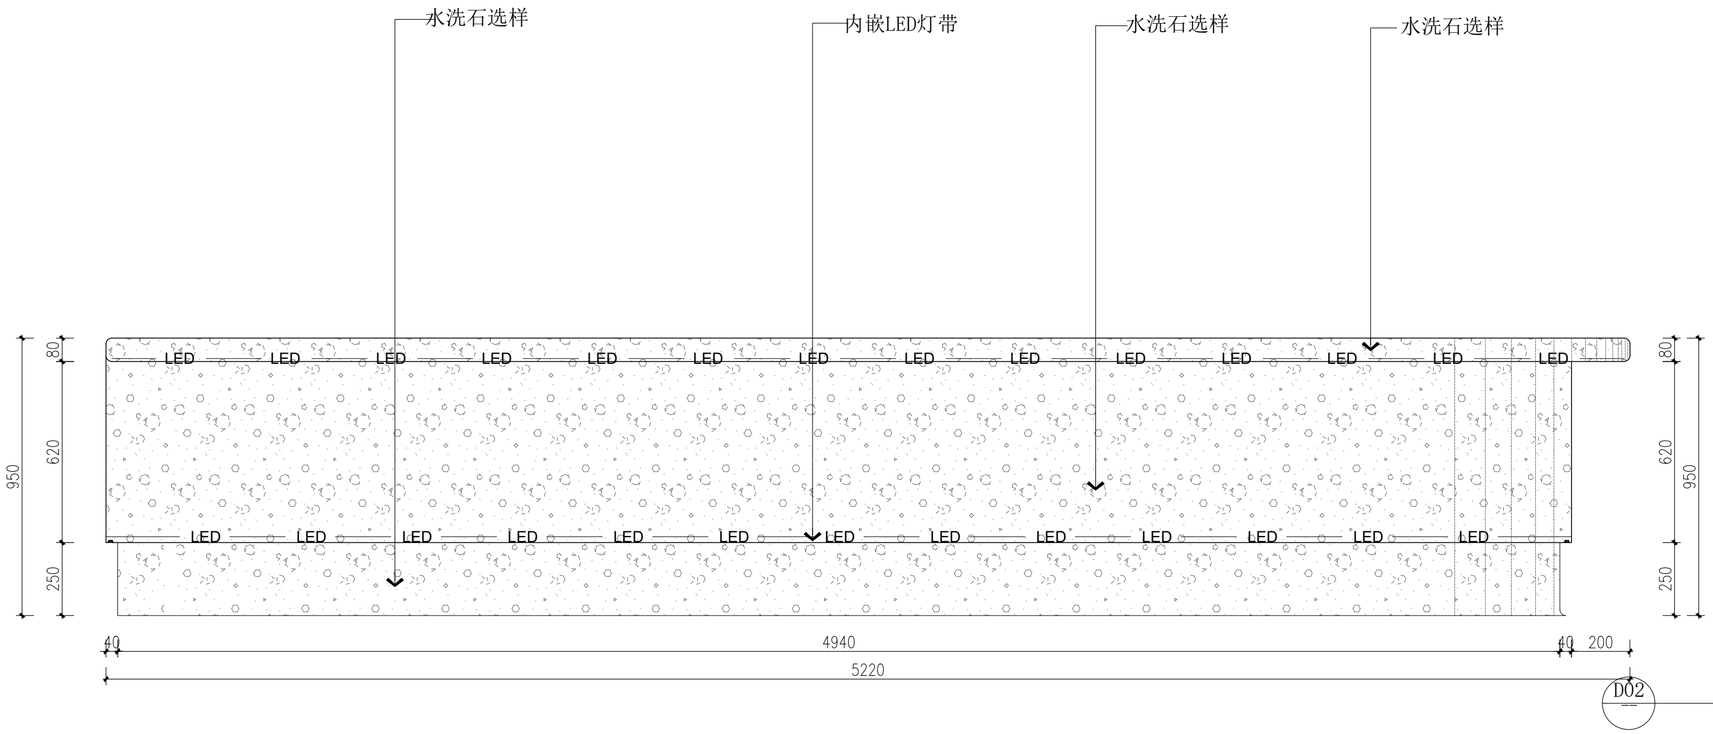

D02

DETAIL

大样图 SCALE:1/20

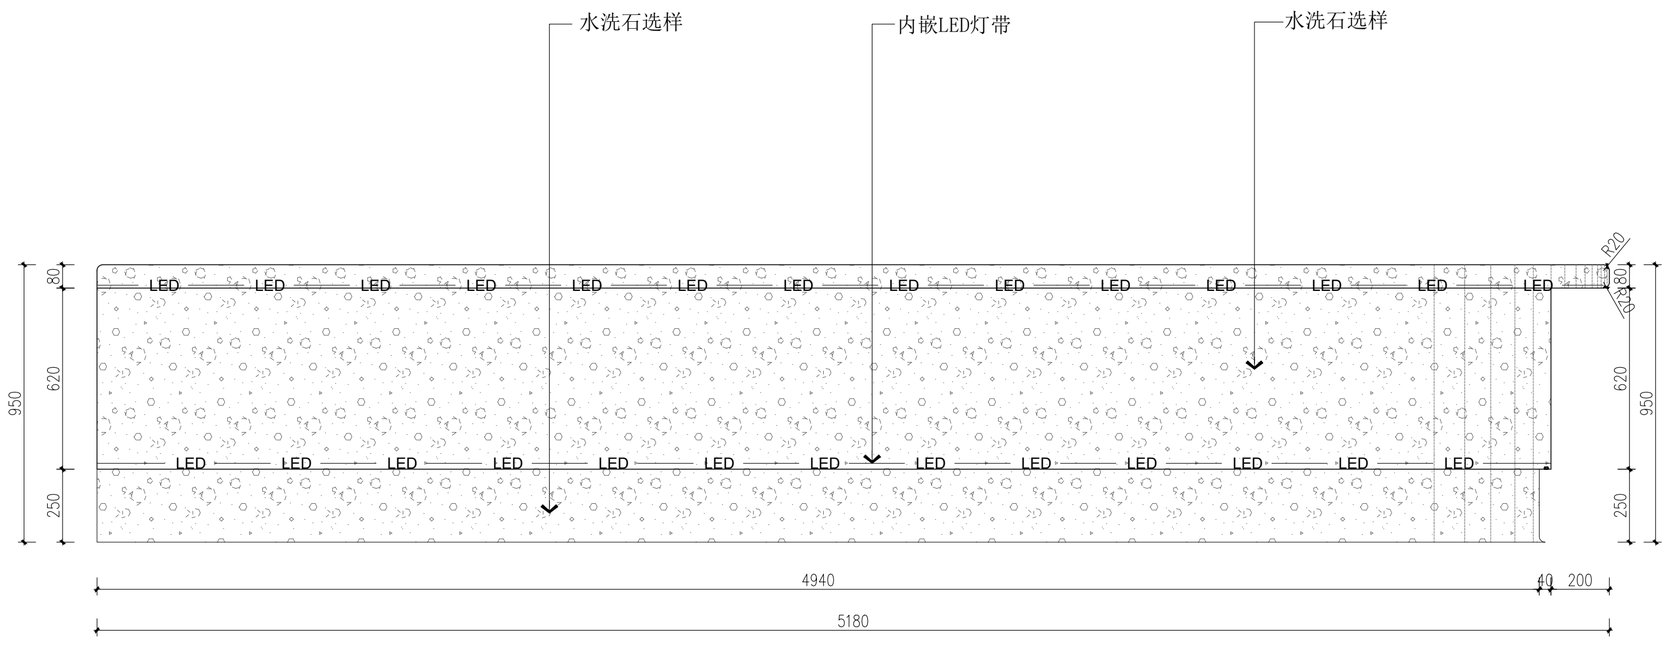

D03

DETAIL

大样图 SCALE:1/20

会签 | 建筑 | 电气 | 结构 | 暖通 | 给排水 | 动力

ESSENZA ARMONIOSA

architecture interiors

中国 杭州
TEL: 180 6796 1470
FAX: 180 6796 1470

图注: Exegesis

建设单位 Construction unit

设计单位 Engineering design company

顾问单位 Consultant unit

工程名称 project name

FIONA SHANGHAI

审 定		
审 核		
校 对		
项目负责人		
设 计		
制 图		

图 名

大样图

图 号	D-02
比 例	1:20
日 期	2026.08
专 业	装饰
设计阶段	施工图
版本编号	
设计编号	


出 图 盖 章

此设计图则之版权归杭州光几建筑室内设计有限公司所有 非得建筑师或设计师之书面批准 不得随意将任何部分翻印 切勿以比例量度此图 一切依图内数字所示为准承建人必须在工场核对图内所示数字之准则如发现有任何矛盾处应立即通知建筑师或设计师


ALL DESIGNS ARE THE SOLE PROPERTY OF HANGZHOU , LTD. AND CANNOT BE USED WITHOUT WRITTEN PERMISSION.DO NOT SCALE DRAWING. FIGURED DIMENSIONS ARE TO BE FOLLOWED. ALL MEASUREMENTS MUST BE CHECKED ON SITE BY THE CONTRACTOR. ANYDISCREPANCIES SHOULD BE REPORTED TO THE ARCHITECT OR DESIGNER.

A3-420*297


会签 | 建筑 | 电气 | 结构 | 暖通 | 给排水 | 动力

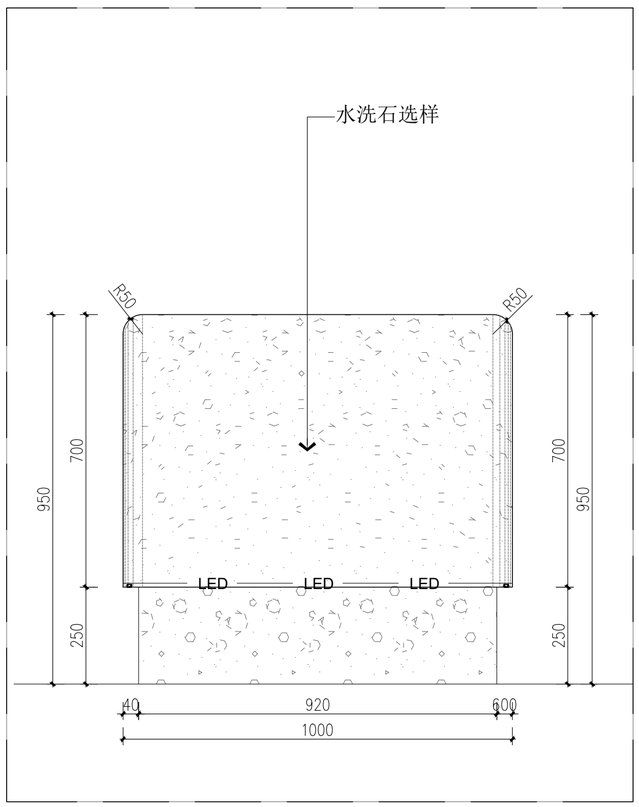

D01 DETAIL
大样图 SCALE:1/15

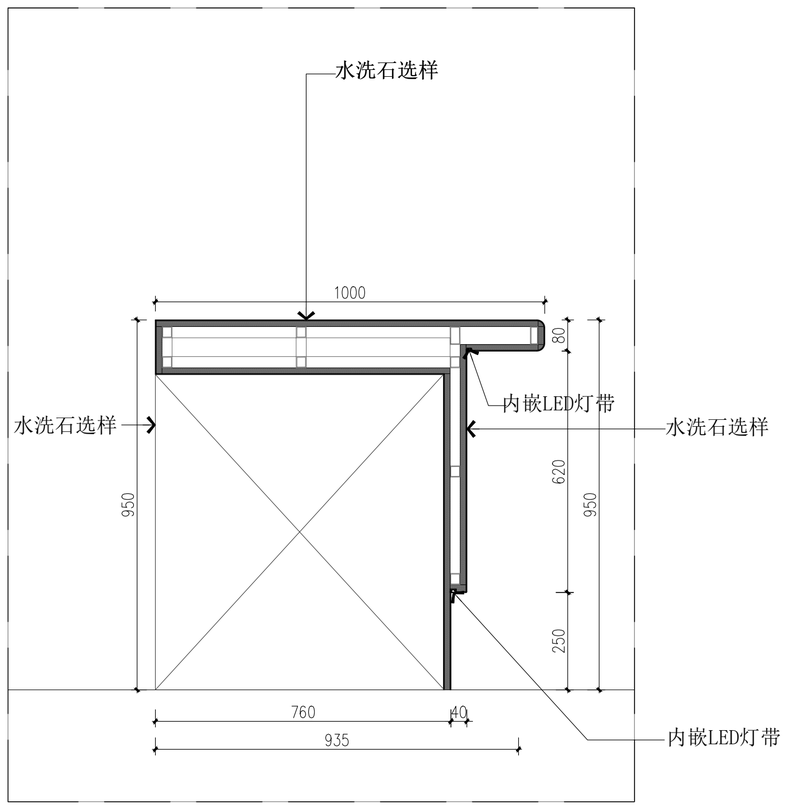

D04 DETAIL
大样图 SCALE:1/15

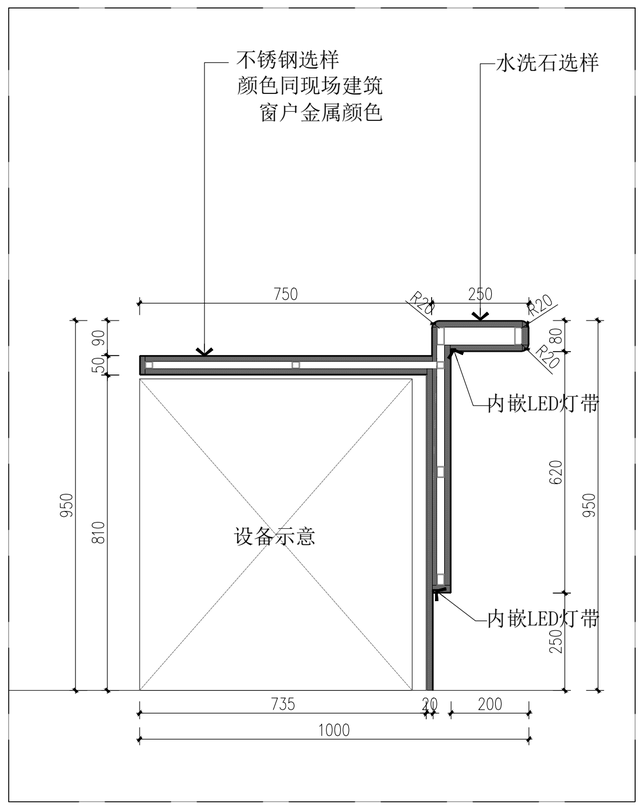

D05 DETAIL
大样图 SCALE:1/15

ESSENZA ARMONIOSA
architecture
interiors

中国 杭州
TEL: 180 6796 1470
FAX: 180 6796 1470

图注: Exegesis

建设单位 Construction unit

设计单位 Engineering design company

顾问单位 Consultant unit

工程名称 project name

FIONA SHANGHAI

审 定		
审 核		
校 对		
项目负责人		
设 计		
制 图		

图 名

大样图


图 号	D-03
比 例	
日 期	2026.08
专 业	装饰
设计阶段	施工图
版本编号	
设计编号	

出 图 盖 章


此设计图则之版权归杭州光几建筑室内设计有限公司所有 非得建筑师或设计师之书面批准 不得随意将任何部分翻印 切勿以比例量度此图 一切依图内数字所示为准承建人必须在工场核对图内所示数字之准则如发现有任何矛盾处应立即通知建筑师或设计师

ALL DESIGNS ARE THE SOLE PROPERTY OF HANGZHOU , LTD. AND CANNOT BE USED WITHOUT WRITTEN PERMISSION.DO NOT SCALE DRAWING FIGURED DIMENSIONS ARE TO BE FOLLOWED. ALL MEASUREMENTS MUST BE CHECKED ON SITE BY THE CONTRACTOR. ANYDISCREPANCIES SHOULD BE REPORTED TO THE ARCHITECT OR DESIGNER.


A3-420*297

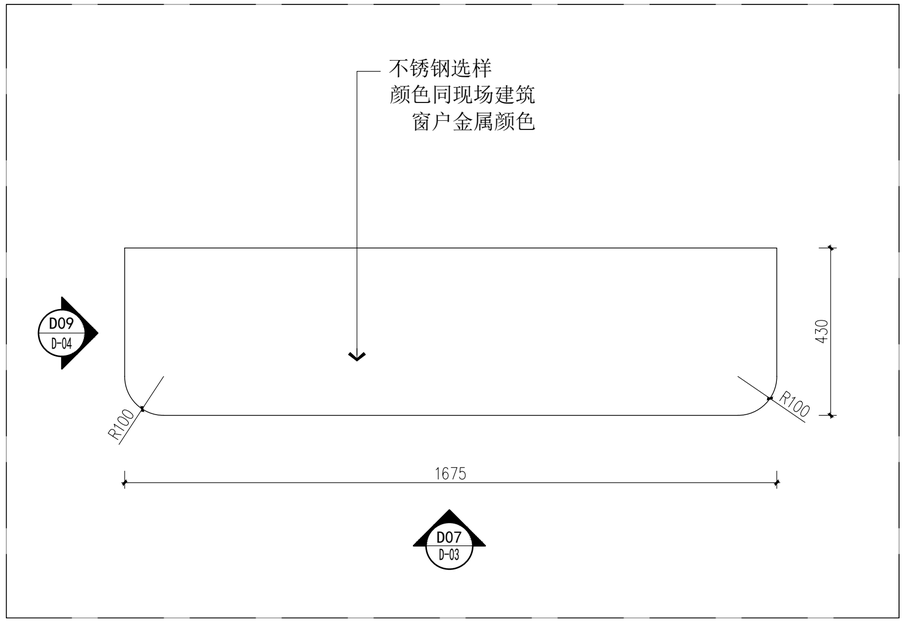


D06 DETAIL 大样图 SCALE:1/15 产品柜1

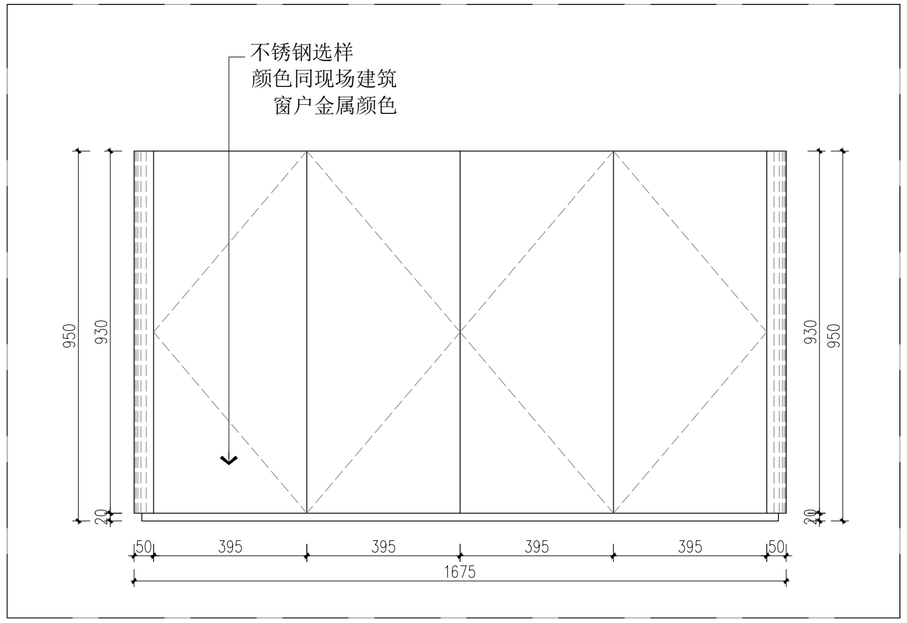


D07 DETAIL 大样图 SCALE:1/15 有柜门

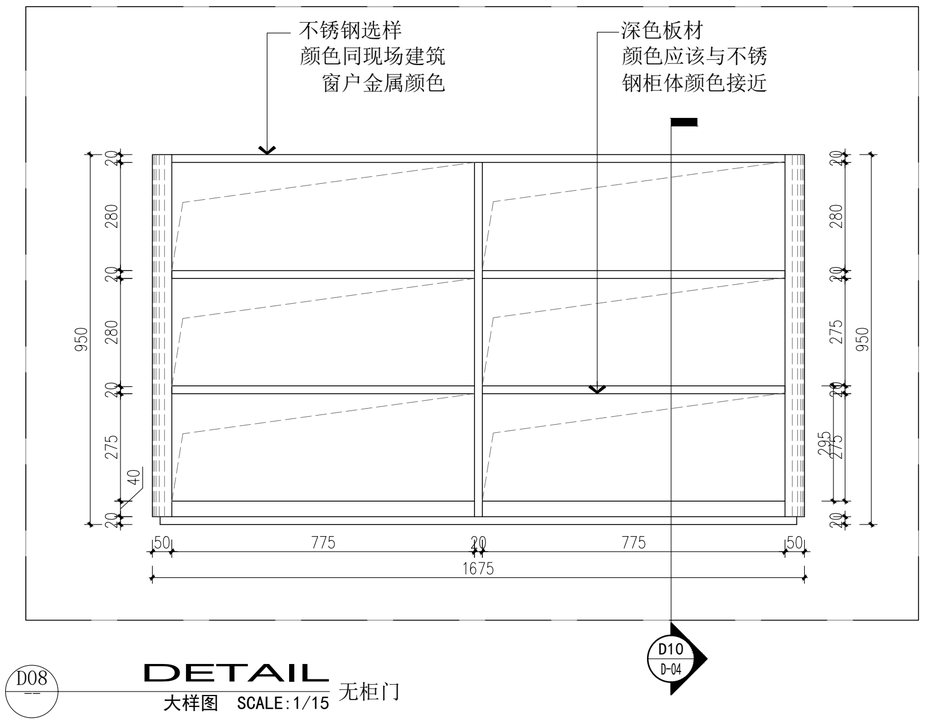

D08 DETAIL 大样图 SCALE:1/15 无柜门

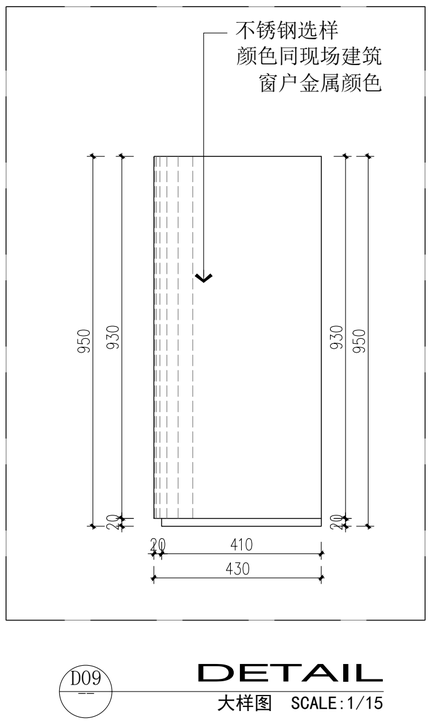

D09 DETAIL 大样图 SCALE:1/15

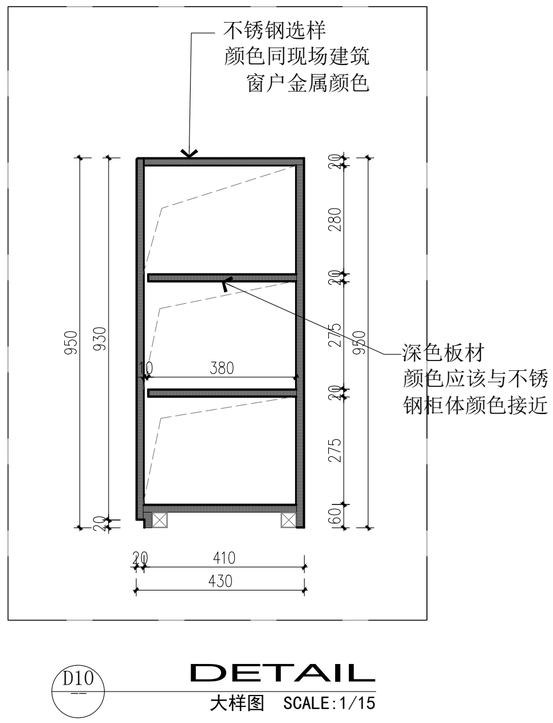

D10 DETAIL 大样图 SCALE:1/15

ESSENZA ARMONIOSA
architecture
interiors

中国 杭州
TEL: 180 6796 1470
FAX: 180 6796 1470

图注: Exegesis

建设单位 Construction unit

设计单位 Engineering design company

顾问单位 Consultant unit

工程名称 project name

FIONA SHANGHAI

审 定		
审 核		
校 对		
项目负责人		
设 计		
制 图		


图 名 大样图

图 号	D-04
比 例	1:15
日 期	2026.08
专 业	装饰
设计阶段	施工图
版本编号	
设计编号	


出 图 盖 章

此设计图则之版权归杭州光几建筑室内设计有限公司所有 非得建筑师或设计师之书面批准 不得随意将任何部分翻印 切勿以比例量度此图 一切依图内数字所示为准承建人必须在工场核对图内所示数字之准则如发现有任何矛盾处应立即通知建筑师或设计师


ALL DESIGNS ARE THE SOLE PROPERTY OF HANGZHOU , LTD. AND CANNOT BE USED WITHOUT WRITTEN PERMISSION.DO NOT SCALE DRAWING. FIGURED DIMENSIONS ARE TO BE FOLLOWED. ALL MEASUREMENTS MUST BE CHECKED ON SITE BY THE CONTRACTOR AND/DISCREPANCIES SHOULD BE REPORTED TO THE ARCHITECT OR DESIGNER.

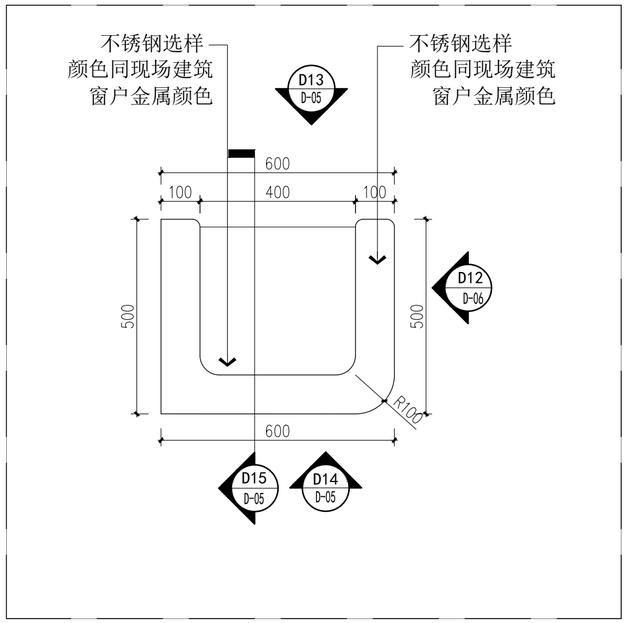


D11 DETAIL 接待台
大样图 SCALE:1/15

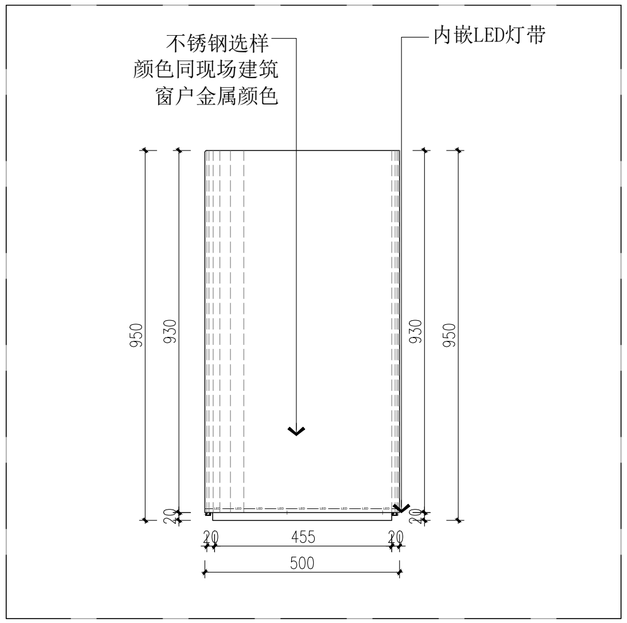


D12 DETAIL
大样图 SCALE:1/15

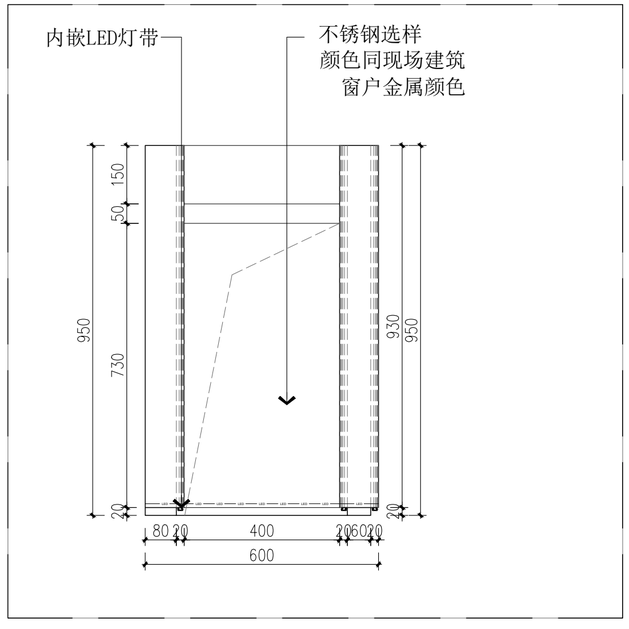

D13 DETAIL
大样图 SCALE:1/15

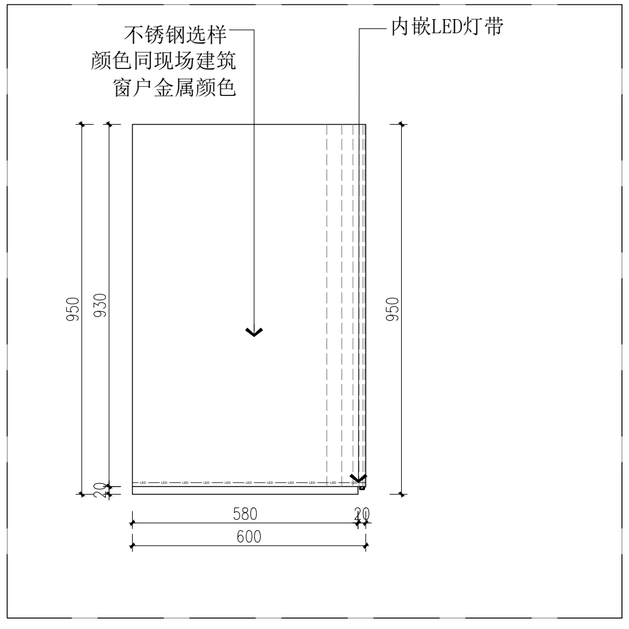

D14 DETAIL
大样图 SCALE:1/15

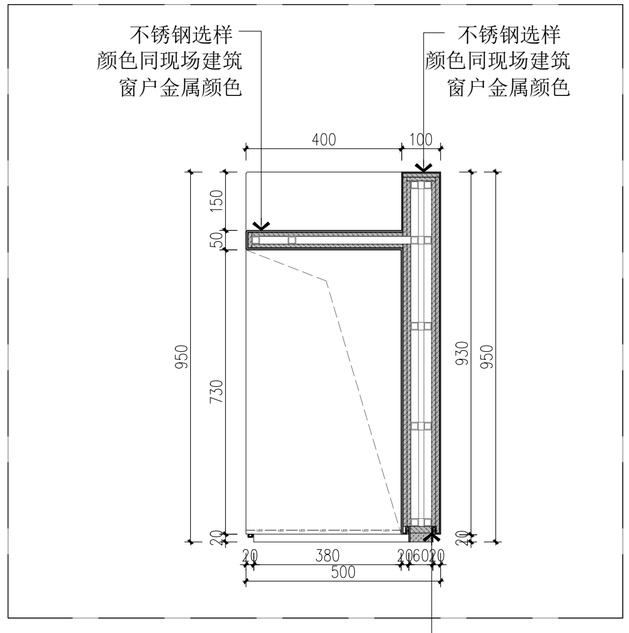

D15 DETAIL
大样图 SCALE:1/15

会签 | 建筑 电气 | 结构 暖通 | 给排水 动力

ESSENZA ARMONIOSA
architecture interiors

中国 杭州
TEL: 180 6796 1470
FAX: 180 6796 1470

图注: Exegesis

建设单位 Construction unit

设计单位 Engineering design company

顾问单位 Consultant unit

工程名称 project name

FIONA SHANGHAI

审 定		
审 核		
校 对		
项目负责人		
设 计		
制 图		

图 名: 大样图


图 号	D-05
比 例	1:15
日 期	2026.08
专 业	装饰
设计阶段	施工图
版本编号	
设计编号	

出 图 盖 章


此设计图则之版权归杭州光几建筑室内设计有限公司所有 非得建筑师或设计师之书面批准 不得随意将任何部分翻印 切勿以比例量度此图 一切依图内数字所示为准承建人必须在工场核对图内所示数字之准则如发现有任何矛盾处应立即通知建筑师或设计师

ALL DESIGNS ARE THE SOLE PROPERTY OF HANGZHOU , LTD, AND CANNOT BE USED WITHOUT WRITTEN PERMISSION.DO NOT SCALE DRAWING. FIGURED DIMENSIONS ARE TO BE FOLLOWED. ALL MEASUREMENTS MUST BE CHECKED ON SITE BY THE CONTRACTOR. ANYDISCREPANCIES SHOULD BE REPORTED TO THE ARCHITECT OR DESIGNER.


A3-420*297

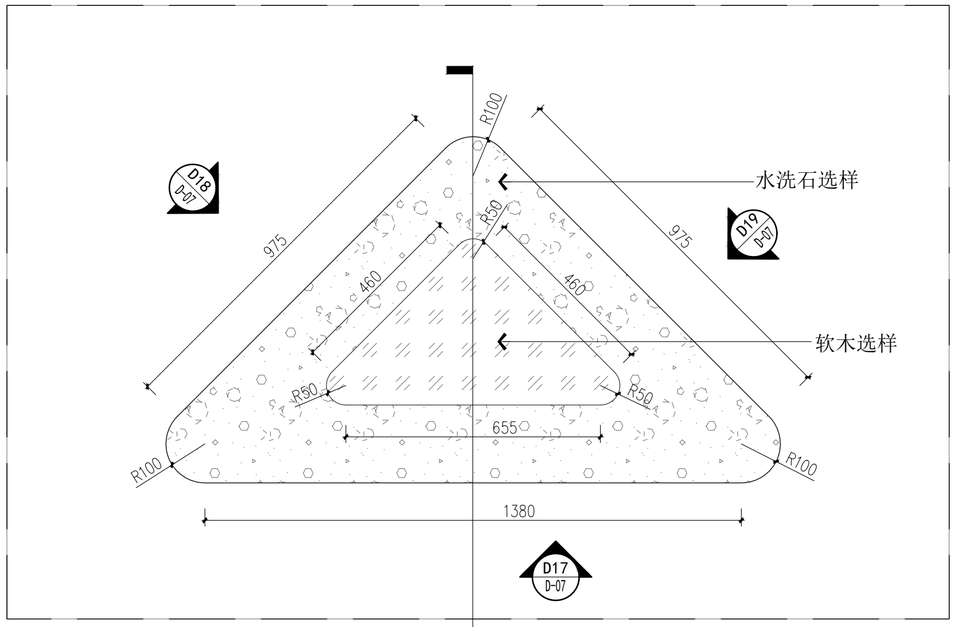


D16 DETAIL 大样图 SCALE:1/15 展示柜 D20 D-07

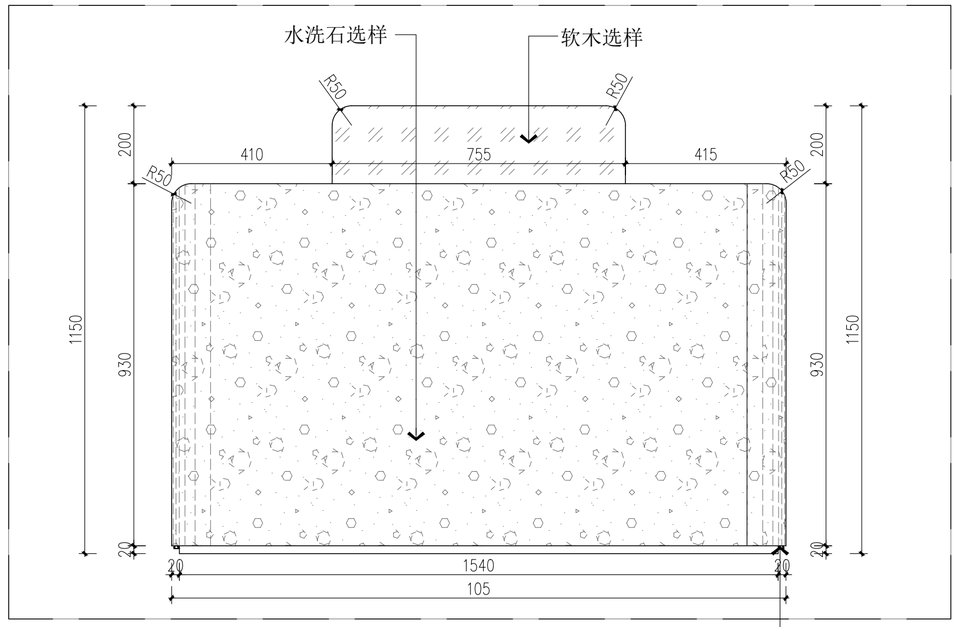


D17 DETAIL 大样图 SCALE:1/15

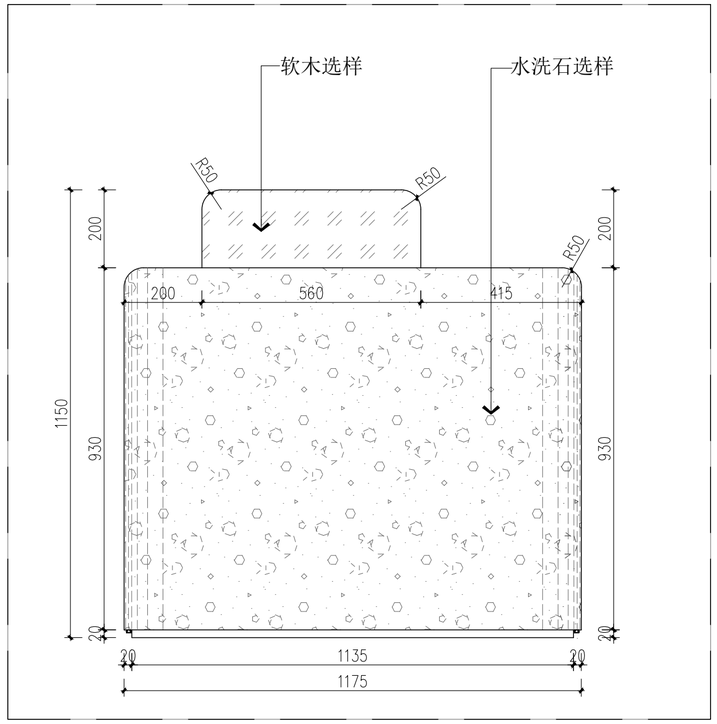

D18 DETAIL 大样图 SCALE:1/15

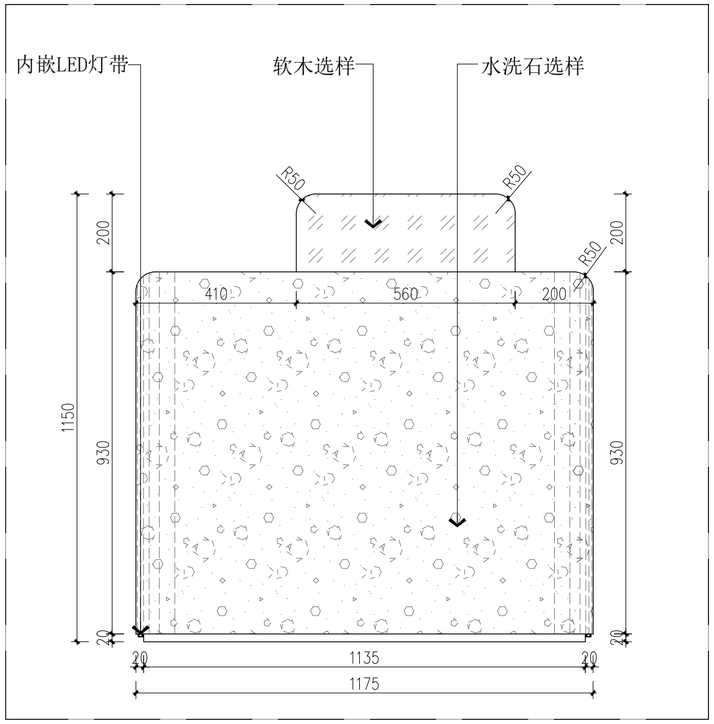

D19 DETAIL 大样图 SCALE:1/15

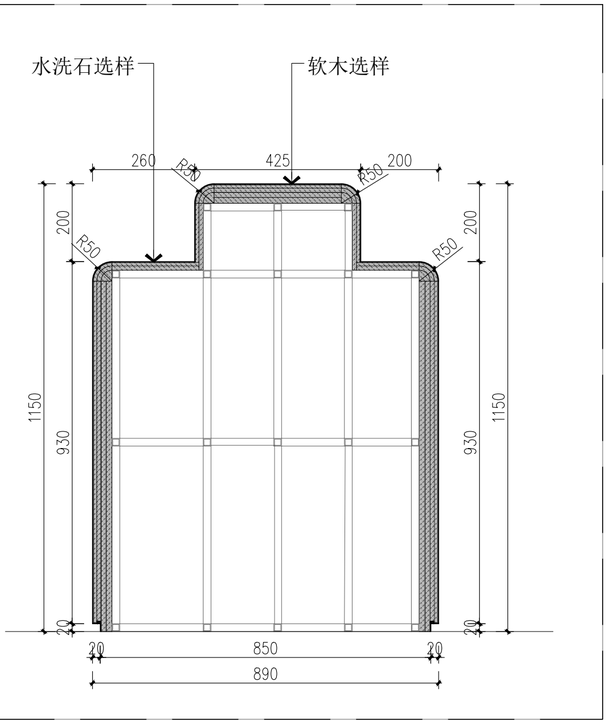

D20 DETAIL 大样图 SCALE:1/15

给排水 动 力
结 构 暖 通
建 筑 电 气
会 签

ESSENZA ARMONIOSA
architecture interiors

中国 杭州
TEL: 180 6796 1470
FAX: 180 6796 1470

图注: Exegesis

建设单位 Construction unit

设计单位 Engineering design company

顾问单位 Consultant unit

工程名称 project name

FIONA SHANGHAI

审 定		
审 核		
校 对		
项目负责人		
设 计		
制 图		

图 名

大样图

图 号	D-06
比 例	1:15
日 期	2026.08
专 业	装饰
设计阶段	施工图
版本编号	
设计编号	


出 图 盖 章

此设计图则之版权归杭州光几建筑室内设计有限公司所有 非得建筑师或设计师之书面批准 不得随意将任何部分翻印 切勿以比例量度此图 一切依图内数字所示为准承建人必须在工场核对图内所示数字之准则如发现有任何矛盾处应立即通知建筑师或设计师

ALL DESIGNS ARE THE SOLE PROPERTY OF HANGZHOU , LTD. AND CANNOT BE USED WITHOUT WRITTEN PERMISSION.DO NOT SCALE DRAWING. FIGURED DIMENSIONS ARE TO BE FOLLOWED. ALL MEASUREMENTS MUST BE CHECKED ON SITE BY THE CONTRACTOR. ANYDISCREPANCIES SHHULD BE REPORTED TO THE ARCHITECT OR DESIGNER.

A3-420*297

给排水 动 力
结 构 暖 通
建 筑 电 气
会 签

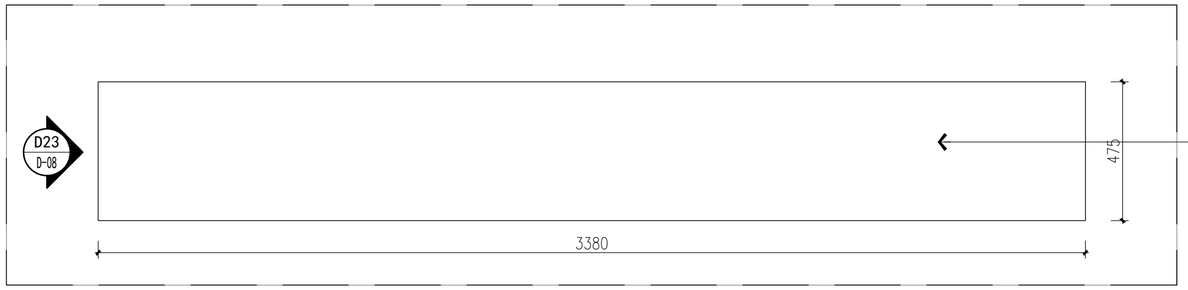


不锈钢选样
颜色同现场建筑
窗户金属颜色




电动伸缩衣架


D21 DETAIL 大样图 SCALE:1/20 储物柜 D22 D-08

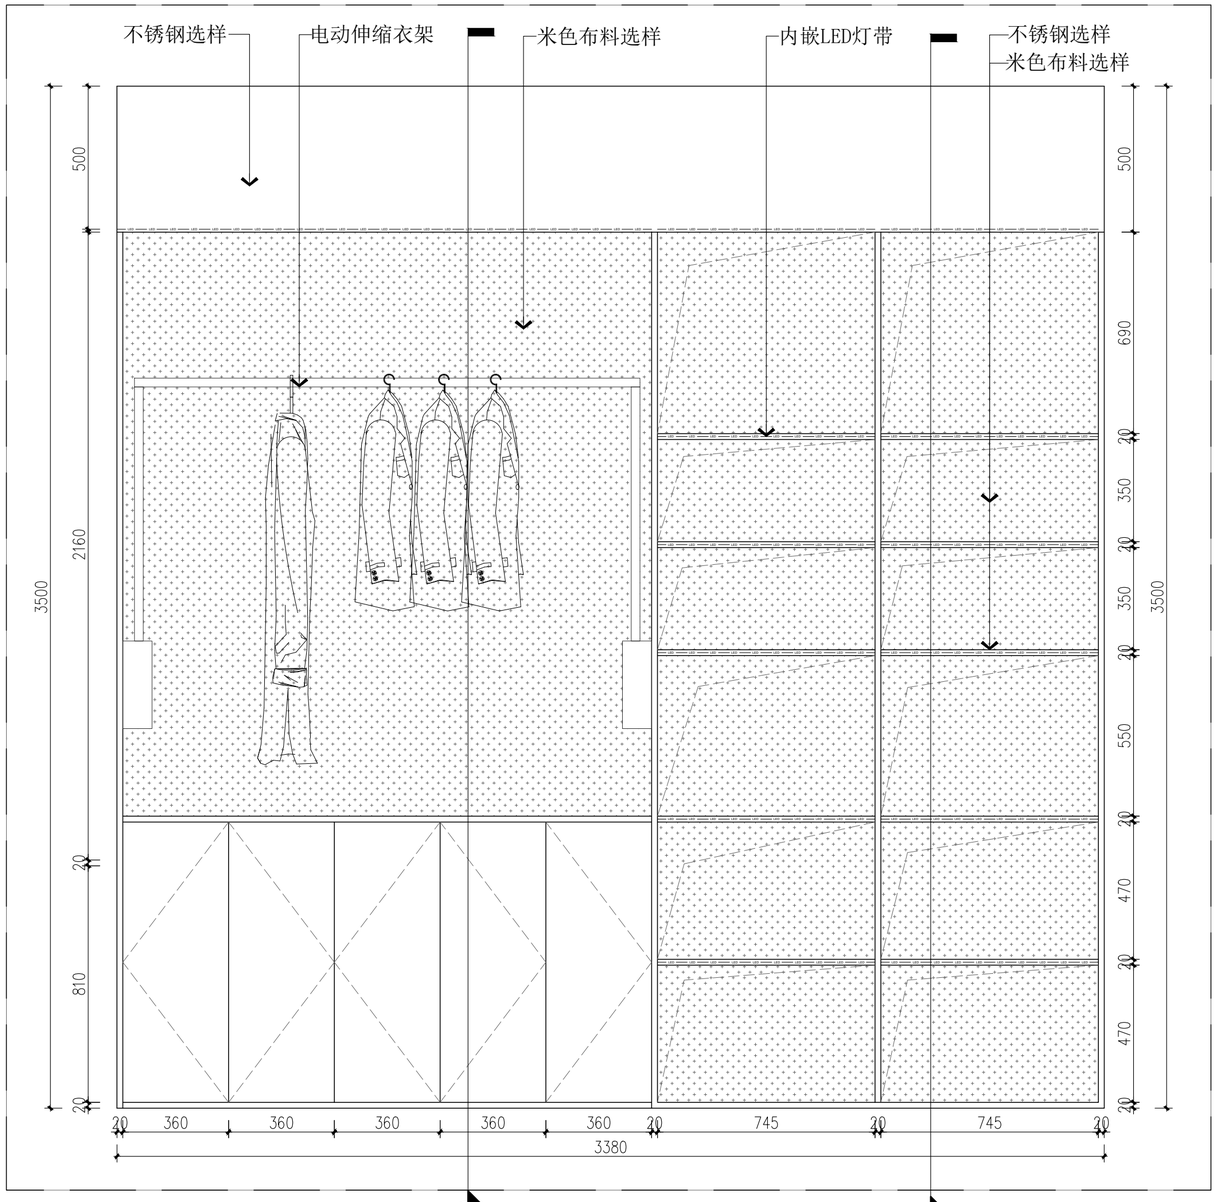


D22 DETAIL 大样图 SCALE:1/20 D24 D-08 D25 D-08

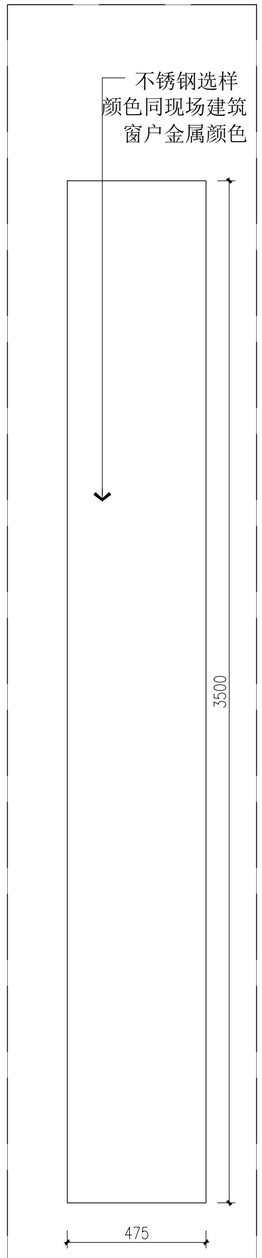

D23 DETAIL 大样图 SCALE:1/20

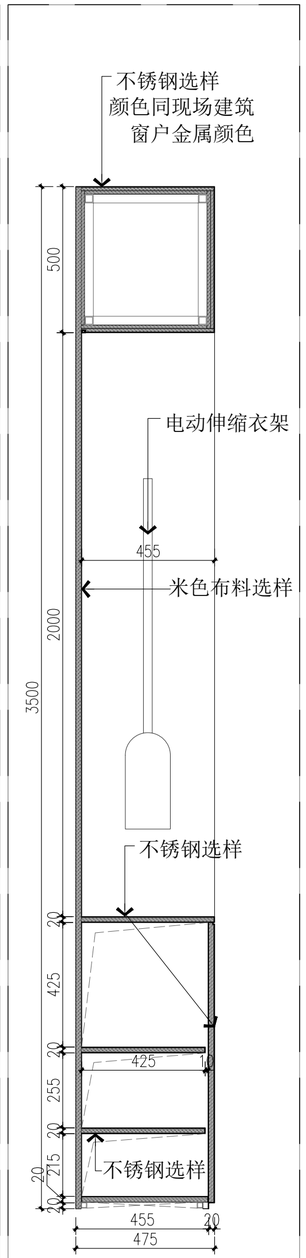

D24 DETAIL 大样图 SCALE:1/20

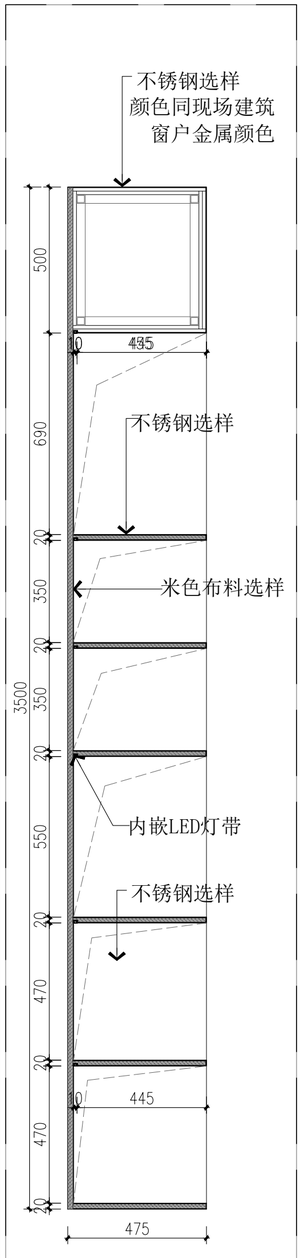

D25 DETAIL 大样图 SCALE:1/20

ESSENZA ARMONIOSA
architecture
interiors

中国 杭州
TEL: 180 6796 1470
FAX: 180 6796 1470

图注: Exegesis

建设单位 Construction unit

设计单位 Engineering design company

顾问单位 Consultant unit

工程名称 project name

FIONA SHANGHAI

审 定		
审 核		
校 对		
项目负责人		
设 计		
制 图		

图 名

大样图


图 号	D-07
比 例	1:20
日 期	2026.08
专 业	装饰
设计阶段	施工图
版本编号	
设计编号	

出 图 盖 章

此设计图则之版权归杭州光几建筑室内设计有限公司所有 非得建筑师或设计师之书面批准 不得随意将任何部分翻印 切勿以比例量度此图 一切依图内数字所示为准承建人必须在工场核对图内所示数字之准则如发现有任何矛盾处应立即通知建筑师或设计师


ALL DESIGNS ARE THE SOLE PROPERTY OF HANGZHOU , LTD. AND CANNOT BE USED WITHOUT WRITTEN PERMISSION.DO NOT SCALE DRAWING FIGURED DIMENSIONS ARE TO BE FOLLOWED. ALL MEASUREMENTS MUST BE CHECKED ON SITE BY THE CONTRACTOR. ANYDISCREPANCIES SHOULD BE REPORTED TO THE ARCHITECT OR DESIGNER.

A3-420*297

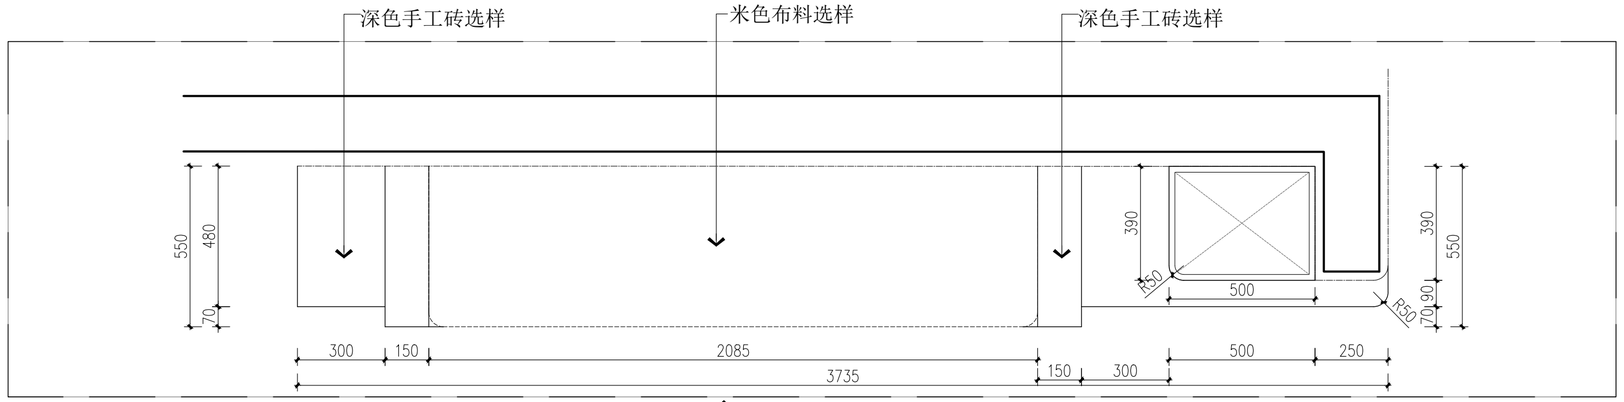

D26 DETAIL 卡座/鞋柜 D27 D-08

大样图 SCALE:1/20

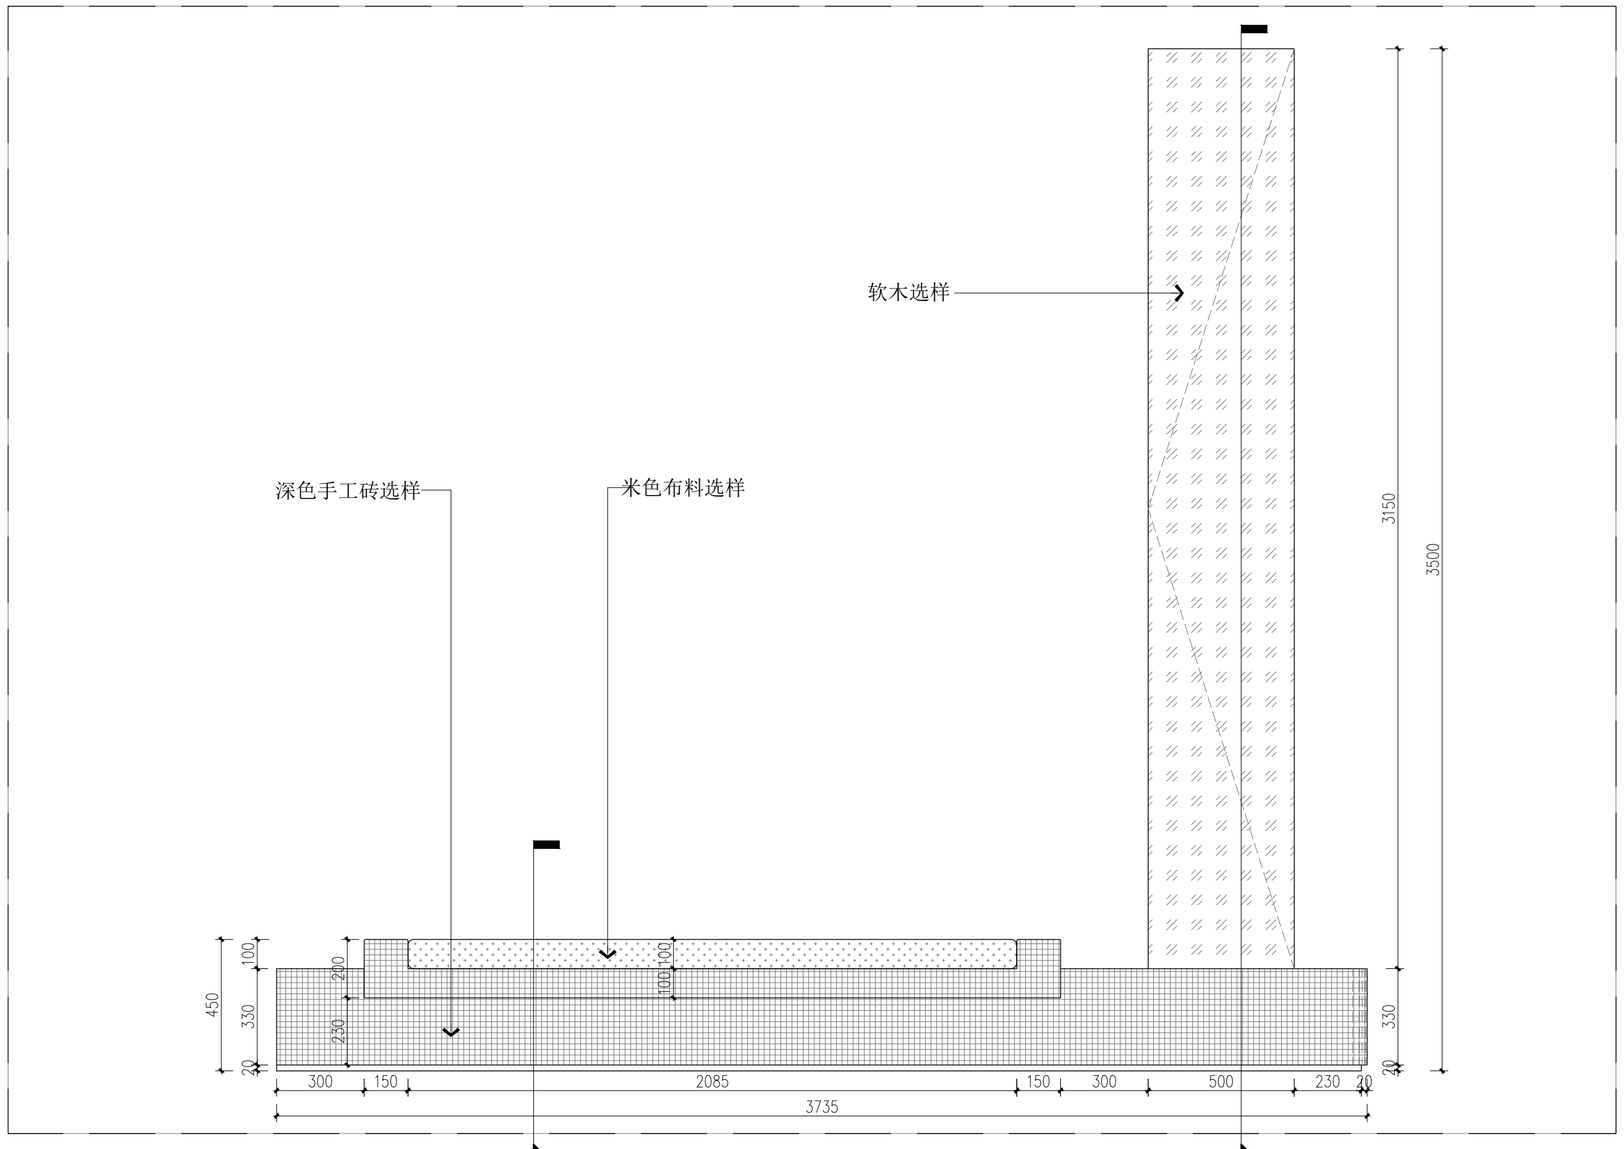

D27 DETAIL 有柜门 D29 D-09 D30 D-09

大样图 SCALE:1/20

会签 建筑 电气 结构 暖通 给排水 动力

ESSENZA ARMONIOSA
architecture
interiors

中国 杭州
TEL: 180 6796 1470
FAX: 180 6796 1470

图注: Exegesis

建设单位 Construction unit

设计单位 Engineering design company

顾问单位 Consultant unit

工程名称 project name

FIONA SHANGHAI

审 定		
审 核		
校 对		
项目负责人		
设 计		
制 图		

图 名

大样图

图 号	D-08
比 例	1:20
日 期	2026.08
专 业	装饰
设计阶段	施工图
版本编号	
设计编号	


出 图 盖 章

此设计图则之版权归杭州光几建筑室内设计有限公司所有 非得建筑师或设计师之书面批准 不得随意将任何部分翻印 切勿以比例量度此图 一切依图内数字所示为准承建人必须在工场核对图内所示数字之准则如发现有任何矛盾处应立即通知建筑师或设计师


ALL DESIGNS ARE THE SOLE PROPERTY OF HANGZHOU , LTD. AND CANNOT BE USED WITHOUT WRITTEN PERMISSION.DO NOT SCALE DRAWING FIGURED DIMENSIONS ARE TO BE FOLLOWED ALL MEASUREMENTS MUST BE CHECKED ON SITE BY THE CONTRACTOR ANYDISCREPANCIES SHOULD BE REPORTED TO THE ARCHITECT OR DESIGNER

A3-420×297


备注：所有大样图需要专业厂家深化，该柜子为鞋柜，内部层板需要做可调节层板

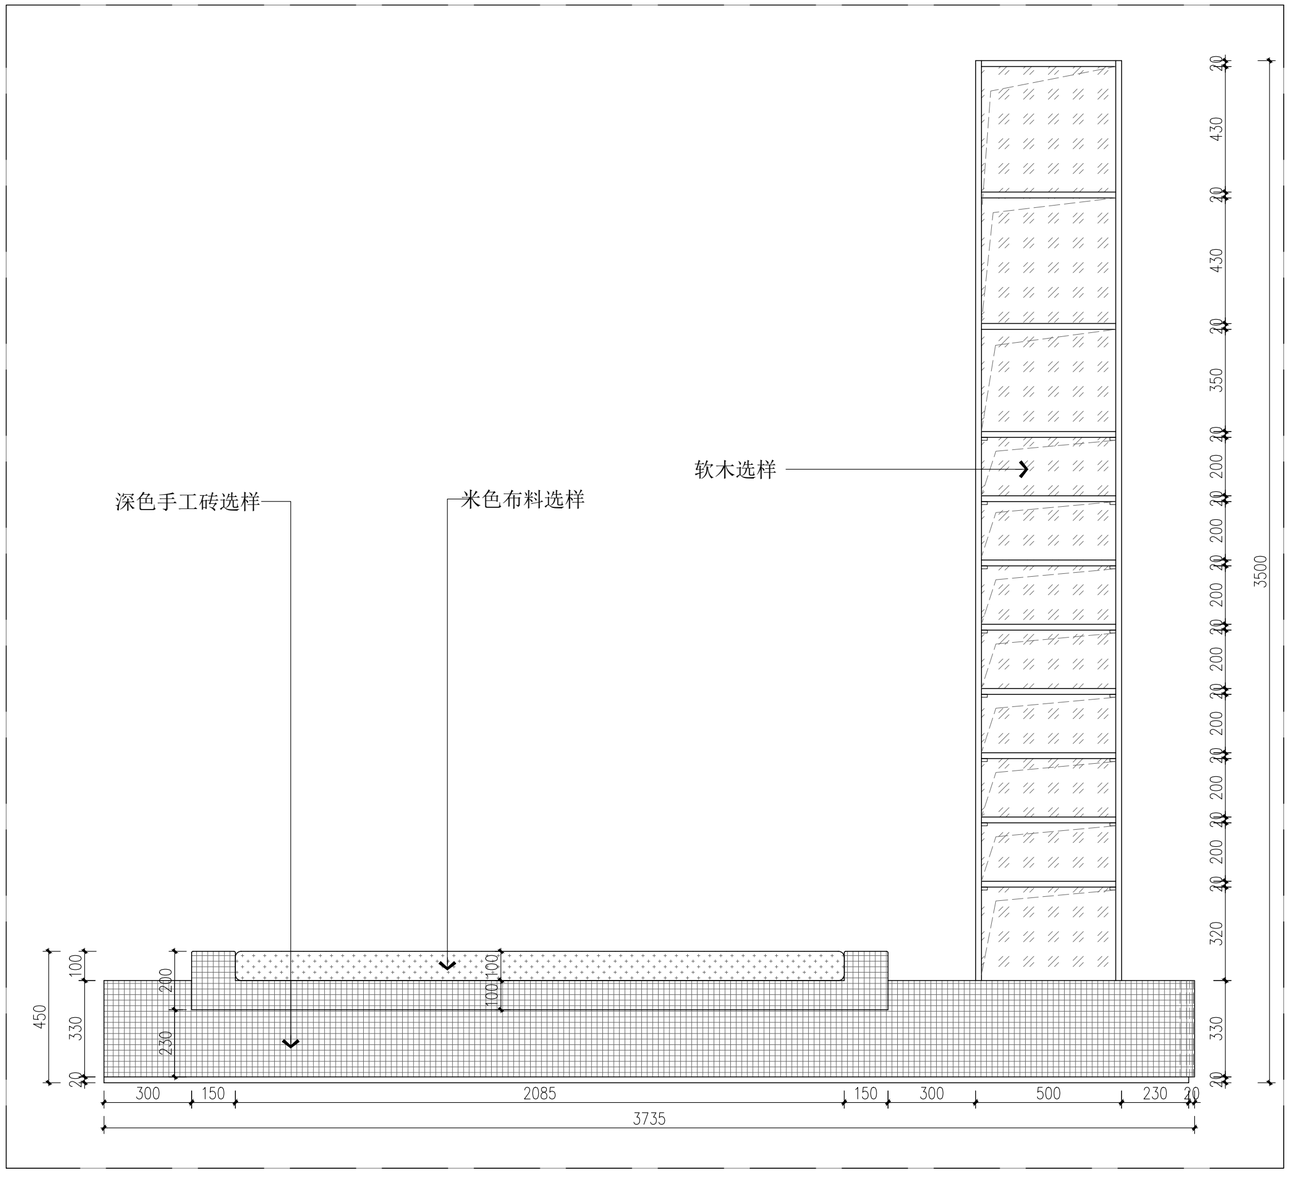

D28 DETAIL 大样图 SCALE:1/20 无柜门

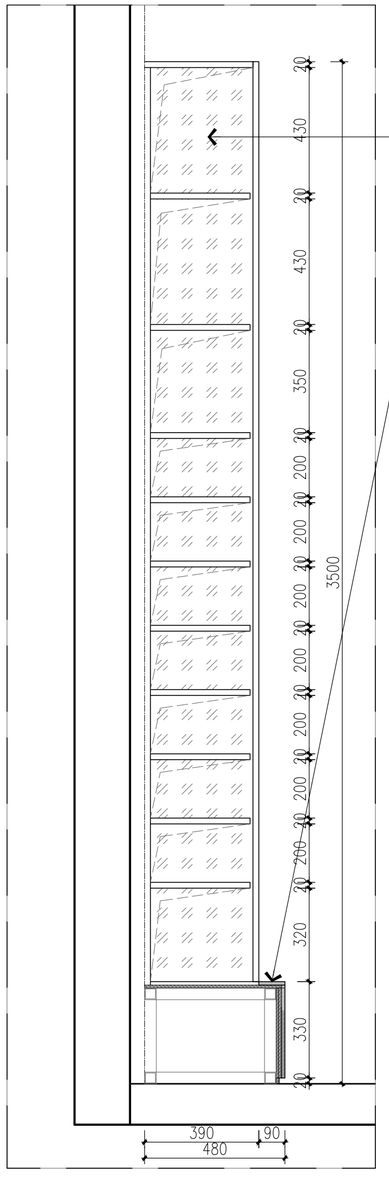

D29 DETAIL 大样图 SCALE:1/20

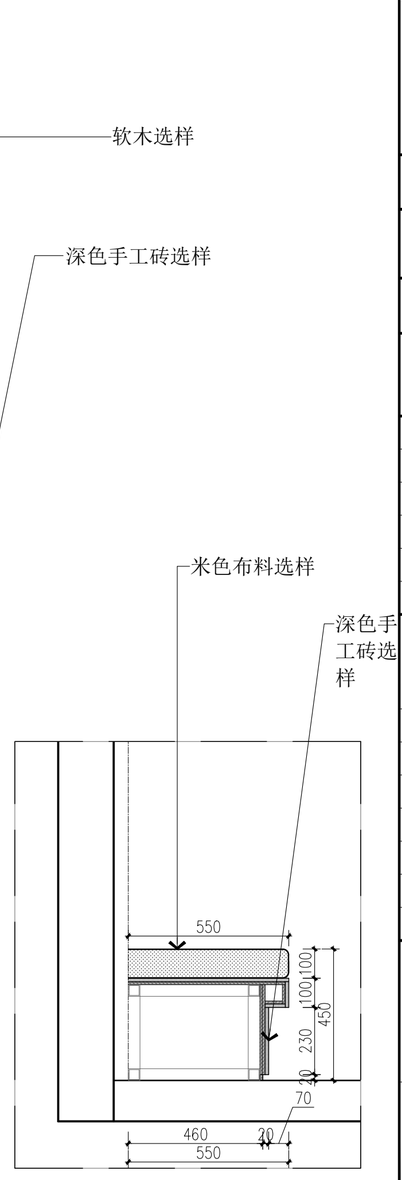

D30 DETAIL 大样图 SCALE:1/20

会签 | 建筑 | 电气 | 结构 | 暖通 | 给排水 | 动力

ESSENZA ARMONIOSA
architecture interiors

中国 杭州
TEL: 180 6796 1470
FAX: 180 6796 1470

图注：Exegesis

建设单位 Construction unit

设计单位 Engineering design company

顾问单位 Consultant unit

工程名称 project name

FIONA SHANGHAI

审 定		
审 核		
校 对		
项目负责人		
设 计		
制 图		

图 名 大样图

图 号	D-09
比 例	1:20
日 期	2026.08
专 业	装饰
设计阶段	施工图
版本编号	
设计编号	


出 图 盖 章

此设计图则之版权归杭州光几建筑室内设计有限公司所有 非得建筑师或设计师之书面批准 不得随意将任何部分翻印 切勿以比例量度此图 一切依图内数字所示为准承建人必须在工场核对图内所示数字之准则如发现有任何矛盾处应立即通知建筑师或设计师

ALL DESIGNS ARE THE SOLE PROPERTY OF HANGZHOU , LTD. AND CANNOT BE USED WITHOUT WRITTEN PERMISSION.DO NOT SCALE DRAWING FIGURED DIMENSIONS ARE TO BE FOLLOWED ALL MEASUREMENTS MUST BE CHECKED ON SITE BY THE CONTRACTOR ANYDISCREPANCIES SHOULD BE REPORTED TO THE ARCHITECT OR DESIGNER


A3-420*297

备注：室外品牌logo制作前，需要现场进行复尺，按照现场尺度制作，该图尺寸仅作参考

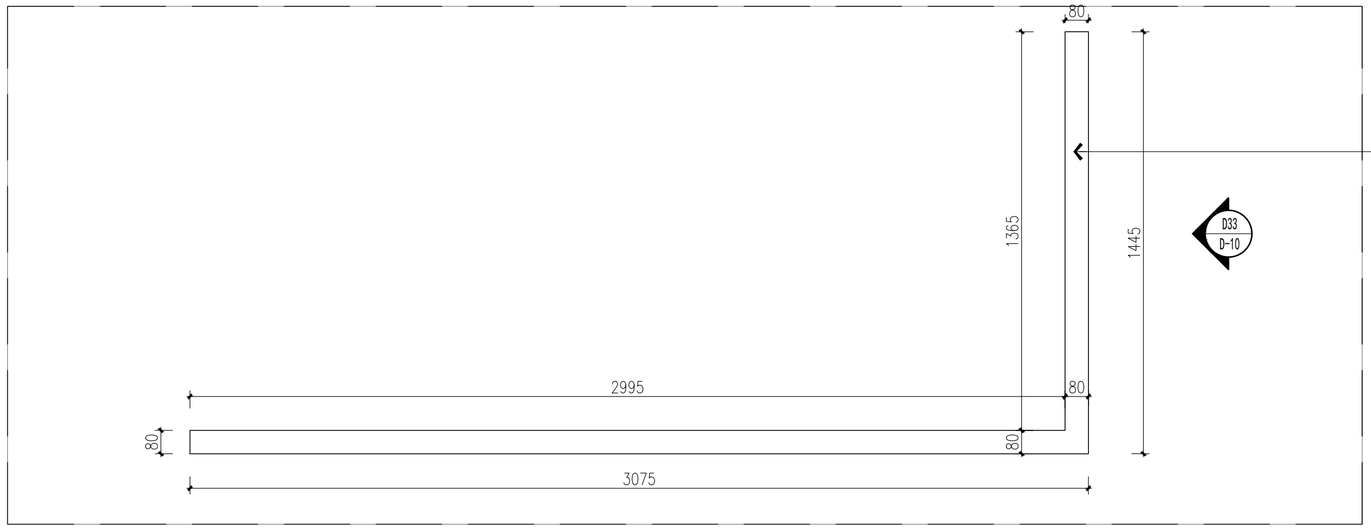


D31 DETAIL 大样图 SCALE:1/20 室外门头logo

D32 D-10

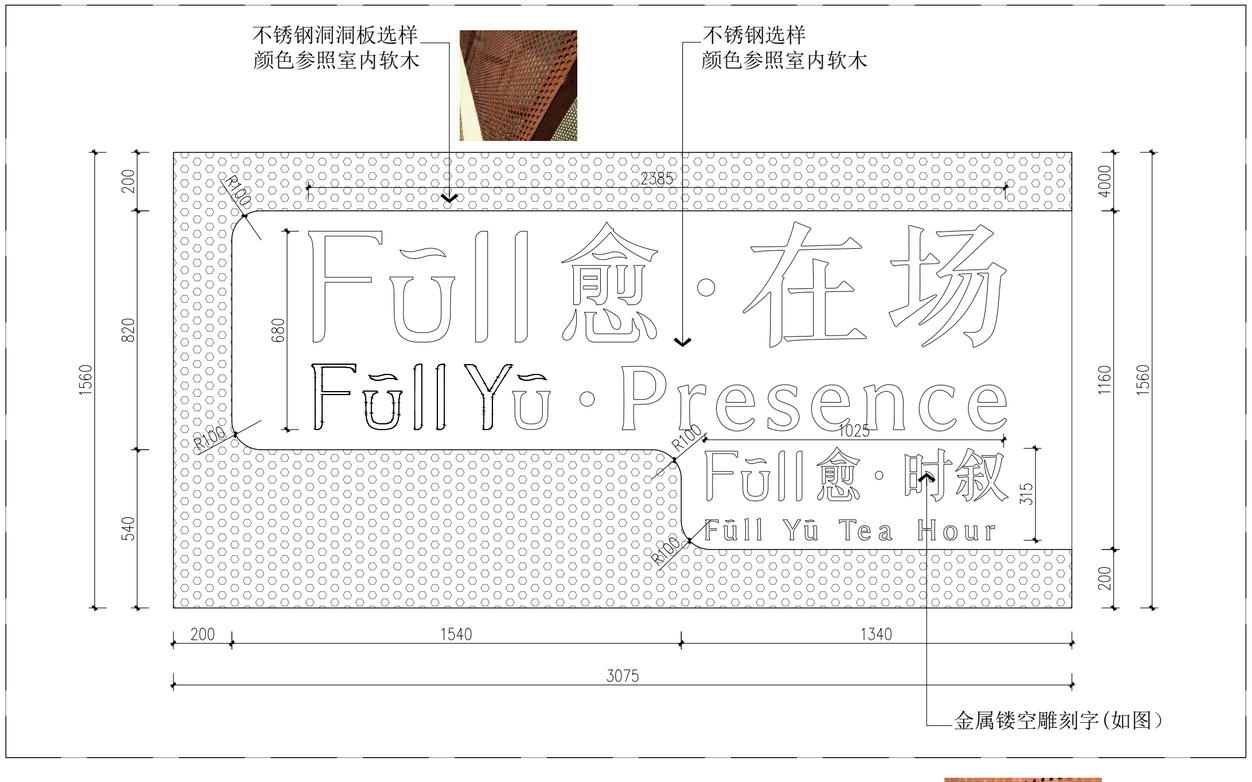

D32 DETAIL 大样图 SCALE:1/20



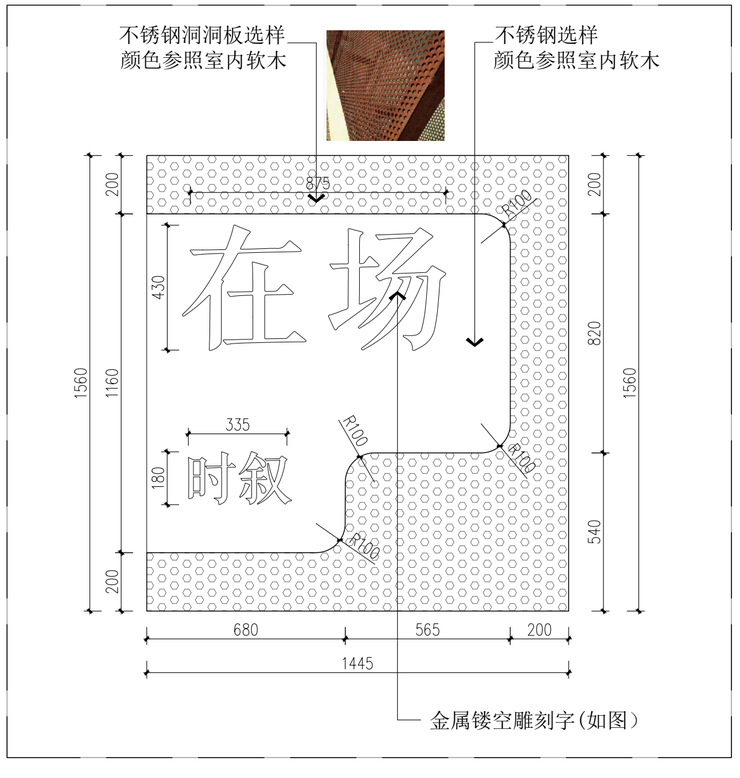

D33 DETAIL 大样图 SCALE:1/20

会签 建筑 电气 结构 暖通 给排水 动力

ESSENZA ARMONIOSA
architecture
interiors

中国 杭州
TEL: 180 6796 1470
FAX: 180 6796 1470

图注：Exegesis

建设单位 Construction unit

设计单位 Engineering design company

顾问单位 Consultant unit

工程名称 project name

FIONA SHANGHAI

审 定		
审 核		
校 对		
项目负责人		
设 计		
制 图		

图 名

大样图

图 号	D-10
比 例	1:20
日 期	2026.08
专 业	装饰
设计阶段	施工图
版本编号	
设计编号	


出 图 盖 章

此设计图则之版权归杭州光几建筑室内设计有限公司所有 非得建筑师或设计师之书面批准 不得随意将任何部分翻印 切勿以比例量度此图 一切依图内数字所示为准承建人必须在工场核对图内所示数字之准则如发现有任何矛盾处应立即通知建筑师或设计师


ALL DESIGNS ARE THE SOLE PROPERTY OF HANGZHOU , LTD. AND CANNOT BE USED WITHOUT WRITTEN PERMISSION.DO NOT SCALE DRAWING FIGURED DIMENSIONS ARE TO BE FOLLOWED ALL MEASUREMENTS MUST BE CHECKED ON SITE BY THE CONTRACTOR ANYDISCREPANCIES SHRULD BE REPORTED TO THE ARCHITECT OR DESIGNER

A3-420*297


备注：所有大样图需要专业厂家深化，此处为可折叠玻璃小桌板

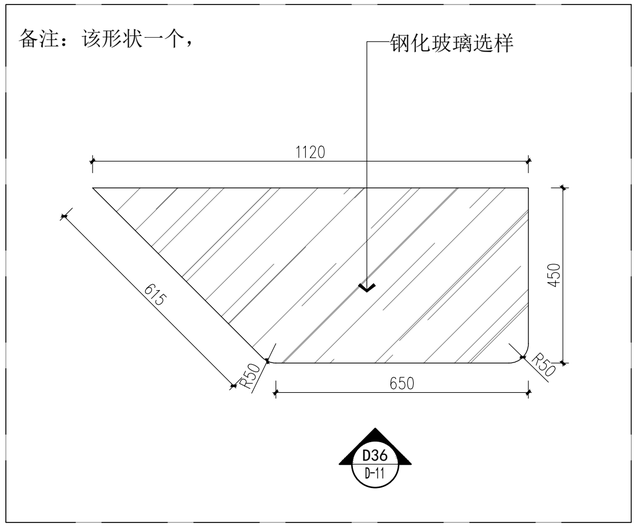


D34 DETAIL 大样图 SCALE:1/15

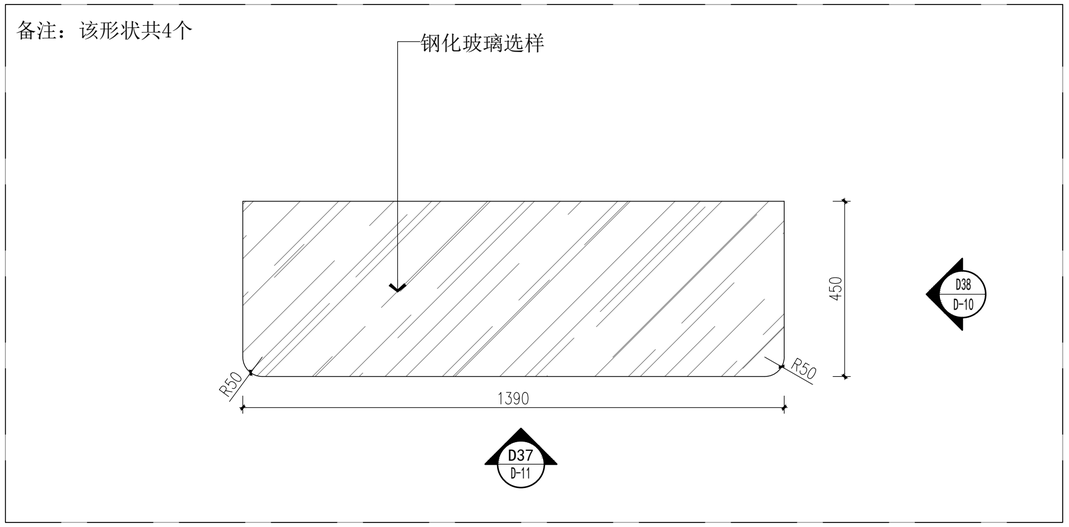


D35 DETAIL 大样图 SCALE:1/15

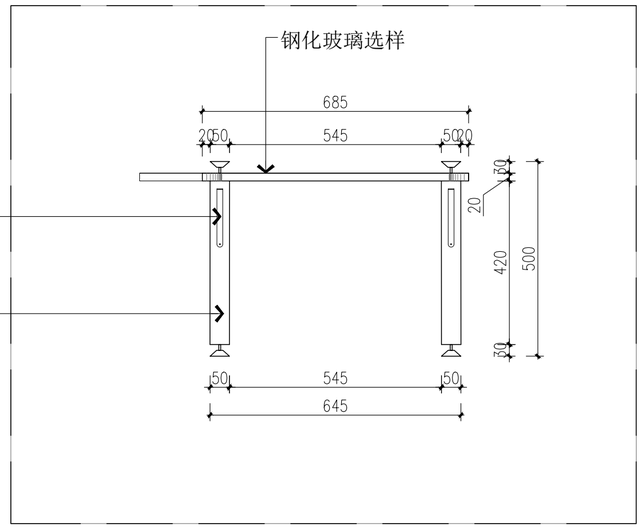

D36 DETAIL 大样图 SCALE:1/15

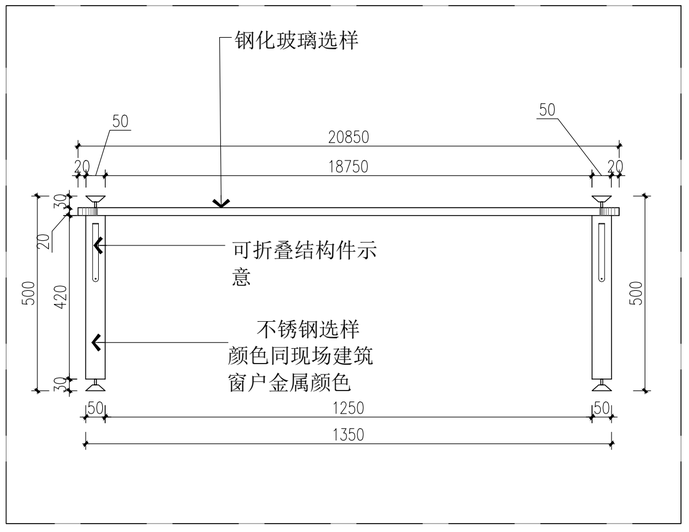

D37 DETAIL 大样图 SCALE:1/15

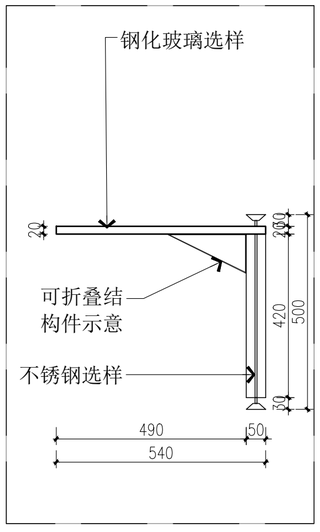

D38 DETAIL 大样图 SCALE:1/15

给排水 | 动 力
结 构 | 暖 通
建 筑 | 电 气
会 签

ESSENZA ARMONIOSA
architecture interiors

中国 杭州
TEL: 180 6796 1470
FAX: 180 6796 1470

图注：Exegesis

建设单位 Construction unit

设计单位 Engineering design company

顾问单位 Consultant unit

工程名称 project name

FIONA SHANGHAI

审 定		
审 核		
校 对		
项目负责人		
设 计		
制 图		

图 名

大样图

图 号	D-11
比 例	1:15
日 期	2026.08
专 业	装饰
设计阶段	施工图
版本编号	
设计编号	


出 图 盖 章

此设计图则之版权归杭州光几建筑室内设计有限公司所有 非得建筑师或设计师之书面批准 不得随意将任何部分翻印 切勿以比例量度此图 一切依图内数字所示为准承建人必须在工场核对图内所示数字之准则如发现有任何矛盾处应立即通知建筑师或设计师


ALL DESIGNS ARE THE SOLE PROPERTY OF HANGZHOU , LTD. AND CANNOT BE USED WITHOUT WRITTEN PERMISSION.DO NOT SCALE DRAWING. FIGURED DIMENSIONS ARE TO BE FOLLOWED. ALL MEASUREMENTS MUST BE CHECKED ON SITE BY THE CONTRACTOR. ANYDISCREPANCIES SHOULD BE REPORTED TO THE ARCHITECT OR DESIGNER.

A3-420*297


备注：所有大样图需要专业厂家深化，此处为可折叠玻璃小桌板

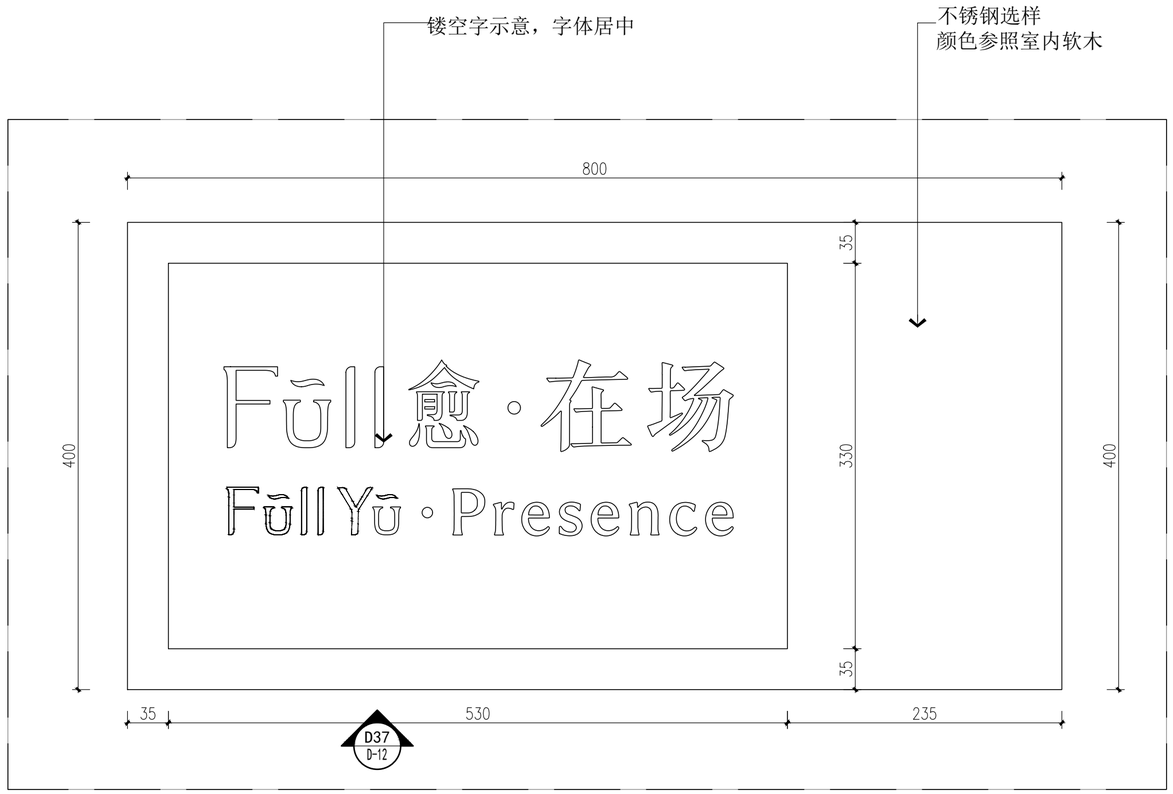

D39 DETAIL
大样图 SCALE:1/15

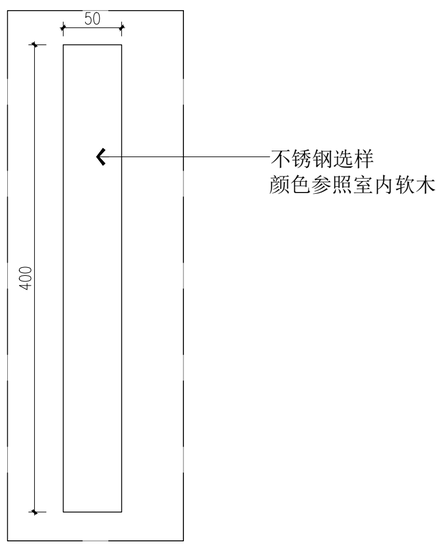

D40 DETAIL
大样图 SCALE:1/15

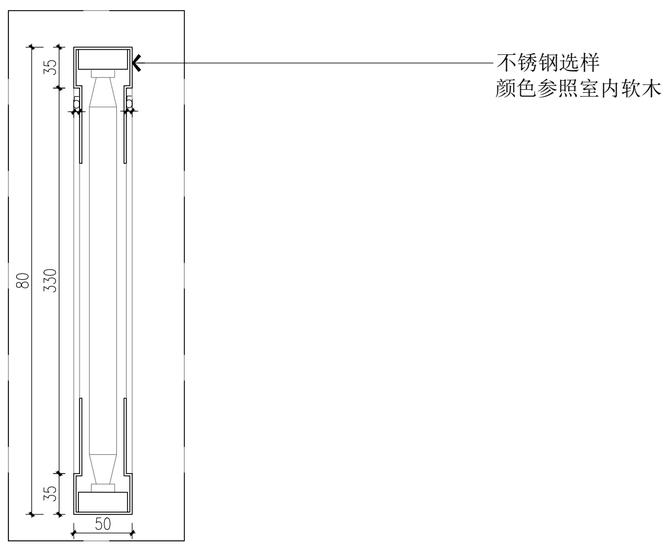

D41 DETAIL
大样图 SCALE:1/15

会签 | 建筑 | 电气 | 结构 | 暖通 | 给排水 | 动力

ESSENZA ARMONIOSA
architecture interiors

中国 杭州
TEL: 180 6796 1470
FAX: 180 6796 1470

图注：Exegesis

建设单位 Construction unit

设计单位 Engineering design company

顾问单位 Consultant unit

工程名称 project name
FIONA SHANGHAI

审 定		
审 核		
校 对		
项目负责人		
设 计		
制 图		

图 名
大样图


图 号	D-12
比 例	1:15
日 期	2026.08
专 业	装饰
设计阶段	施工图
版本编号	
设计编号	

出 图 盖 章


此设计图则之版权归杭州光几建筑室内设计有限公司所有 非得建筑师或设计师之书面批准 不得随意将任何部分翻印 切勿以比例量度此图 一切依图内数字所示为准承建人必须在工场核对图内所示数字之准则如发现有任何矛盾处应立即通知建筑师或设计师

ALL DESIGNS ARE THE SOLE PROPERTY OF HANGZHOU . LTD. AND I CANNOT BE USED WITHOUT WRITTEN PERMISSION.DO NOT SCALE DRAWING FIGURED DIMENSIONS ARE TO BE FOLLOWED. ALL MEASUREMENTS MUST BE CHECKED ON SITE BY THE CONTRACTOR. ANYDISCREPANCIES SHOULD BE REPORTED TO THE ARCHITECT OR DESIGNER


A3-420*297

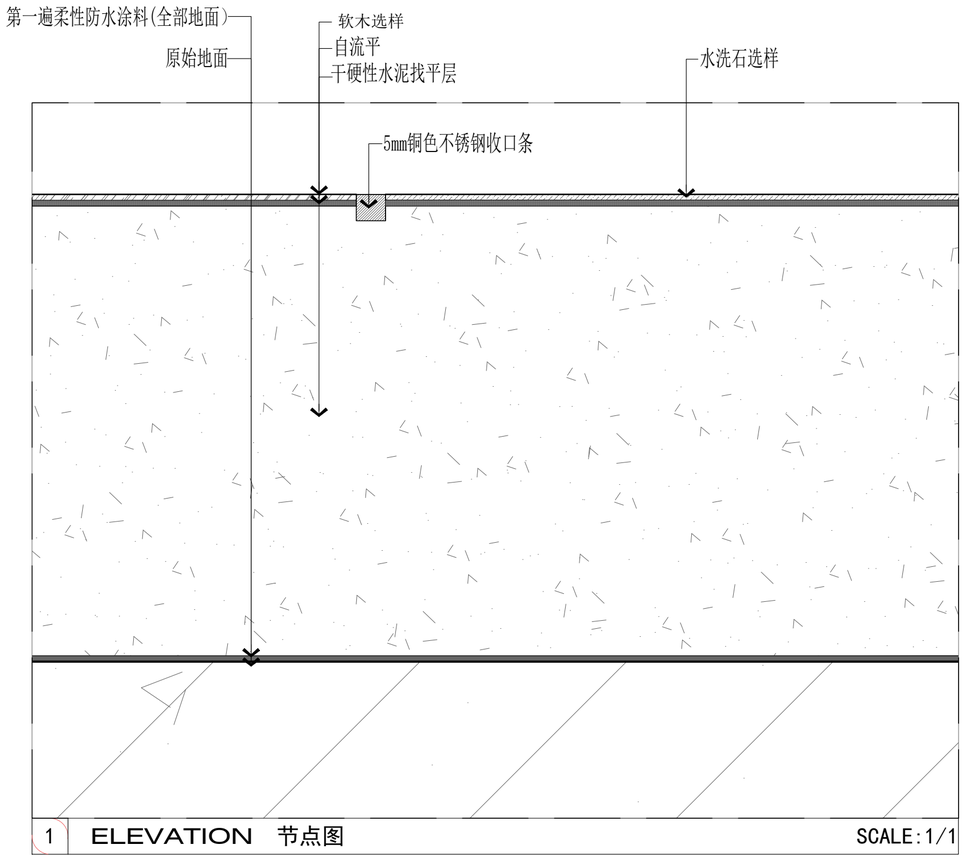

1 ELEVATION 节点图 SCALE:1/1

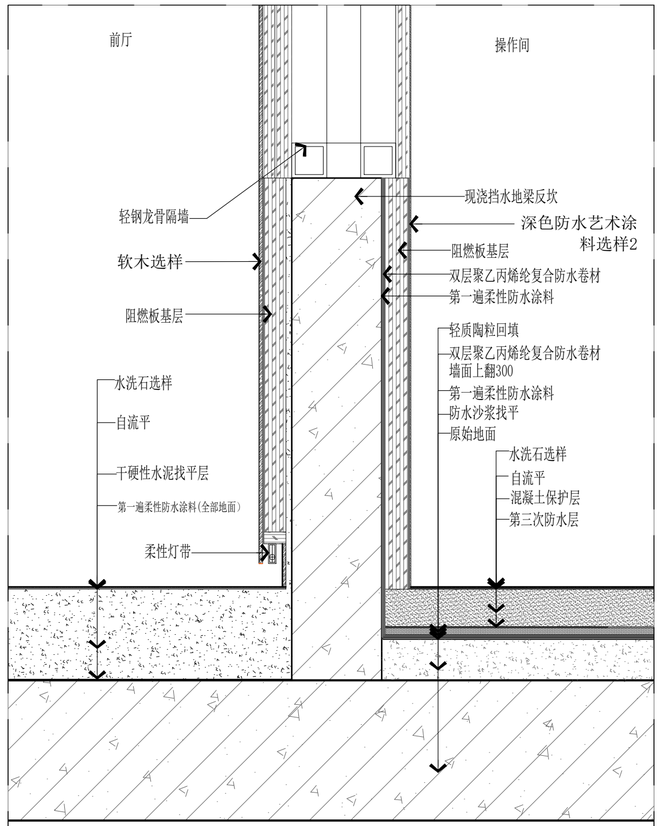

3 ELEVATION 节点图 SCALE:1/5

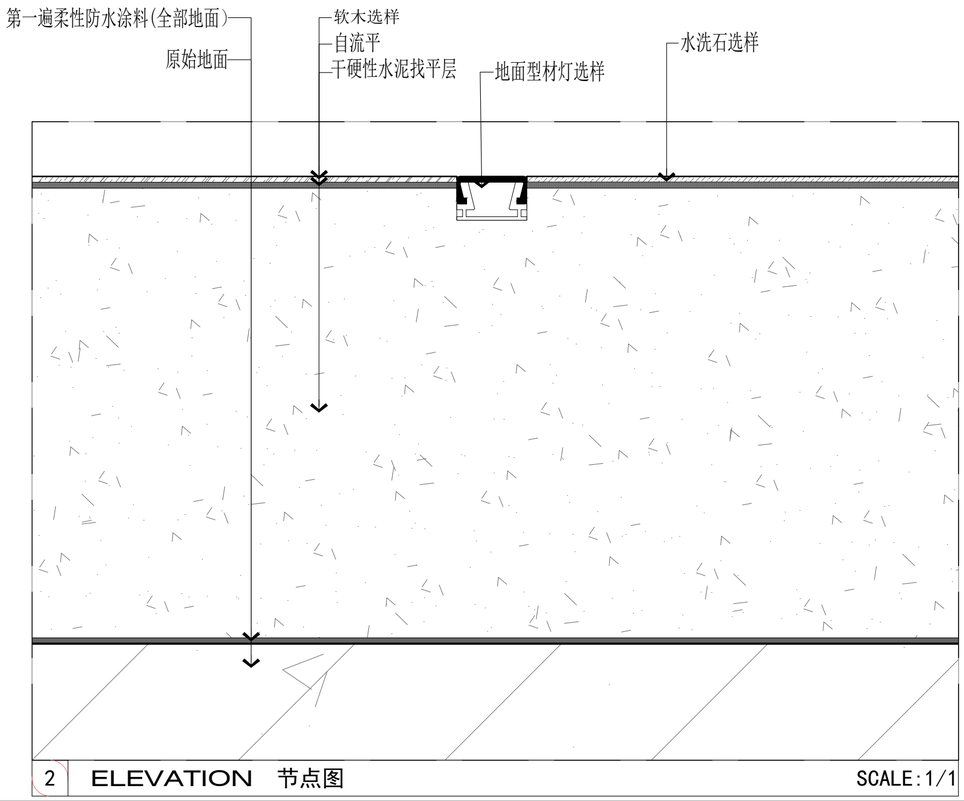

2 ELEVATION 节点图 SCALE:1/1

会签 建筑 电气 结构 暖通 给排水 动力

ESSENZA ARMONIOSA
architecture interiors

中国 杭州
TEL: 180 6796 1470
FAX: 180 6796 1470

图注: Exegesis

建设单位 Construction unit

设计单位 Engineering design company

顾问单位 Consultant unit

工程名称 project name

FIONA SHANGHAI

审 定		
审 核		
校 对		
项目负责人		
设 计		
制 图		

图 名 节点图

图 号	JD-01
比 例	
日 期	2026.08
专 业	装饰
设计阶段	施工图
版本编号	
设计编号	


出 图 盖 章


此设计图则之版权归杭州光几建筑室内设计有限公司所有 非得建筑师或设计师之书面批准 不得随意将任何部分翻印 切勿以比例量度此图 一切依图内数字所示为准承建人必须在工场核对图内所示数字之准则如发现有任何矛盾处应立即通知建筑师或设计师

ALL DESIGNS ARE THE SOLE PROPERTY OF HANGZHOU ... LTD. AND I CANNOT BE USED WITHOUT WRITTEN PERMISSION.DO NOT SCALE DRAWING FIGURED DIMENSIONS ARE TO BE FOLLOWED ALL MEASUREMENTS MUST BE CHECKED ON SITE BY THE CONTRACTOR ANYDISCREPANCIES SHOULD BE REPORTED TO THE ARCHITECT OR DESIGNER


A3-420*297

会签 | 建筑 | 电气 | 结构 | 暖通 | 给排水 | 动力

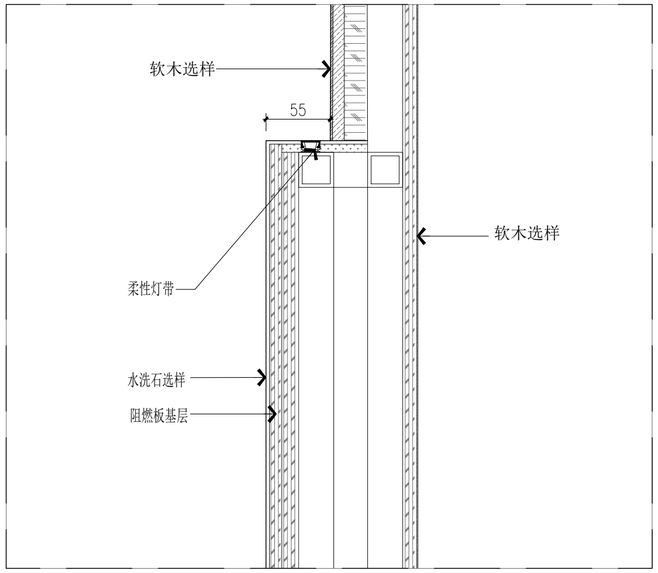

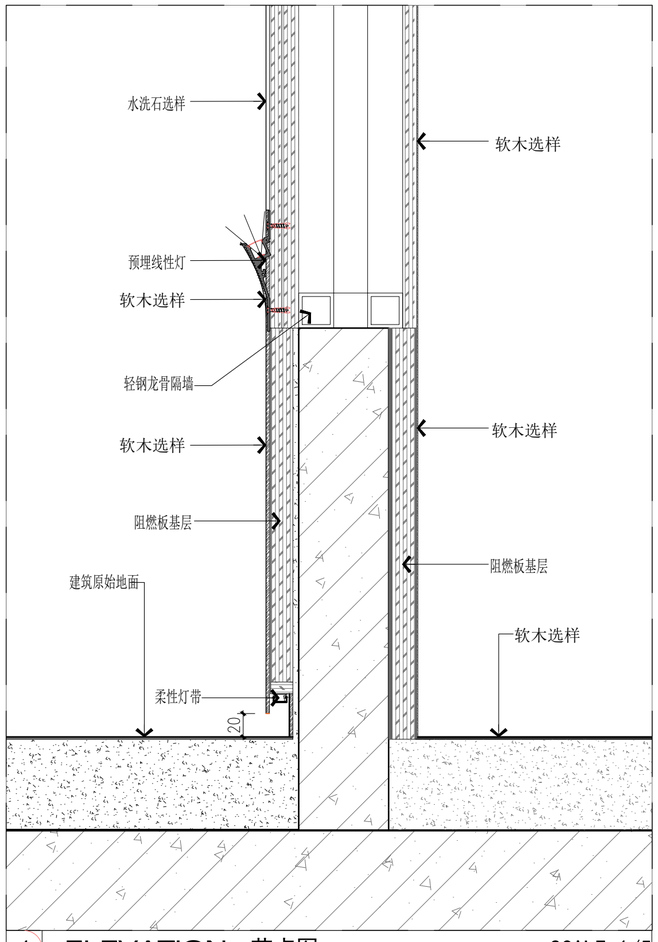

4 ELEVATION 节点图 SCALE:1/5

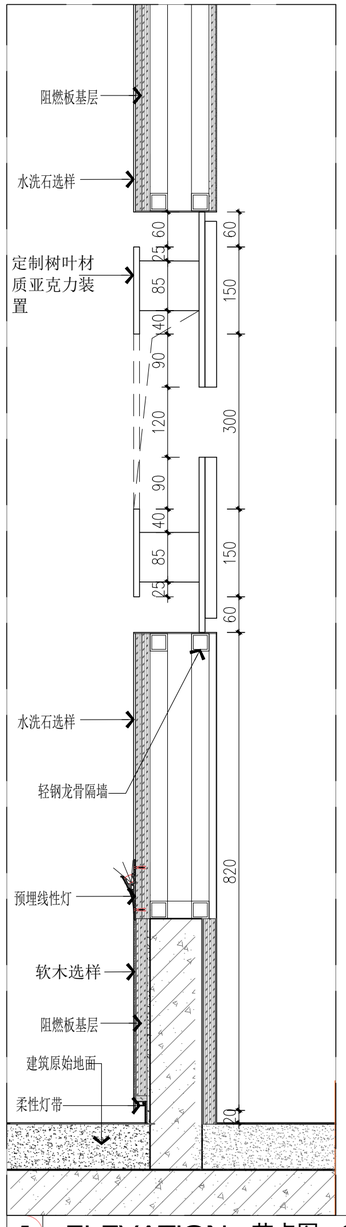

5 ELEVATION 节点图 SCALE:1/10

ESSENZA ARMONIOSA
architecture
interiors

中国 杭州
TEL: 180 6796 1470
FAX: 180 6796 1470

图注: Exegesis

建设单位 Construction unit

设计单位 Engineering design company

顾问单位 Consultant unit

工程名称 project name

FIONA SHANGHAI

审 定		
审 核		
校 对		
项目负责人		
设 计		
制 图		

图 名

节点图


图 号	JD-02
比 例	
日 期	2026.08
专 业	装饰
设计阶段	施工图
版本编号	
设计编号	

出 图 盖 章


此设计图则之版权归杭州光几建筑室内设计有限公司所有 非得建筑师或设计师之书面批准 不得随意将任何部分翻印 切勿以比例量度此图 一切依图内数字所示为准承建人必须在工场核对图内所示数字之准则如发现有任何矛盾处应立即通知建筑师或设计师

ALL DESIGNS ARE THE SOLE PROPERTY OF HANGZHOU , LTD. AND CANNOT BE USED WITHOUT WRITTEN PERMISSION.DO NOT SCALE DRAWING FIGURED DIMENSIONS ARE TO BE FOLLOWED.ALL MEASUREMENTS MUST BE CHECKED ON SITE BY THE CONTRACTOR.ANYDISCREPANCIES SHOULD BE REPORTED TO THE ARCHITECT OR DESIGNER.


会签 | 建筑 | 电气 | 结构 | 暖通 | 给排水 | 动力

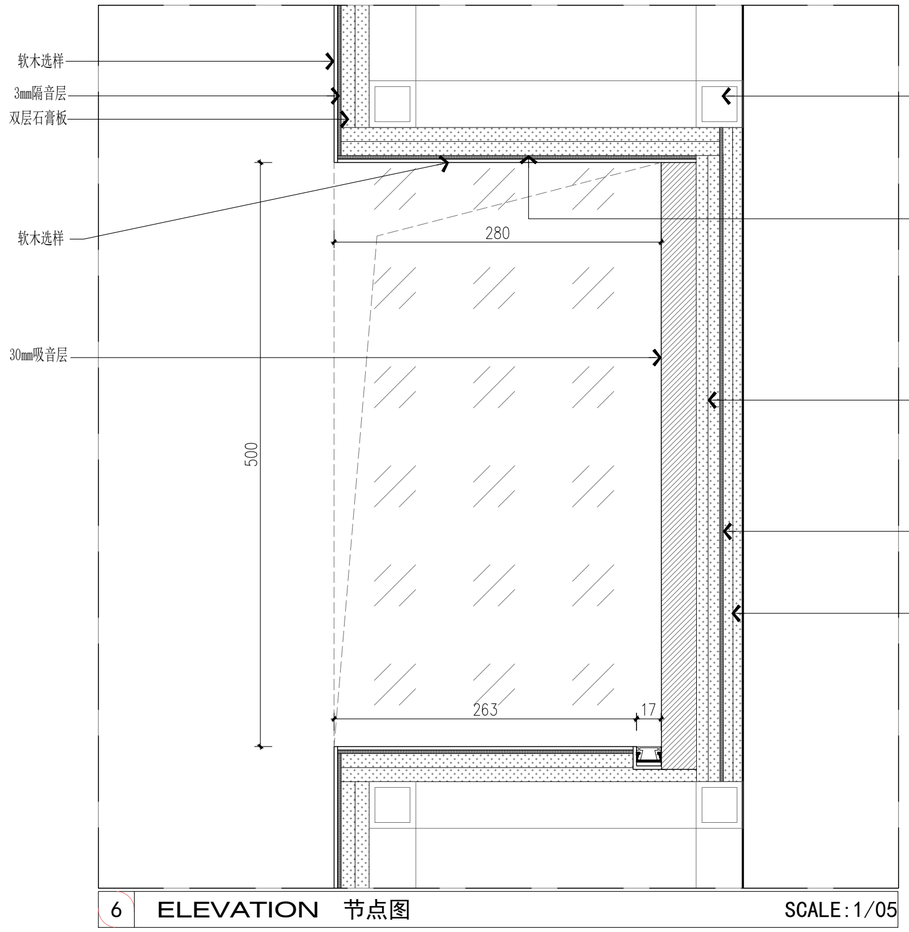


6 ELEVATION 节点图 SCALE:1/05

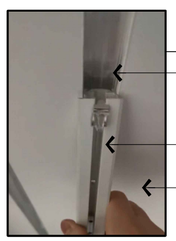


安装图示

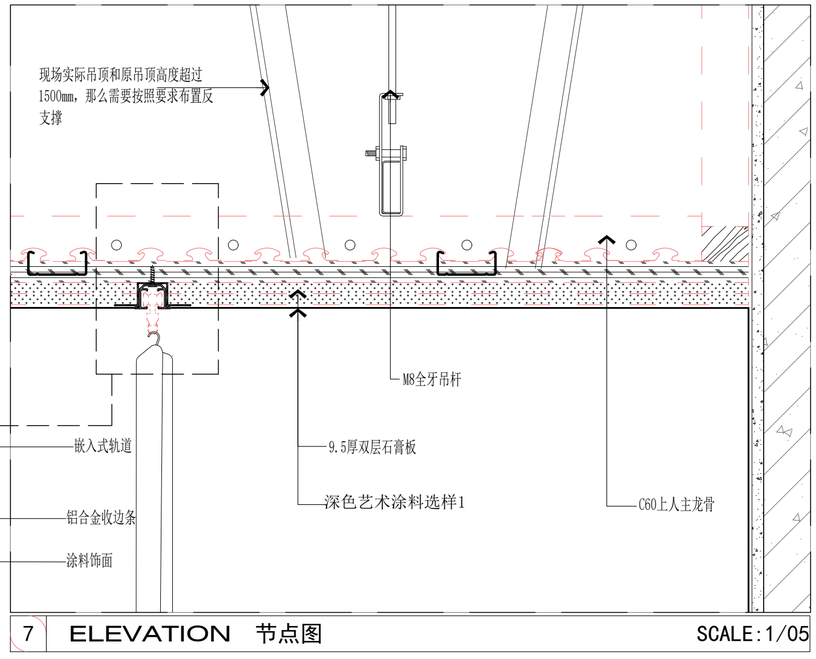

7 ELEVATION 节点图 SCALE:1/05

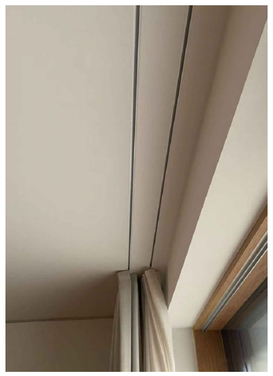

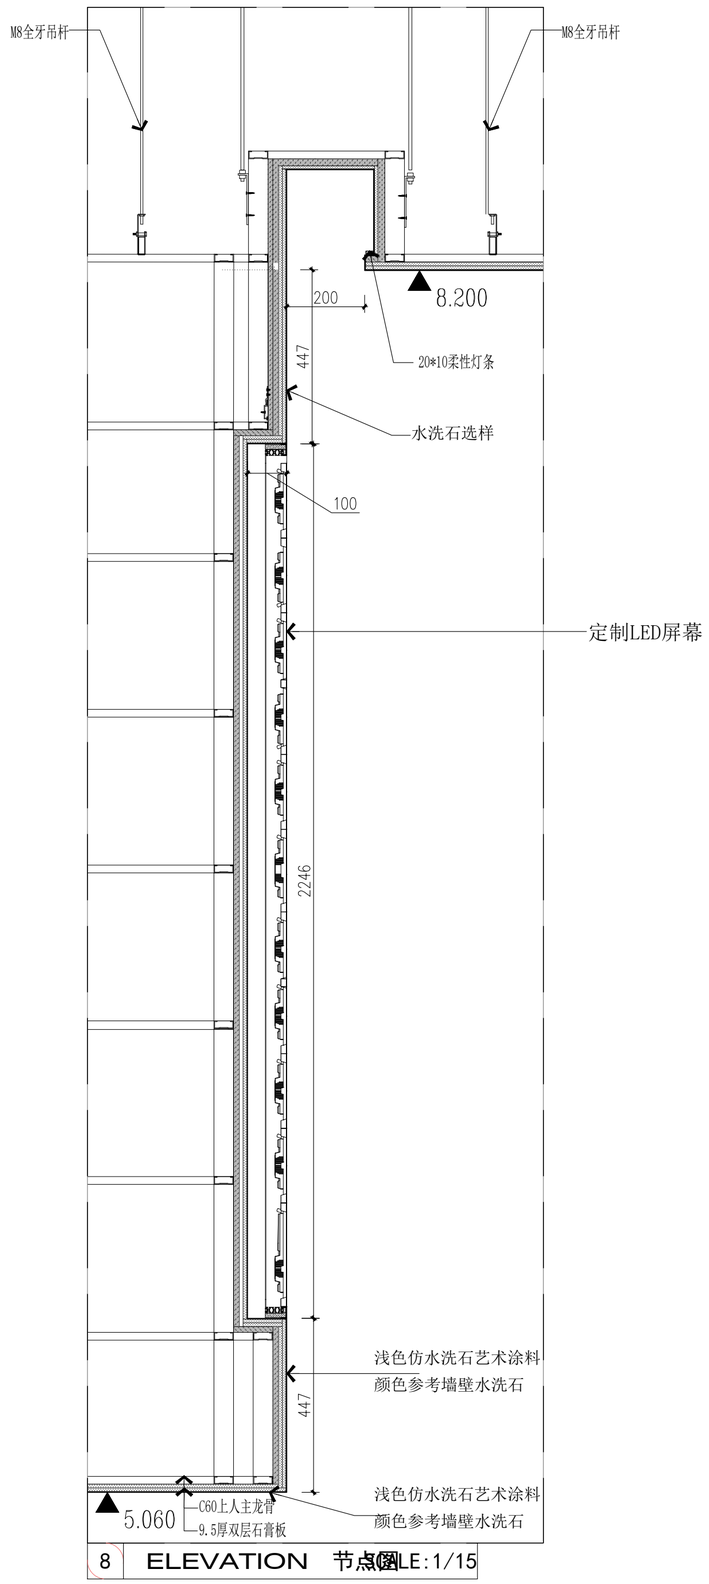

8 ELEVATION 节点图 SCALE:1/15

ESSENZA ARMONIOSA
architecture interiors

中国 杭州
TEL: 180 6796 1470
FAX: 180 6796 1470

图注: Exegesis

建设单位 Construction unit

设计单位 Engineering design company

顾问单位 Consultant unit

工程名称 project name

FIONA SHANGHAI

审 定		
审 核		
校 对		
项目负责人		
设 计		
制 图		

图 名

节点图

图 号	JD-03
比 例	
日 期	2026.08
专 业	装饰
设计阶段	施工图
版本编号	
设计编号	

出 图 盖 章

此设计图则之版权归杭州光几建筑室内设计有限公司所有 非得建筑师或设计师之书面批准 不得随意将任何部分翻印 切勿以比例量度此图 一切依图内数字所示为准承建人必须在工场核对图内所示数字之准则如发现有任何矛盾处应立即通知建筑师或设计师

ALL DESIGNS ARE THE SOLE PROPERTY OF HANGZHOU , LTD. AND CANNOT BE USED WITHOUT WRITTEN PERMISSION.DO NOT SCALE DRAWING FIGURED DIMENSIONS ARE TO BE FOLLOWED ALL MEASUREMENTS MUST BE CHECKED ON SITE BY THE CONTRACTOR ANYDISCREPANCIES SHOULD BE REPORTED TO THE ARCHITECT OR DESIGNER

A3-420*297